

GURUGRAM

LAYOUT PLAN OF HOUSING SCHEME UNDER
"MUKHYAMANTRI GRAMIN AWAS YOJANA-EXTENSION"
(MMGAY-E) AREA MEASURING 2.837 ACRES,
BEARING KHASRA NO.66//12, 13 & 22 IN THE REVENUE
ESTATE OF VILLAGE MAU TEHSIL PATAUDI DISTRICT
GURUGRAM.

DETAILS OF PLOTTED AREA :-

SR.NO.	PARTICULAR	SIZE	NOS.	AREA
1.	RESI. PLOT	6.71X12.47M	73	6108.18 SQM
2.	MAHILA CHOUPAL	15.51X12.47	1	193.41 SQM.

DETAILS OF AREA :-

AREA OF SCHEME = 2.866 ACRES (11602.2519 SQM.)
 AREA OF FUTURE EXTENSION LAND = 0.152 ACRES (613.49 SQM.)
 TOTAL PLANNED AREA = 2.714 ACRES (10983.15 SQM.)
 AREA UNDER PLOTS = 6301.59 SQM
 AREA UNDER PARKS/OPEN SPACES = 697.40 SQM

LEGEND:-


SCHEME BOUNDARY
KILLA LINE
PARK / OPEN SPACES

MB (MILK BOOTH)
UGT (UNDERGROUND WATER TANK)

UG STP (UNDERGROUND SEWERAGE
TREATMENT PLANT)

11 KV HT LINE

HT STBACK LINE

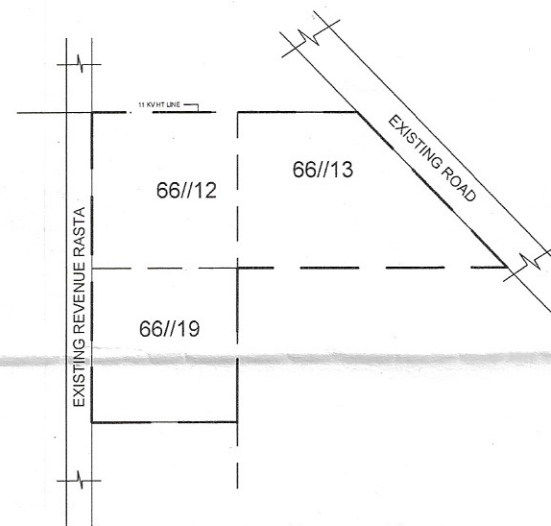

LOCATION MAP NOT FOR SCALE



SCALE: 1CM = 5MTR.

DRG. NO. D.T.P (G) :- 2707/2024

DATED :- 12-12-2024

DRAWN BY :- 


CHECKED BY :- 

PLANNING ASSISTANT :-

ASSTT. TOWN PLANNER :-

DEPARTMENT OF TOWN AND COUNTRY PLANNING, HARYANA

NOTE : ALL DIMENSIONS ARE IN 'METER'

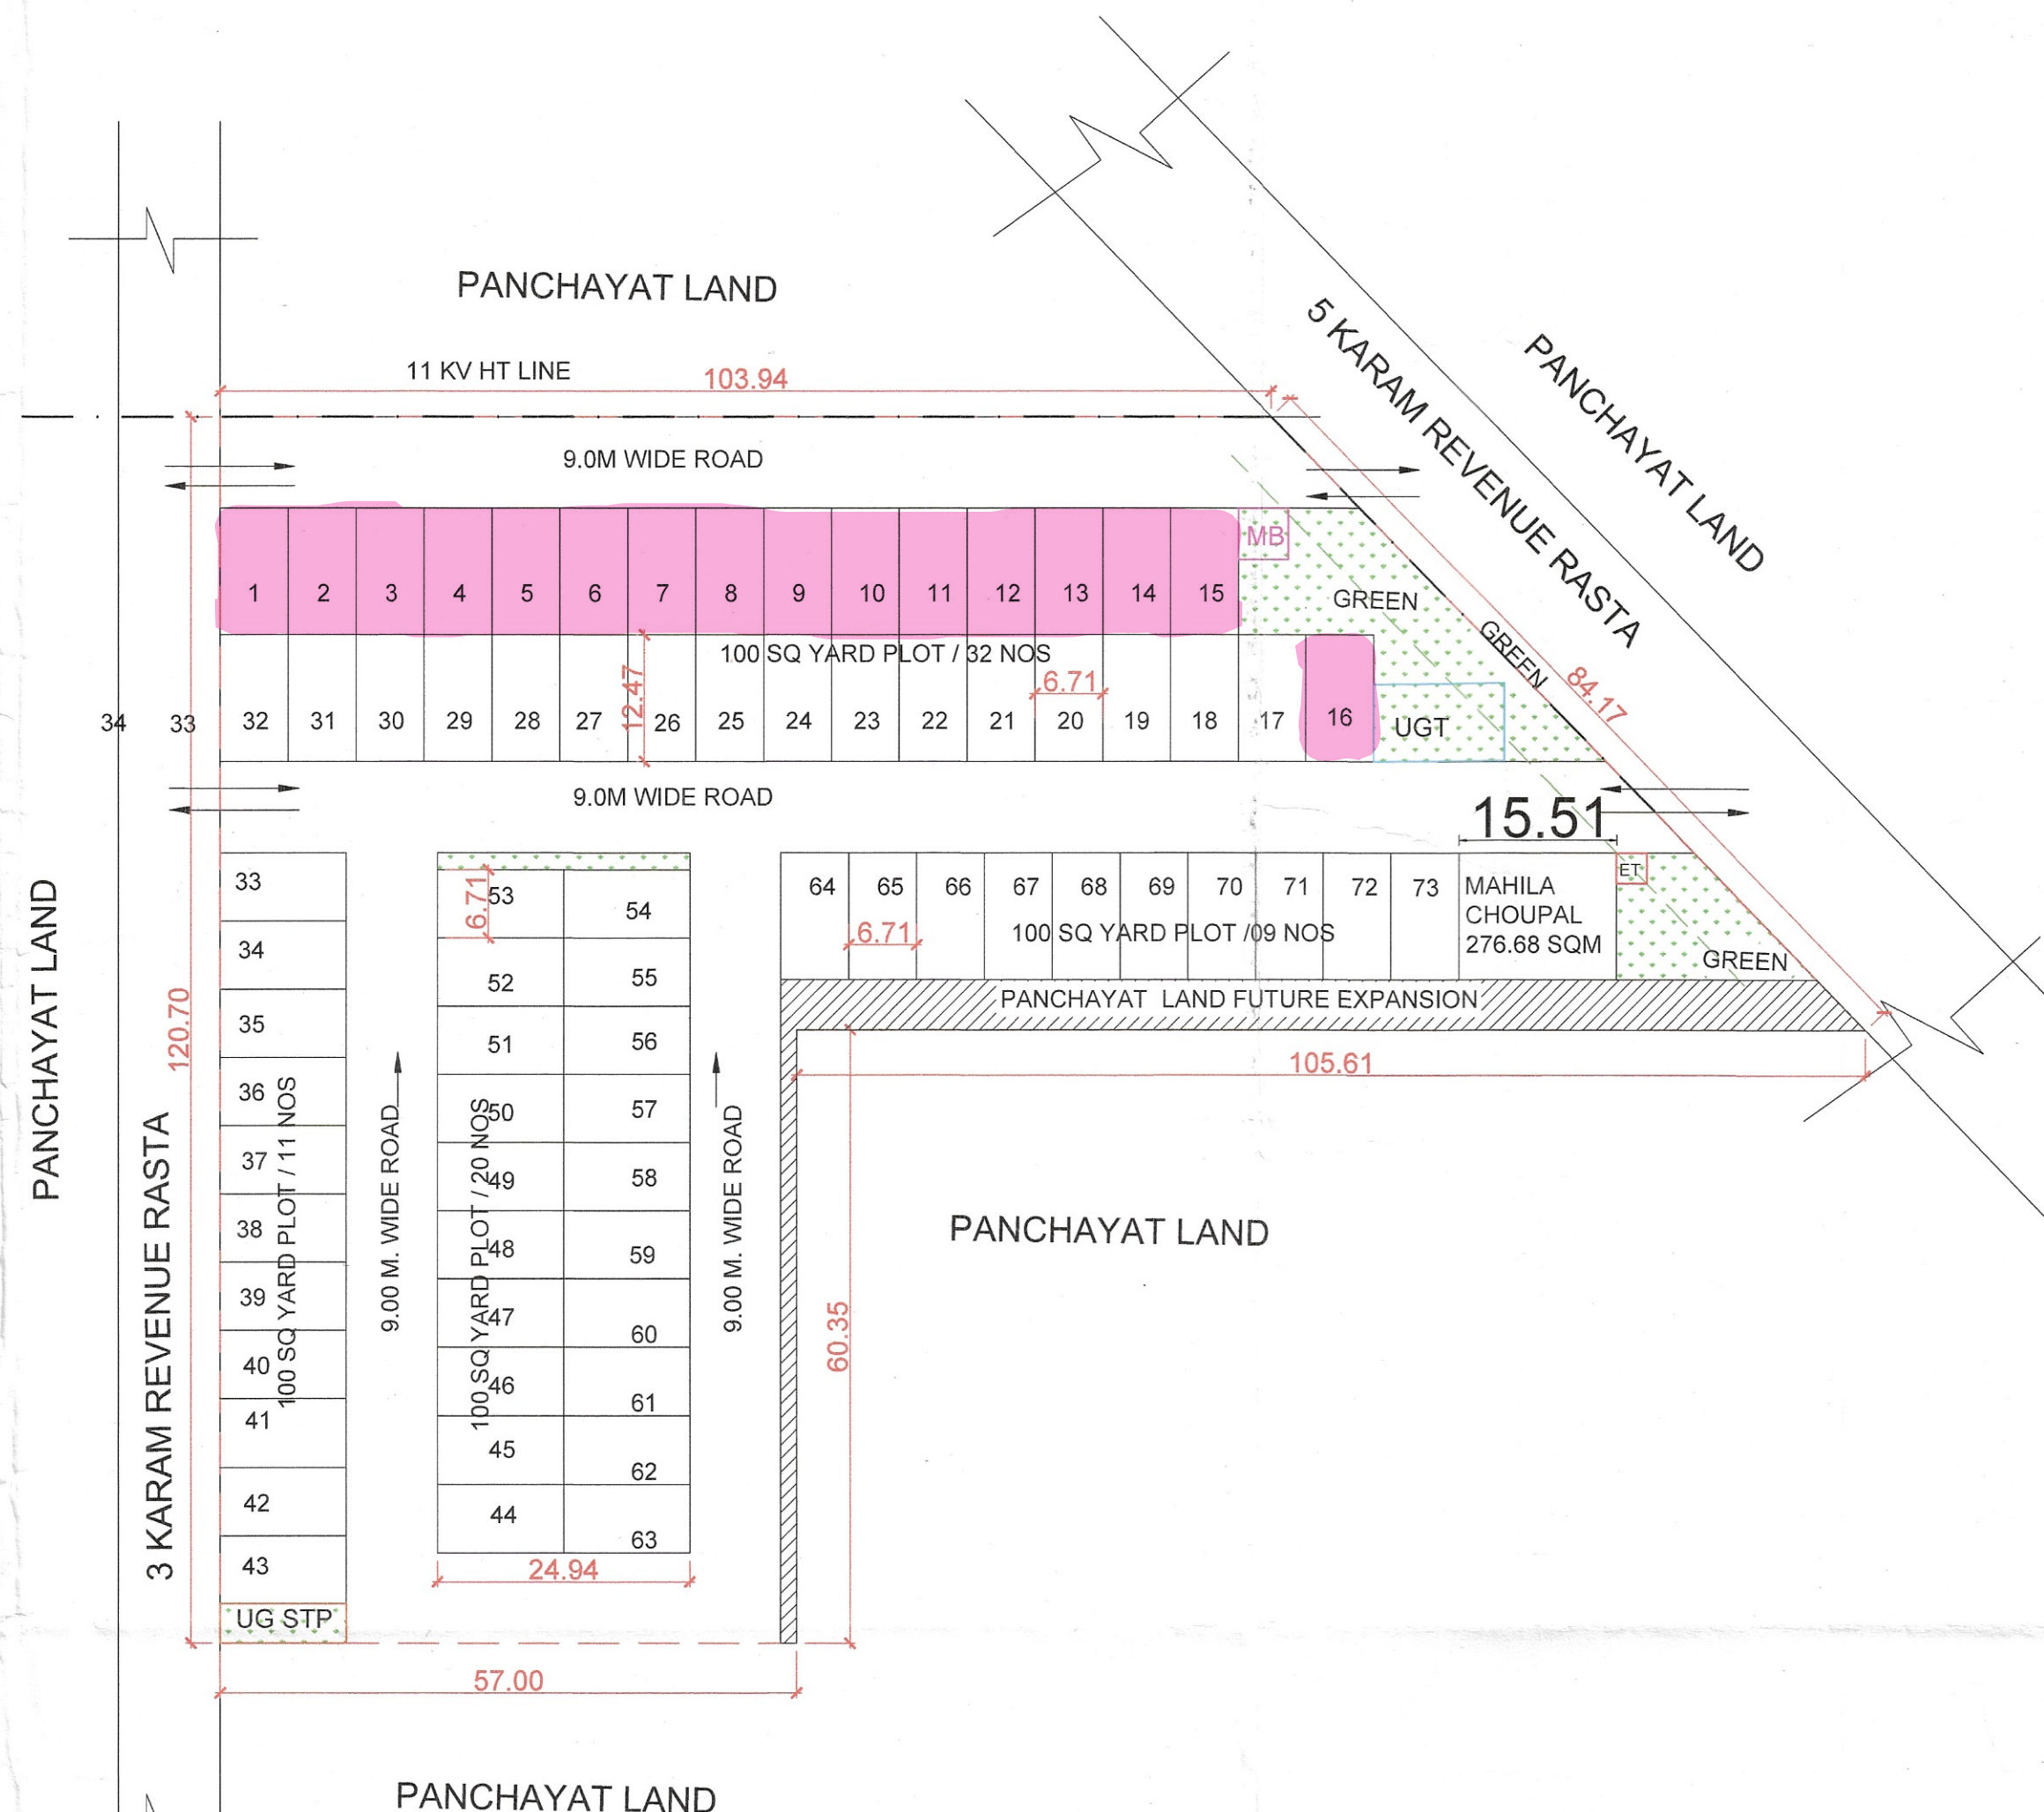

SUB DIVISIONAL OFFICER,
PATAUDI BLOCK , DISTT GURUGRAM
PANCHAYATI RAJ DEPARTMENT,
HARYANA CHANDIGARH

B.D.P.O., PATAUDI BLOCK
DISTT GURUGRAM

DISTRICT TOWN PLANNER, GURUGRAM
TOWN & COUNTRY PLANNING DEPARTMENT,
HARYANA CHANDIGARH

SENIOR TOWN PLANNER, GURUGRAM
TOWN & COUNTRY PLANNING DEPARTMENT
HARYANA CHANDIGARH