

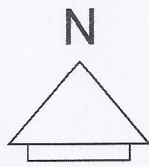
LAYOUT PLAN OF MUKHYA MANTRI GRAMIN
AWAS YOJNA - EXTENSION SCHEME IN VILLAGE
KALAWATI, TEHSIL SAFIDON, DISTT. JIND KH.
NO. 35//10, 11, 20, 36//15, 16

LEGEND

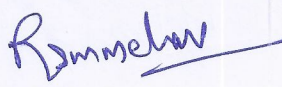
TOTAL AREA OF SCHEME = 3.47 ACRES
TOTAL NOS OF PLOTS = 93
AREA UNDER PLOTS = 1.92 ACRES(55.33%)
AREA UNDER MAHILA CHOUPAL = 0.05 ACRE.
AREA UNDER ROADS AND OPEN SPACE = 1.50 ACRES.

S. NO.	CATEGORY OF PLOTS	SIZE OF PLOTS(IN MTR.)	NO. OF PLOTS	TOTAL AREA (IN SQM.)
1.	100 SQ. YDS.	6.71 X 12.47	93	7781.65
2.	200 SQ. YDS. MAHILA CHAUPAL	15.74 X 12.47	1	196.28

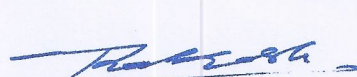
Drawing No. DTP (3) / 1521 / 2025 Date: 14.01.2025

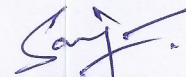


SCALE:- 1CM = 5M

DRAWN BY : 
RAMMEHAR. AD

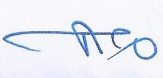
CHECKED BY : 
RAJESH KUMAR, JD

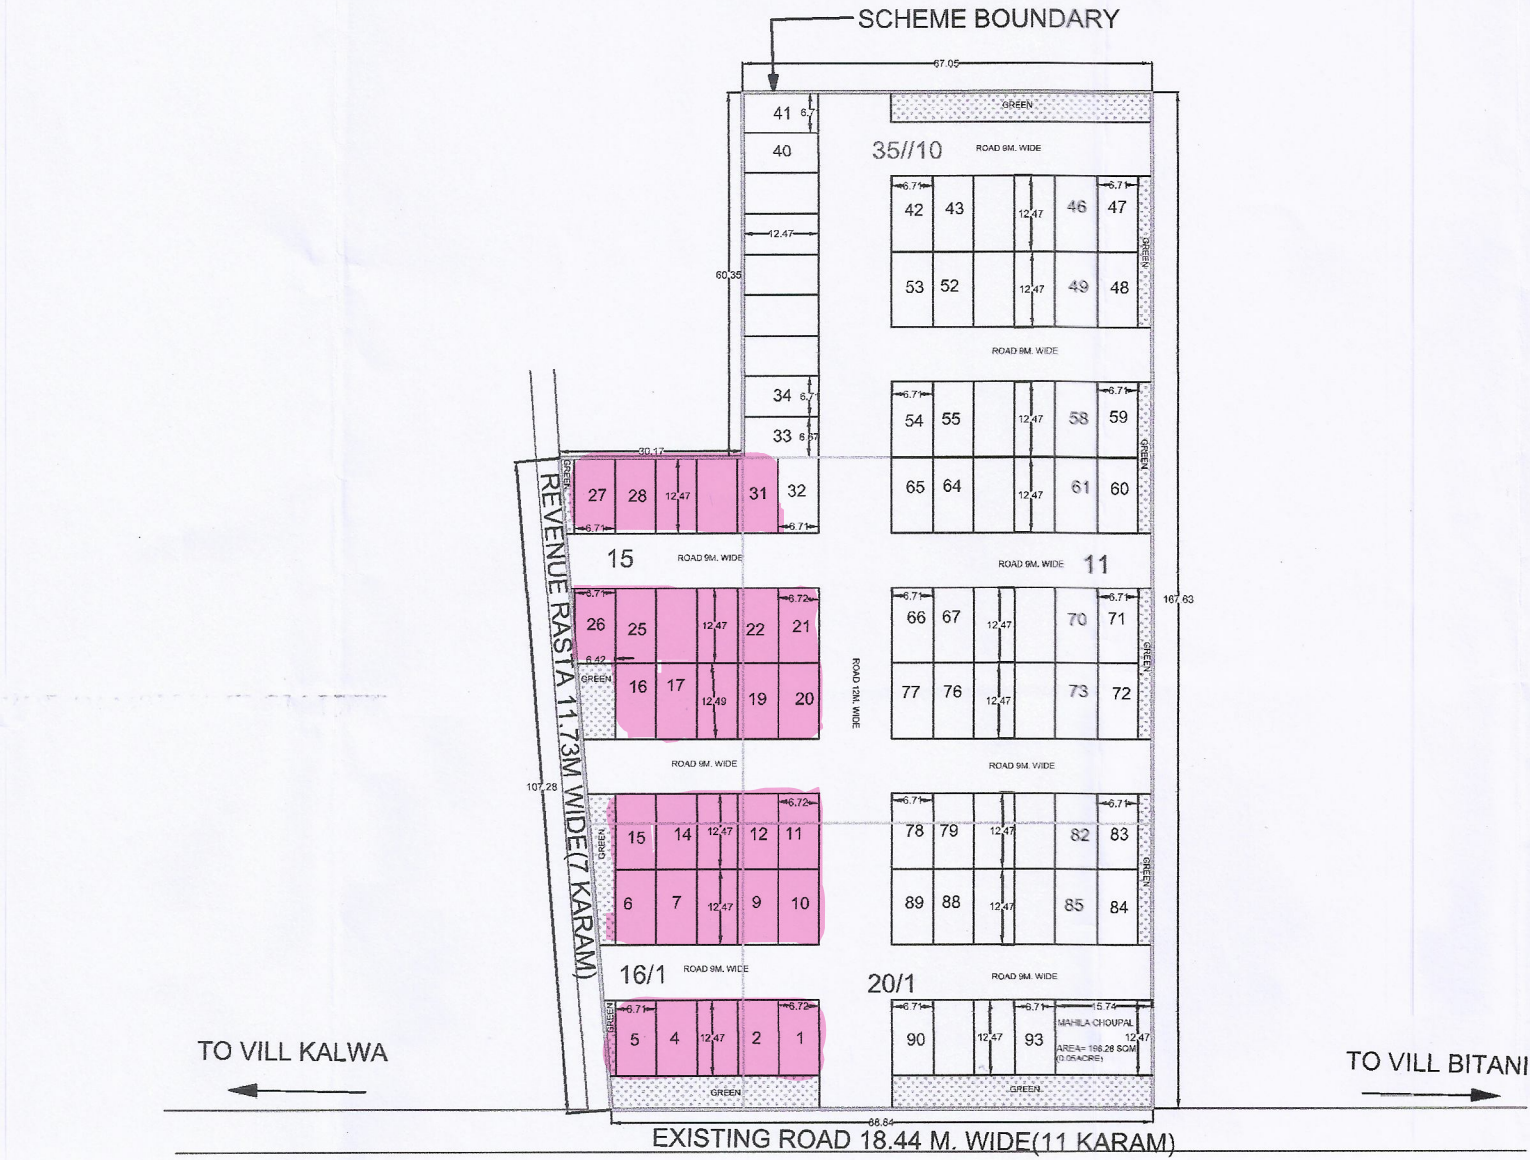
PLANNING ASSISTANT : 
RAKESH KUMAR,

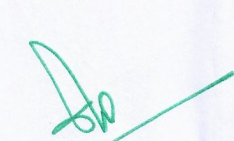
SURVEYED BY : 
JUNIOR ENGINEER

ASSISTANT TOWN PLANNER : (VACANT)

DISTRICT TOWN PLANNER, 

SENIOR TOWN PLANNER,
HISAR 



SUB DIVISIONAL OFFICER,
PANCHAYATI RAJ,
PILLU KHERA 

BLOCK DEVELOPMENT
& PANCHAYAT OFFICER,
PILLUKHERA 