

LAYOUT CUM DEMARCATION PLAN OF SITE APPROVED UNDER "MUKHYA MANTRI GRAMIN AWAS YOJNA - EXTENSION" (MMGAY-E), SITUATED AT KHASRA NO. 770,771,773, IN THE REVENUE ESTATE OF VILLAGE MANAS, TEHSIL AND DISTRICT KATHAL.



- LEGEND:-**
1. APPROVED "MMSAY" SCHEME BOUNDARY SHOWN THUS
 2. OPEN SPACE / PARK SHOWN THUS
 3. EXISTING ROAD SHOWN THUS
 4. KACHHIA/REVENUE RASTA SHOWN THUS
 5. H.T. LINE SHOWN THUS

DETAIL OF AREA	AREA IN ACRESS/ SQ. MT.
APPROVED "IMAGINE" SCHEME AREA	= 4.00 / 16187.40
NET PLANNED AREA	= 4.00 / 16187.40
AREA UNDER S.T.P.	= 0.04 / 165.92
AREA UNDER MANILA CHOUPL	= 0.027 / 109.26
AREA UNDER U.T.	= 0.027 / 109.26
AREA UNDER U.T.	= 0.023 / 93.07
AREA UNDER R.W.H. SPACE / PARK	= 0.03 / 121.40
AREA UNDER ROADS	= 1.516 / 6135.02

DETAIL OF NET PLANNED AREA = 100 ACRES				NO. OF PLOTS
SER. NO.	CATEGORY	SIZE		
1.	4 MARLA	9.71 M X 12.67 M		104
2.	4 MARLA	AS PER LAYOUT		01
3.	S.T.P.	AS PER LAYOUT		01
4.	U.T.	AS PER LAYOUT		01
5.	U.T.	AS PER LAYOUT		01
6.	E.T.	AS PER LAYOUT		01
TOTAL				109

PLOT AREA = 57.25 % (APP)

NOTES:-

1. ALL THE DIMENSIONS ARE IN METERS.
2. THE REVENUE MAP PLAN HAS BEEN PREPARED ON THE BASIS OF REVENUE SAJRA COLLECT FROM REVENUE DEPARTMENT OFFICE.
3. THE EXACT LOCATION, SHAPE AND SIZE OF EACH PLOTS ARE SUBJECT AT LOCAL DEMARCATION AT SITE.
4. THE SITE OF MUKHANYATI GRAMIN AYAS - EXTENTION (IMKAY-E) IN THE REVENUE ESTATE OF VILLAGE MANVAS, TESHIL AND DISTRICT KATHAL HAS BEEN PROVIDED BY DIRECTOR GENERAL DEVELOPMENT & PANCHAYATS DEPARTMENT - HARYANA, CHANDIGARH.

SCALE :- 1 CM. = 5 MTS.

DRAWING. NO. DTP (KTL) 295 / 2025

DATED:- 08.01.2025


DRAWN BY : - (RAJU, AD & RAJ KANWAR, AD)

JUNIOR DRAFTSMAN :- (VACANT)

PLANNING ASSISTANT. :- (VACANT)

ASSTT. TOWN PLANNER :- (VACANT)

DEPARTMENT. OF T & C PLANNING, HARYANA, CHANDIGARH.

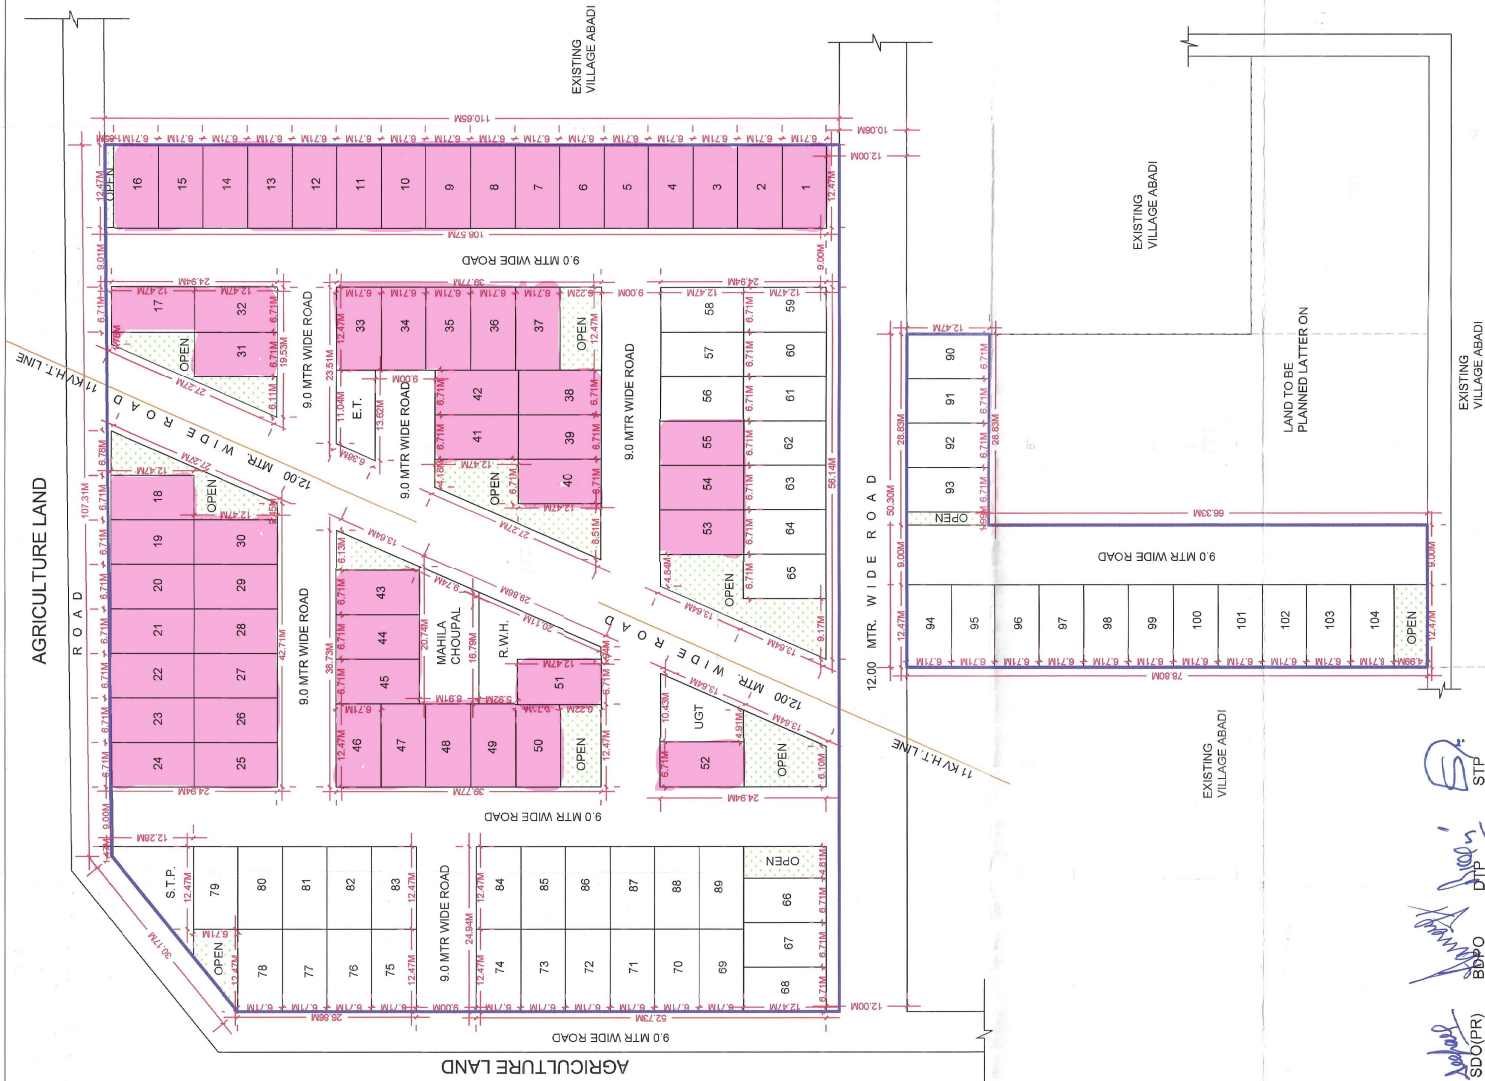

	SDO (PR)	(MEMBER)
	BDPO	(MEMBER)
	DTP	(MEMBER)
	STP	(CHAIRPERSON)