

KARNAL

PLAN OF HOUSING SCHEME UNDER
GROUP AMANTRI GRAMIN AWAS YOJANA-
EXTENSION (MMGAY-E) AREA MEASURING 4.00
ACRES, COMPRISING IN KHASRA NOS. 10// 8, 9, 12
& 13 IN THE REVENUE ESTATE OF VILLAGE CHAND
SARAI BLOCK-KUNJPURA, DISTRICT KARNAL.

DETAILS OF PLOTTED AREA

SR NO	PARTICULAR	SIZE	NOS	AREA
1	RES. PLOT	6.71X12.47 M	116	9706.15 SQM.
2	MAHILA CHOUPAL	10.63X15.80 M	1	167.95 SQM
TOTAL PLOTTED AREA				= 9874.10 SQM OR 2.44 ACRES

DETAILS OF AREA :-

AREA OF SCHEME
= 4.00 ACRES
PLOTTED AREA
= 2.44 ACRES (61%)
AREA UNDER PARK / OPEN SPACES
= 1.56 ACRES

LEGEND

SCHEME BOUNDARY	---
HT LINE	---
KULLA LINE	---
PARK / OPEN SPACES	---

NOTE: ALL DIMENSIONS ARE IN METERS ONLY.

THIS LAYOUT PLAN HAS BEEN PREPARED ON THE BASIS
OF SURVEY PLAN SUPPLIED BY DEPT OF HOUSING FOR
ALL (UPEA) AND RECEIVED THROUGH DIRECTORATE,
TOWN & COUNTRY PLANNING HARVANA VIDE THEIR
OFFICE E-MAIL DATED 02.01.2025.

SCALE: 1 CM = 5 MTR. NORTH

DR. NO. D.T.P (K) 1673/2024 DT. 06.12.2024 / 14.01.2025

DRAWN BY: RAJNEESH KUMAR (TRACER)

CHECKED BY: DHANIRAM RANGA (JD) PARDEEP KUMAR (JD)

ASSISTANT

RAMESH KUMAR (SD)

(VACANT)

TOWN PLANNER

MORHI SINGH

EXT. TOWN PLANNER


SATISH KUMAR

DEPT. OF TOWN & COUNTRY PLANNING HARVANA

SUB-DIVISIONAL OFFICER,
KUNJPURA BLOCK, DISTRICT KARNAL
PAU/CHAYATI R/O DEPARTMENT,
HARVANA CHANDIGARH

B.D.P.O. KUNJPURA BLOCK,
DISTRICT KARNAL

SENIOR TOWN PLANNER, PANCHKULA
TOWN & COUNTRY PLANNING DEPARTMENT
HARVANA CHANDIGARH

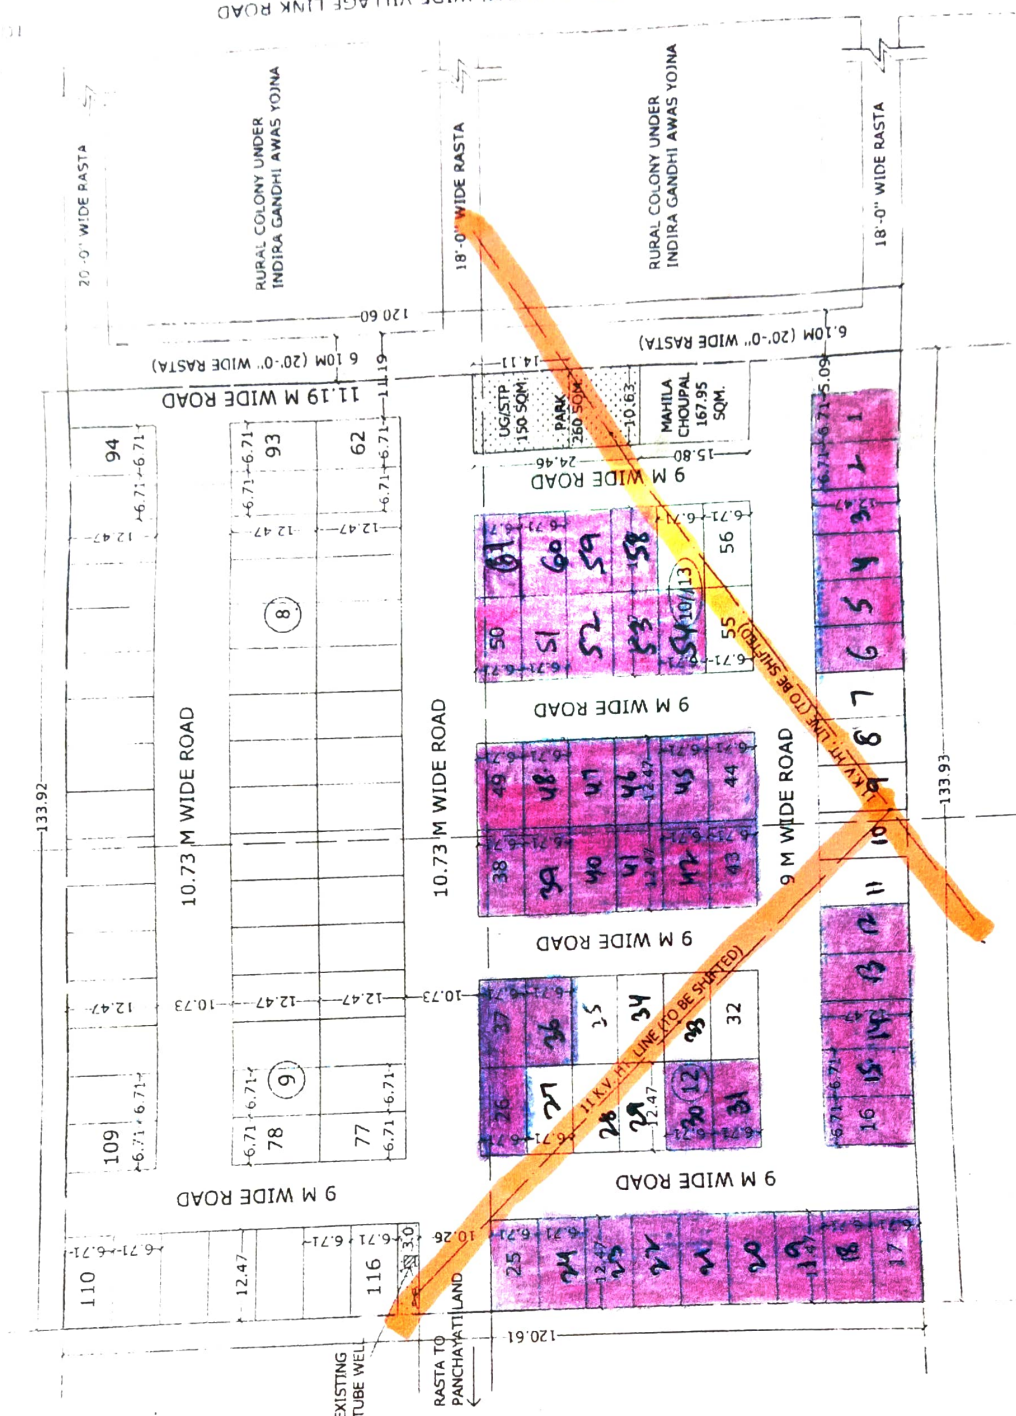

TO VILL CHANDSAMAND
13.41 MT (8-KARAM) WIDE VILLAGE LINK ROAD

32