

KARNAL

LAYOUT PLAN OF HOUSING SCHEME UNDER
"MUKHYAMANTRI GRAMIN AWAS YOLANA-
EXTENSION" (MMGAY-E) AREA MEASURING 5.70
ACRES, COMPRISING IN KHASRA NOS. 37/1/7, 8, 9, 12,
13 & 14 IN THE REVENUE ESTATE OF VILLAGE
HASSAMPUR, BLOCK-GHARAUNDA, DISTRICT KARNAL.

DETAILS OF PLOTTED AREA:-

SER. NO.	PARTICULAR	SIZE	NOS.	AREA
1.	RESIL. PLOT	6.71X12.47 M	140	11714.32 SQM.
2.	COMMUNITY CENTRE	56.41X35.88 M	1	2023.99 SQM.
3.	MAHILA CHOPAL	13.35X12.58 M	1	167.94 SQM.
4.	TUBE WELL	AS PER SITE	1	67.90 SQM.
TOTAL PLOTTED AREA				= 13974.15 SQM. OR 3.45 ACRES

DETAILS OF AREA:-

AREA OF SCHEME	= 5.70 ACRES
PLOTTED AREA	= 3.45 ACRES (60.52%)
AREA UNDER ROADS / PARK / OPEN SPACES	= 2.25 ACRES

LEGEND:-

SCHEME BOUNDARY	---
VILLAGE BOUNDARY	---
KULLA LINE	---
PARK / OPEN SPACES	---

NOTE:-
1. ALL DIMENSIONS ARE IN METERS.
2. THIS LAYOUT PLAN HAS BEEN PREPARED ON THE BASIS OF
AAS SAKRA PLAN OF PANCHAYATI LAND PROPOSED TO BE
DEVELOPED UNDER MMGAY-E SUPPLIED BY B.D.P.O.,
GHARAUNDA, DISTRICT KARNAL.

SCALE: 1 CM = 5 MTR.	NORTH
DRAWING NO. D.T.P (K) 1708 / 2025	DATED 21.01.2025

CHECKED BY: *[Signature]*
DHANIRAM PANDEY (J.D) PROJECT KARNAL (J.D)

PLANNING ASSISTANT (MOUNT)
RAMESH KUMAR (B.D)


ASSTT. TOWN PLANNER
MOHIT SINGH

DEPT. TOWN PLANNER
SATISH KUMAR

DEPT. OF TOWN & COUNTRY PLANNING HARYANA

6-KARAM (10.06 M) WIDE VILLAGE PHIRNI

PROPOSED 7-KARAM (11.73 M)
WIDE PANCHAYATI RASTA

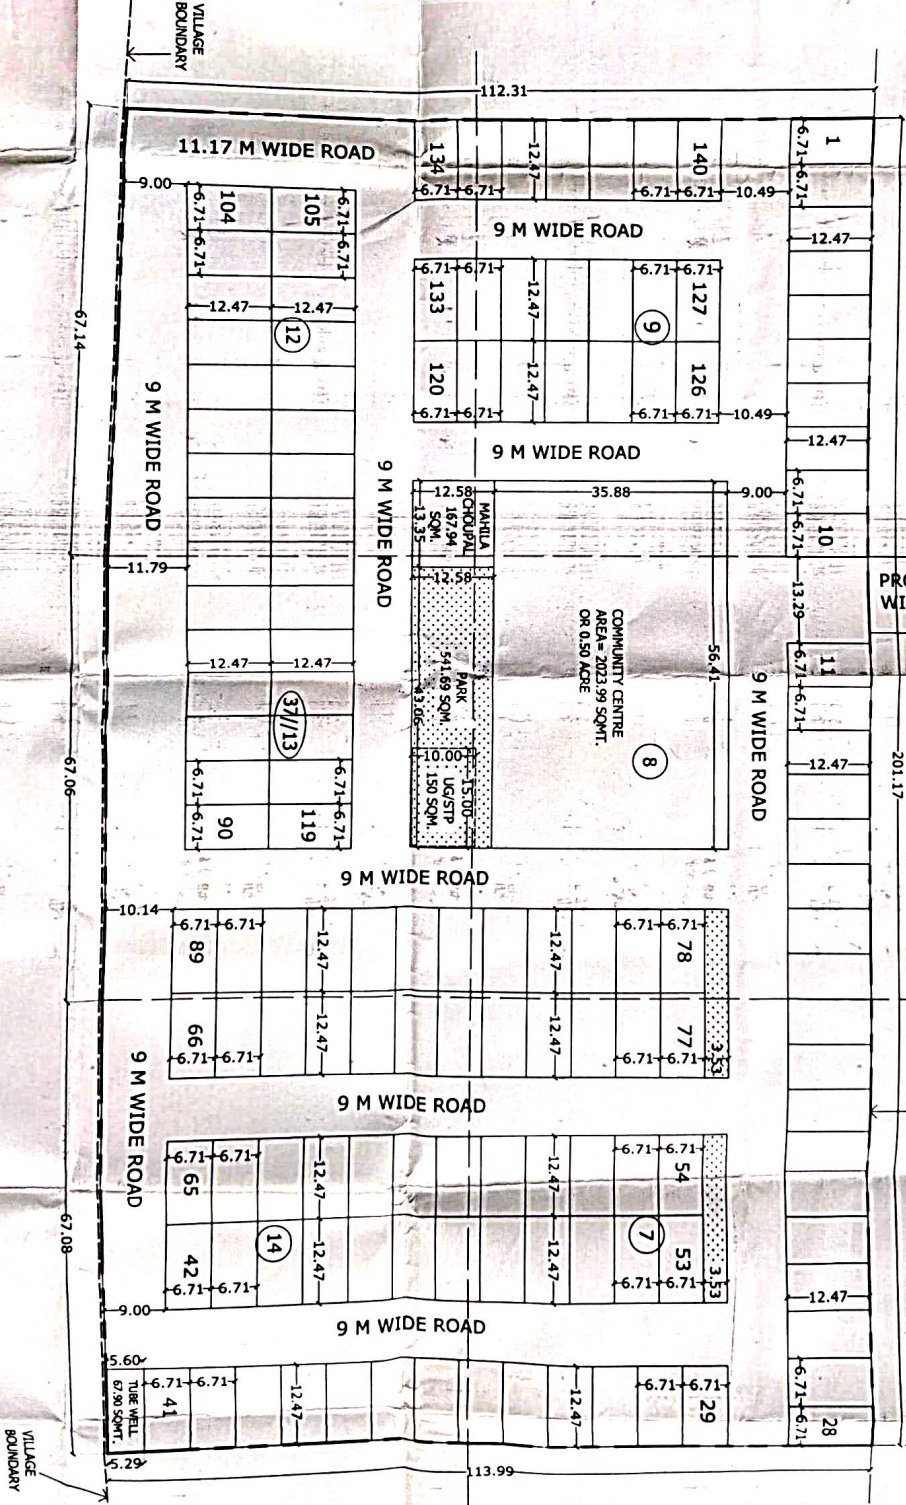

SUB DIVISION OFFICE,
GHARAUNDA BLOCK, DISTRICT KARNAL,
PANCHAYATI DEPARTMENT,
KARNAL, CHANDIGARH

B.D.P. GHARAUNDA BLOCK,
DISTRICT KARNAL

CHARTERPERSON MMGAY-E, CUM -
SENIOR TOWN PLANNER, PANCHKULA
TOWN & COUNTRY PLANNING DEPARTMENT,
HARYANA, CHANDIGARH