J H A J J A R

PART LAYOUT CUM DEMARCATION PLAN OF M.M.G.A.Y SITE IN KHASRA NO.- 86//11,12,87//14,15 REVENUE ESTATE TALAO, DISTRICT JHAJJAR.

LEGENED -

DETAIL OF AREA	AREA IN ACRES
TOTAL SITE AREA	4 051 ACRE
AREA UNDER PLOTS	1 985 "
AREA UNDER MAHILA CHOUPAL	0 049 "
AREA UNDER MARKET	0 049 "
AREA UNDER STP SITE	0 040 "
AREA UNDER ROADS & PARKS	1 928 "

CATEGORY	SIZE OF PLOTS	AREA OF PLOTS	TOTAL PLOT	TOTAL AREA
100 SQY	13 12MX8 38M	83 70 SQM	96 NOS	8035 2 SQM
				1 985 ACRS

SCHEME BOUNDARY SHOWN THUS

NOTE - 1. THIS DRAWING HAS BEEN PREPARED OF BASIS OF SURVEY PLAN RECEIVED FROM BLOCK DEVELOPMENT PANCHYAT OFFICE JHAJJAR MEMO NO 3484 DATED 13 01 2025

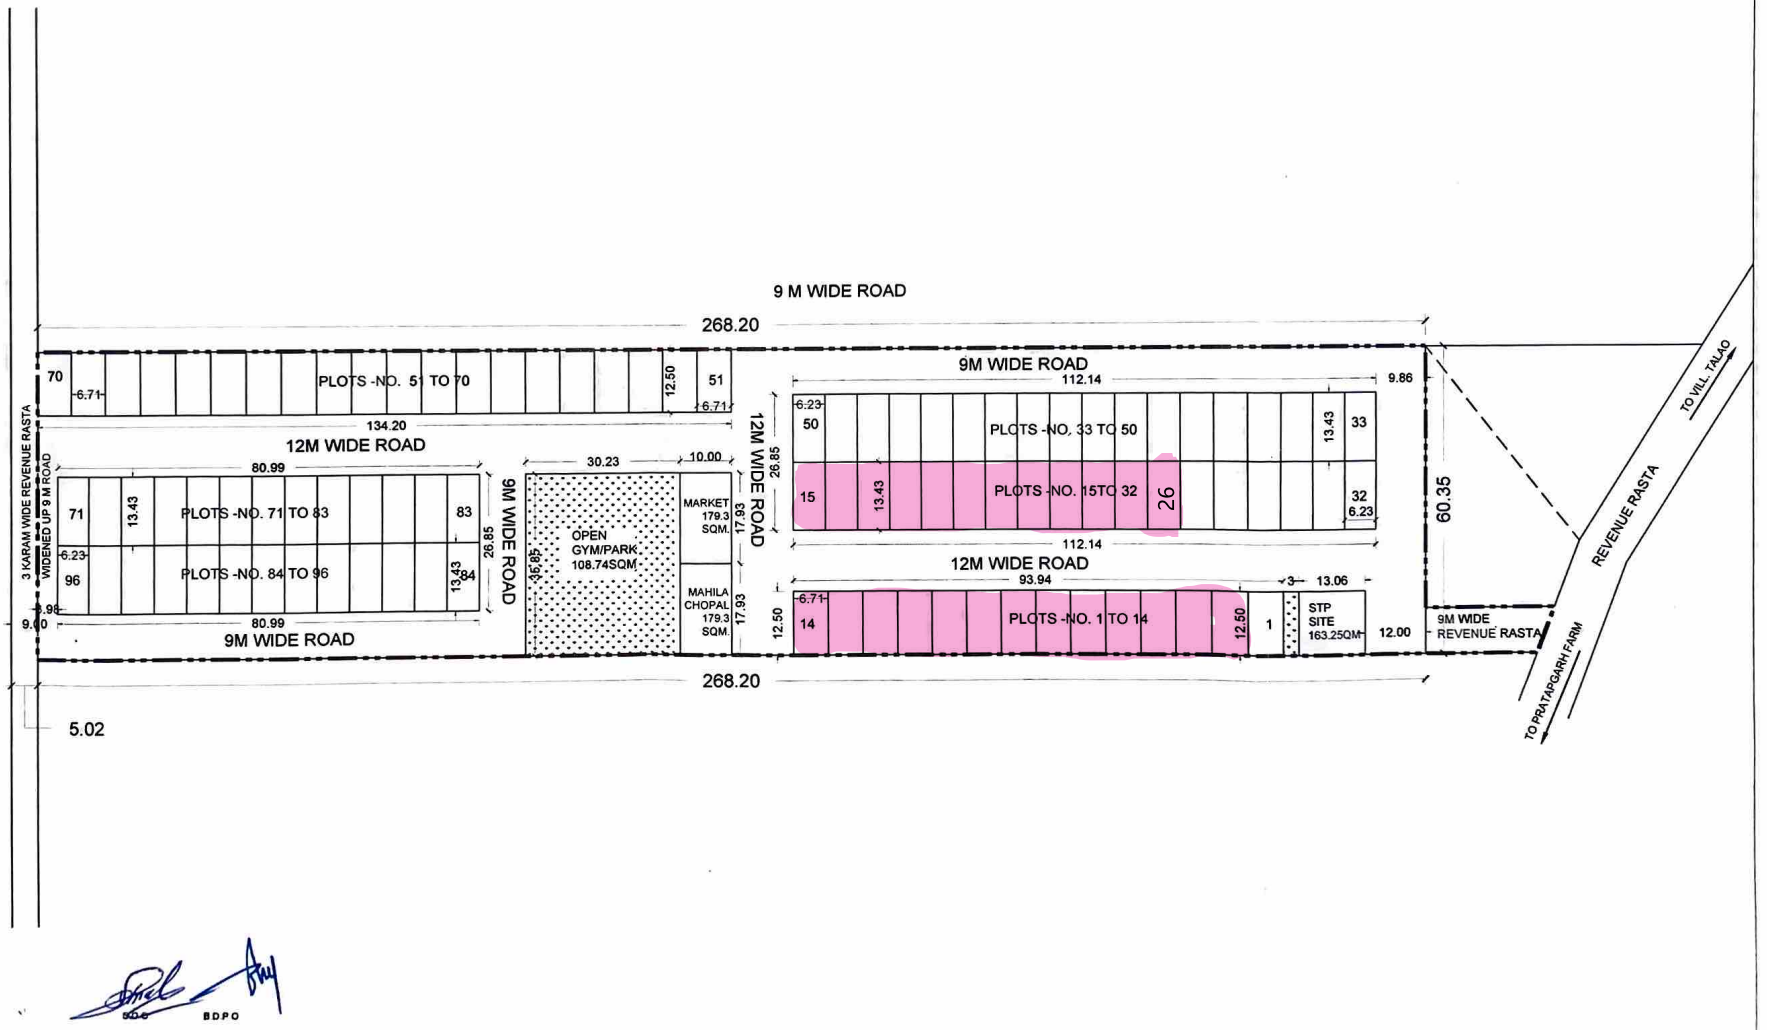

SCALE -NTS

DRAWING NO.- DTP (JH)738/2025, DT. 15.01.2025

DRAWN BY	(NARENDER AG)
CHECKED BY	(SANDEEP KUMAR JE) JE
Sr. DRAUGHTSMAN	(SUKESH SO)
ASSTT TOWN PLANNER	(SATISH KUMAR)
DISTT TOWN PLANNER	(MANISH CHHOKAR)
SENIOR TOWN PLANNER ROHTAK	(GAGANDEEP SINGH)

SDO BDPO

DEPTT. OF T & C. PLANNING HARYANA