


SECTOR - 8 DADRI

AREA = 6.49 ACRES, PLOTS = 425, 1 MARLA PLOT = 30 SQ YDS

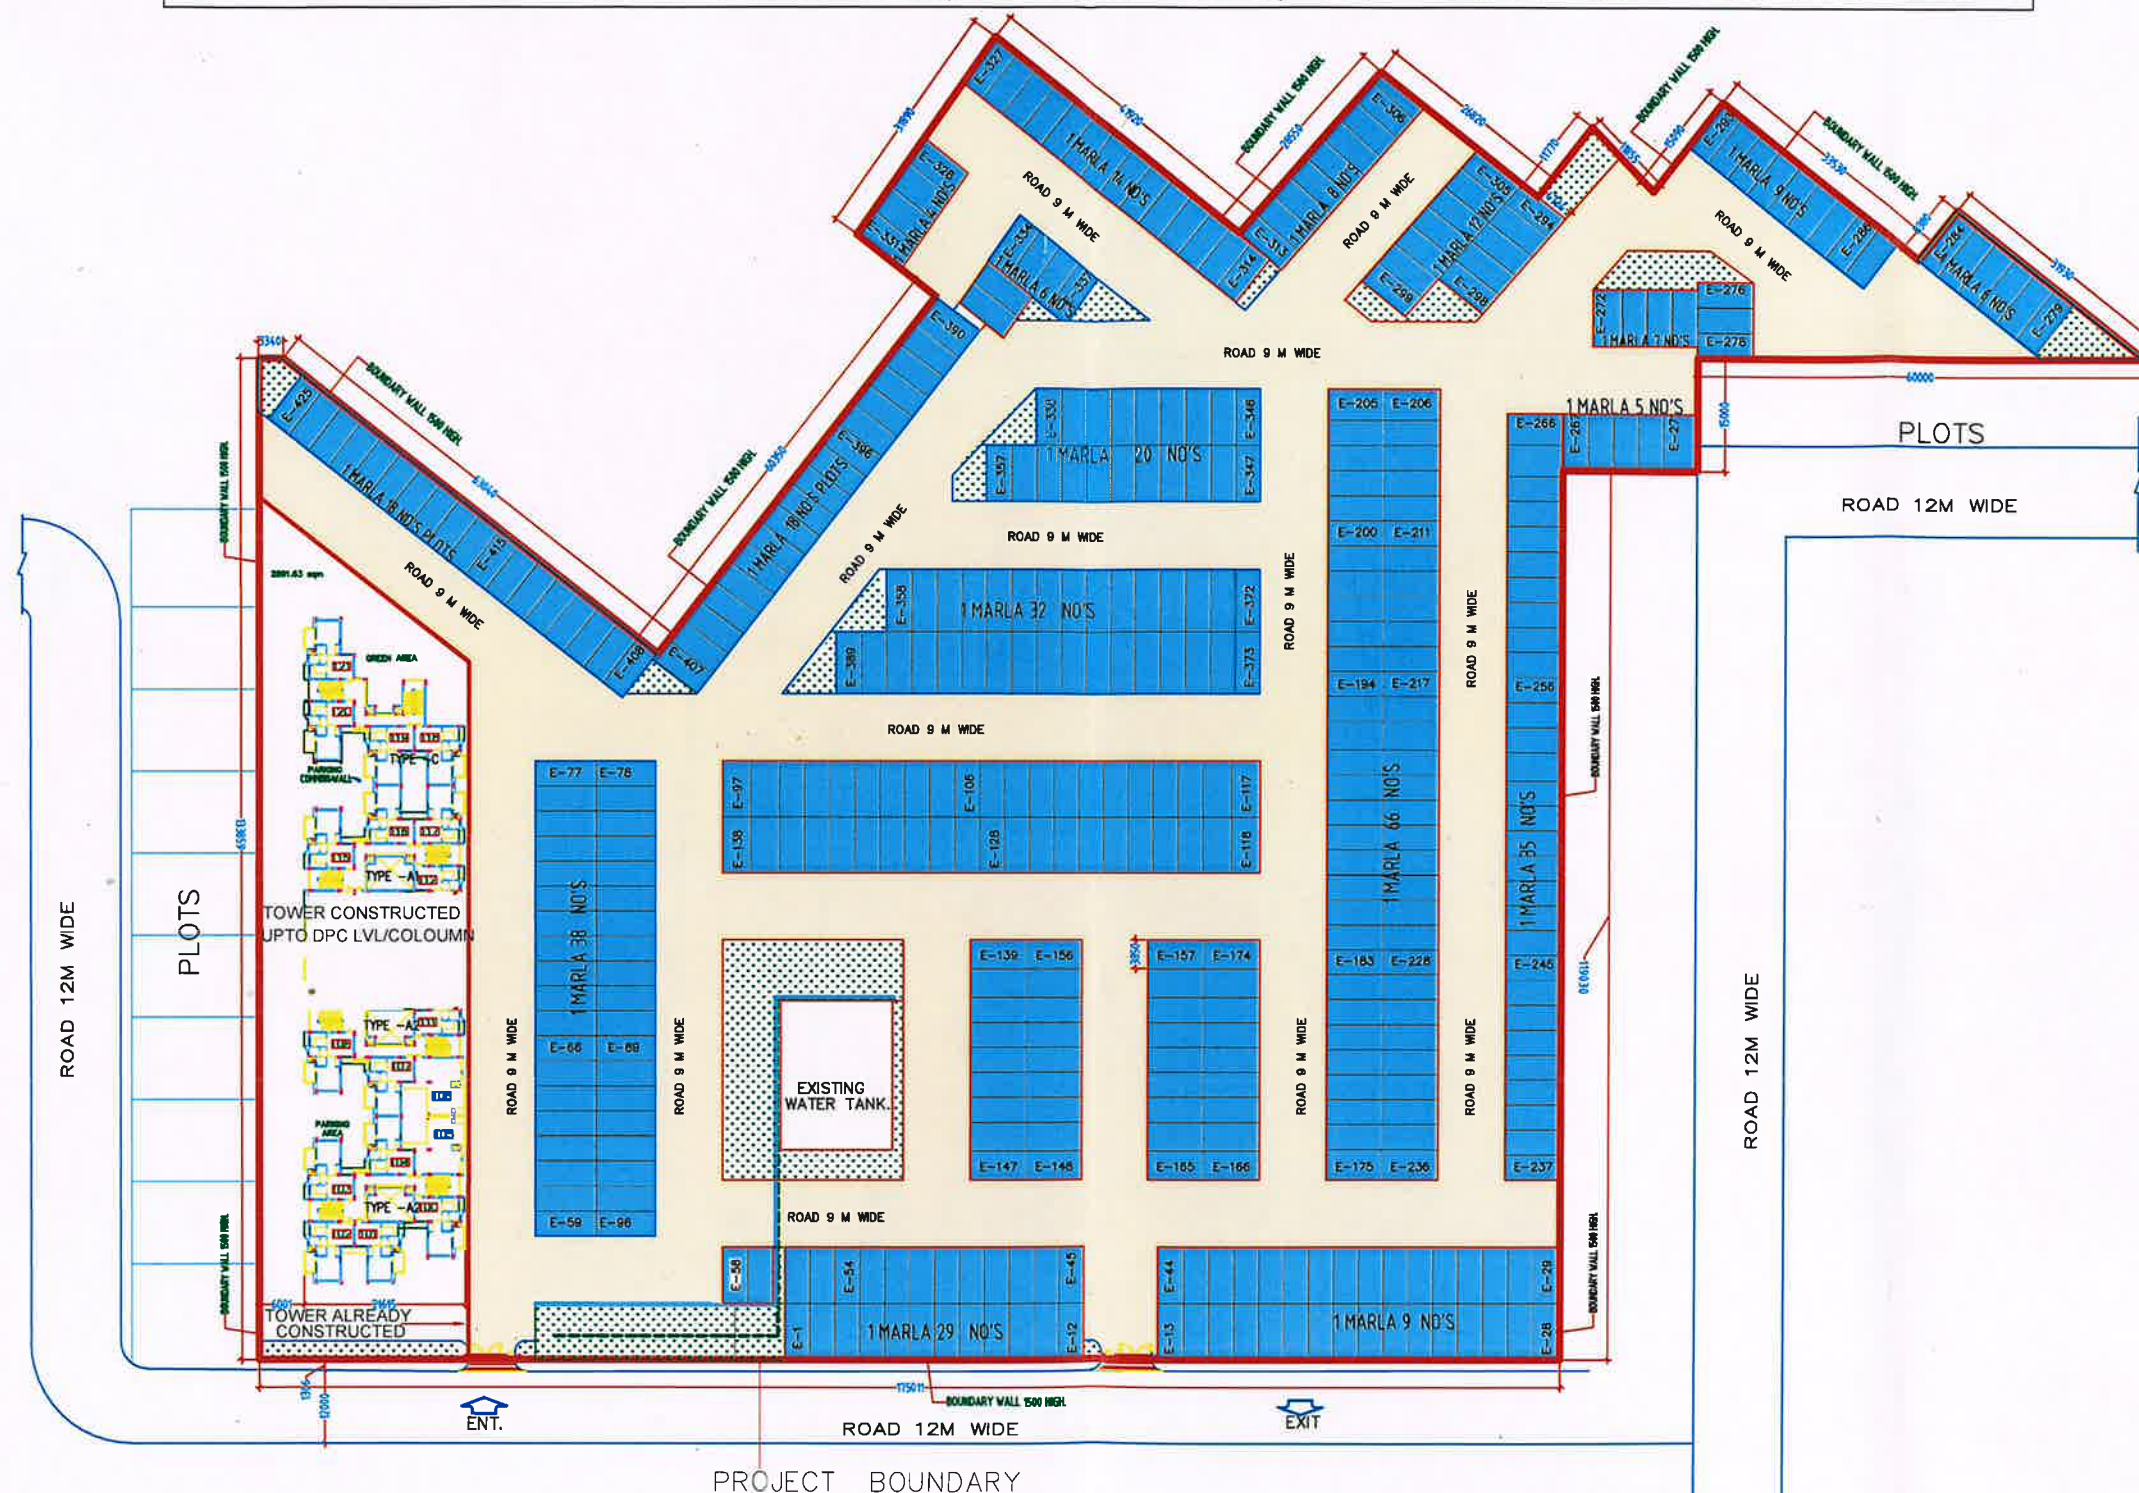


AREA DETAIL

TOTAL SITE AREA = 26287.423 SQM (6.49 ACRES)
 AREA UNDER GROUP HOUSING = 2891.63 SQM (0.71 ACRES)
 TOTAL BALANCE AREA = 23395.80 SQM (5.78 ACRES)
 PERMISSIBLE 60% AREA = 14037.475 SQM
 ACHIEVED PLOTTABLE AREA = 11633.11 SQM (49.72%)
 ACHIEVED GREEN AREA = 1179.11 SQM 0.35 ACRES (4.485%)

DETAIL OF PLOTS

PLOT SIZE = 3.350MX7.50M
 CATEGORY = 1 MARLA
 TOTAL NO'S PLOTS = 425 NO'S

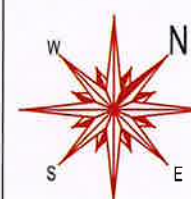

Drawing title : SITE PLAN

CHIEF ADMINISTRATOR -sd-
 SECRETARY
 CHIEF ENGINEER
 SENIOR TOWN PLANNER
 ARCHITECT
 ASSISTANT TOWN PLANNER

HBH

PROPOSAL FOR TENTATIVE
 LAYOUT PLAN FOR 1 MARLA
 PLOTS UNDER MUKHYAMANTRI
 AWAS YOJANA SECTOR-8,
 DADRI.

DEALT BY
 Job no. DATE drg no.

scale