
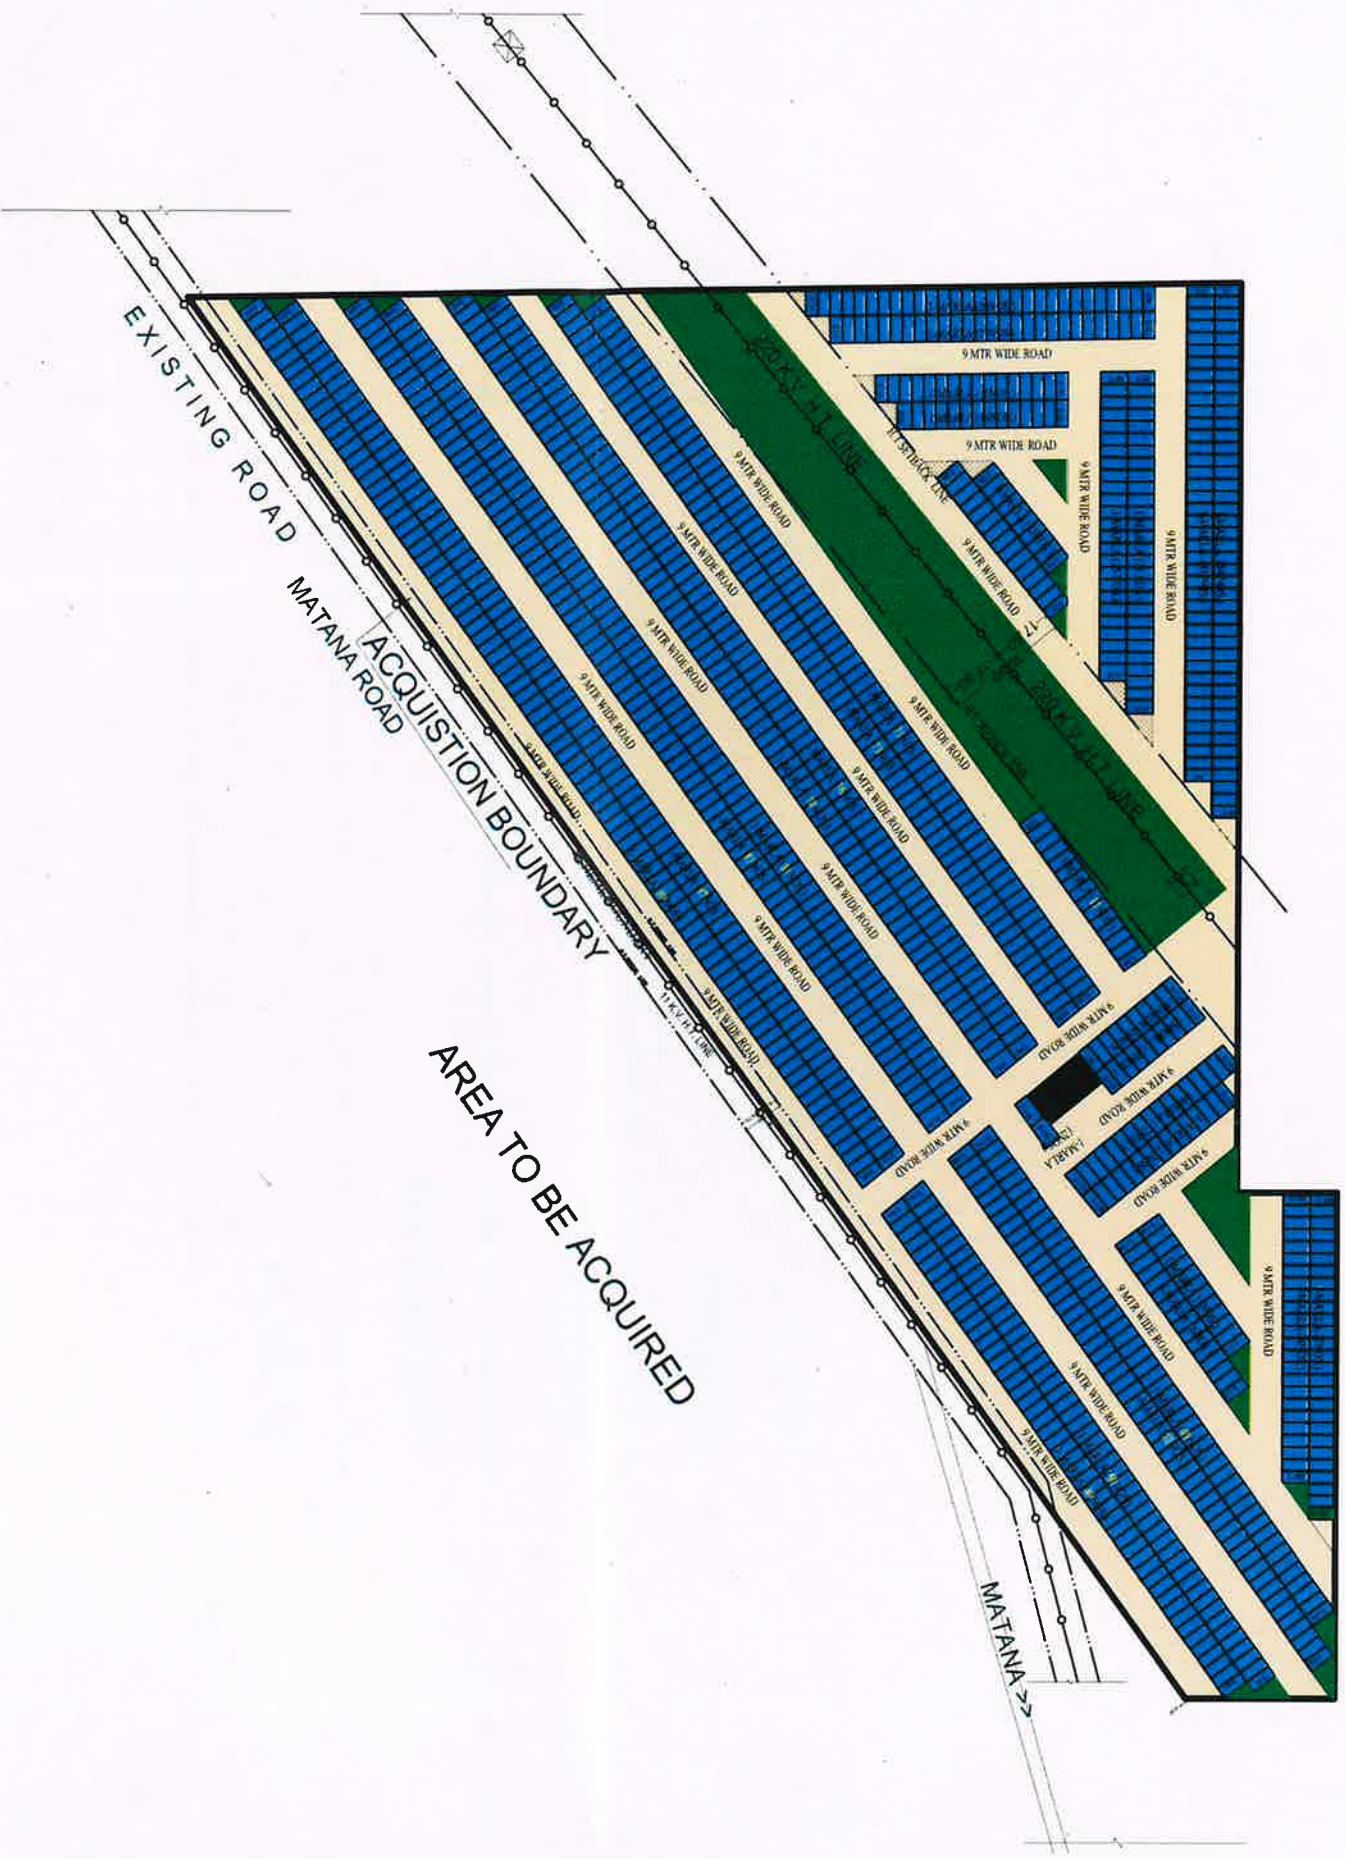


Fatehbad , SECTOR-9, Part -1 & 2

AREA=15.795ACRES, PLOTS=1236NOS., 1MARLA =30SQ.YDS.

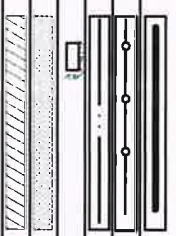

AREA DETAIL TOTAL AREA OF SCHEME = 63906.57 SQ.M. OR 15.795 ACRES AREA UNDER H.T LINE/ENCROCHMENT = 8362.77+202.10= 8564.87 OR 2.11 acres AREA AVAILABLE FOR PLOTTED SCHEME= 55341.7 SQ.M. OR 13.68 ACRES AREA ACHIEVED UNDER PLOTTED SCHEME TOTAL NO OF PLOTS = 1236 PLOTS (PLOT SIZE:-3.35mx7.50m = 25.125 SQ.M) TOTAL AREA ACHIEVED@1236PLOTS =31157.93 Sqm@59.24% GREEN AREA = 6058.62SQ.M @9.48% (INCLUDING AREA UNDER H.T LINE)		CHIEF ADMINISTRATOR - <i>sd-</i> SECRETARY* <i>gh.</i> CHIEF ENGINEER <i>g</i> SENIOR TOWN PLANNER <i>Sh</i> ARCHITECT <i>gk</i> ASSISTANT TOWN PLANNER <i>R.</i>	HBH PROPOSAL FOR TENTATIVE LAYOUT PLAN FOR 1-MARLA PLOTS UNDER MUKHYAMANTRI AWAS YOJANA SECTOR- Fatehbad Sector-9 Part -1 & 2
1. SCHEME BOUNDARY 2. 220 K.V. H.T. LINE 3. H.T SETBACK LINE 4. PROPOSED 1-MARLA PLAN 5. PROPOSED GREEN AREA 6. ENCROCHED AREA		DEALT BY	Job no. date : dng.no.