

KARNAL

LAYOUT PLAN OF HOUSING SCHEME UNDER "MUKHYAMANTRI GRAMIN AWAS YOJANA - 2.0" (MMGAY-2.0) AREA MEASURING 9.15 ACRES, COMPRISING IN KHASRA NOS. 14//18, 19, 20, 22, 23, 23//2, 3, 67//4, 5, 6, 7, & 16 IN THE REVENUE ESTATE OF VILLAGE BARSALU, BLOCK-NILOKHERI, DISTRICT KARNAL.

DETAILS OF PLOTTED AREA :-

SR.NO.	PARTICULAR	SIZE	NOS.	AREA
1.	RESI. PLOT	6.71x12.47 M	200	16734.74 SQM.
2.	MAHILA CHOUPAL	AS PER SITE	1	200.00 SQM.
3.	TUBE WELL	AS PER SITE	2	217.67 SQM.
TOTAL PLOTTED AREA		= 17152.41 SQM. OR 4.24 ACRES		

DETAILS OF AREA :-

AREA OF SCHEME PLOTTED AREA	= 9.15 ACRES
AREA UNDER ROADS / PARKS / OPEN SPACES	= 4.24 ACRES (46.33%)
	= 4.91 ACRES

LEGEND :-

SCHEME BOUNDARY	
HT. LINE	
KILLA LINE	
VILLAGE BOUNDARY	
PARK / OPEN SPACES	

- NOTE:-
1. ALL DIMENSIONS ARE IN METERS.
 2. THIS LAYOUT PLAN HAS BEEN PREPARED ON THE BASIS OF SAJARA PLAN PROVIDED BY BDPO, NLOKHERI AND SITE PLAN PROVIDED BY GRAM PANCHAYAT BARSALU.
 3. THE KHARSA NOS. OF MMGAY-2.0 SCHEME FALLS OUTSIDE CONTROLLED AREA AND URBAN AREA OF DISTRICT KARNAL.
 4. THIS SITE DOES NOT FALL IN NCZ SURVEY REPORT APPROVED BY DLSC AND SENT TO SLC.

SCALE: 1 CM = 6 MTR. NORTH

DRAWING NO. D.T.P (K) 1752 / 2025 DATED 13.08.2025

DRAWN BY:- RAJNEESH KUMAR (TRACER)


CHECKED BY:- DHANI RAM RANGA (JD) PARDEEH KUMAR (SD)

PLANNING ASSISTANT (VACANT) RAMESH KUMAR (SD) ANKUR, F.I.

ASSTT. TOWN PLANNER MOHIT SINGH

DISTT. TOWN PLANNER GUNJAN VERMA

DEPTT. OF TOWN & COUNTRY PLANNING HARYANA

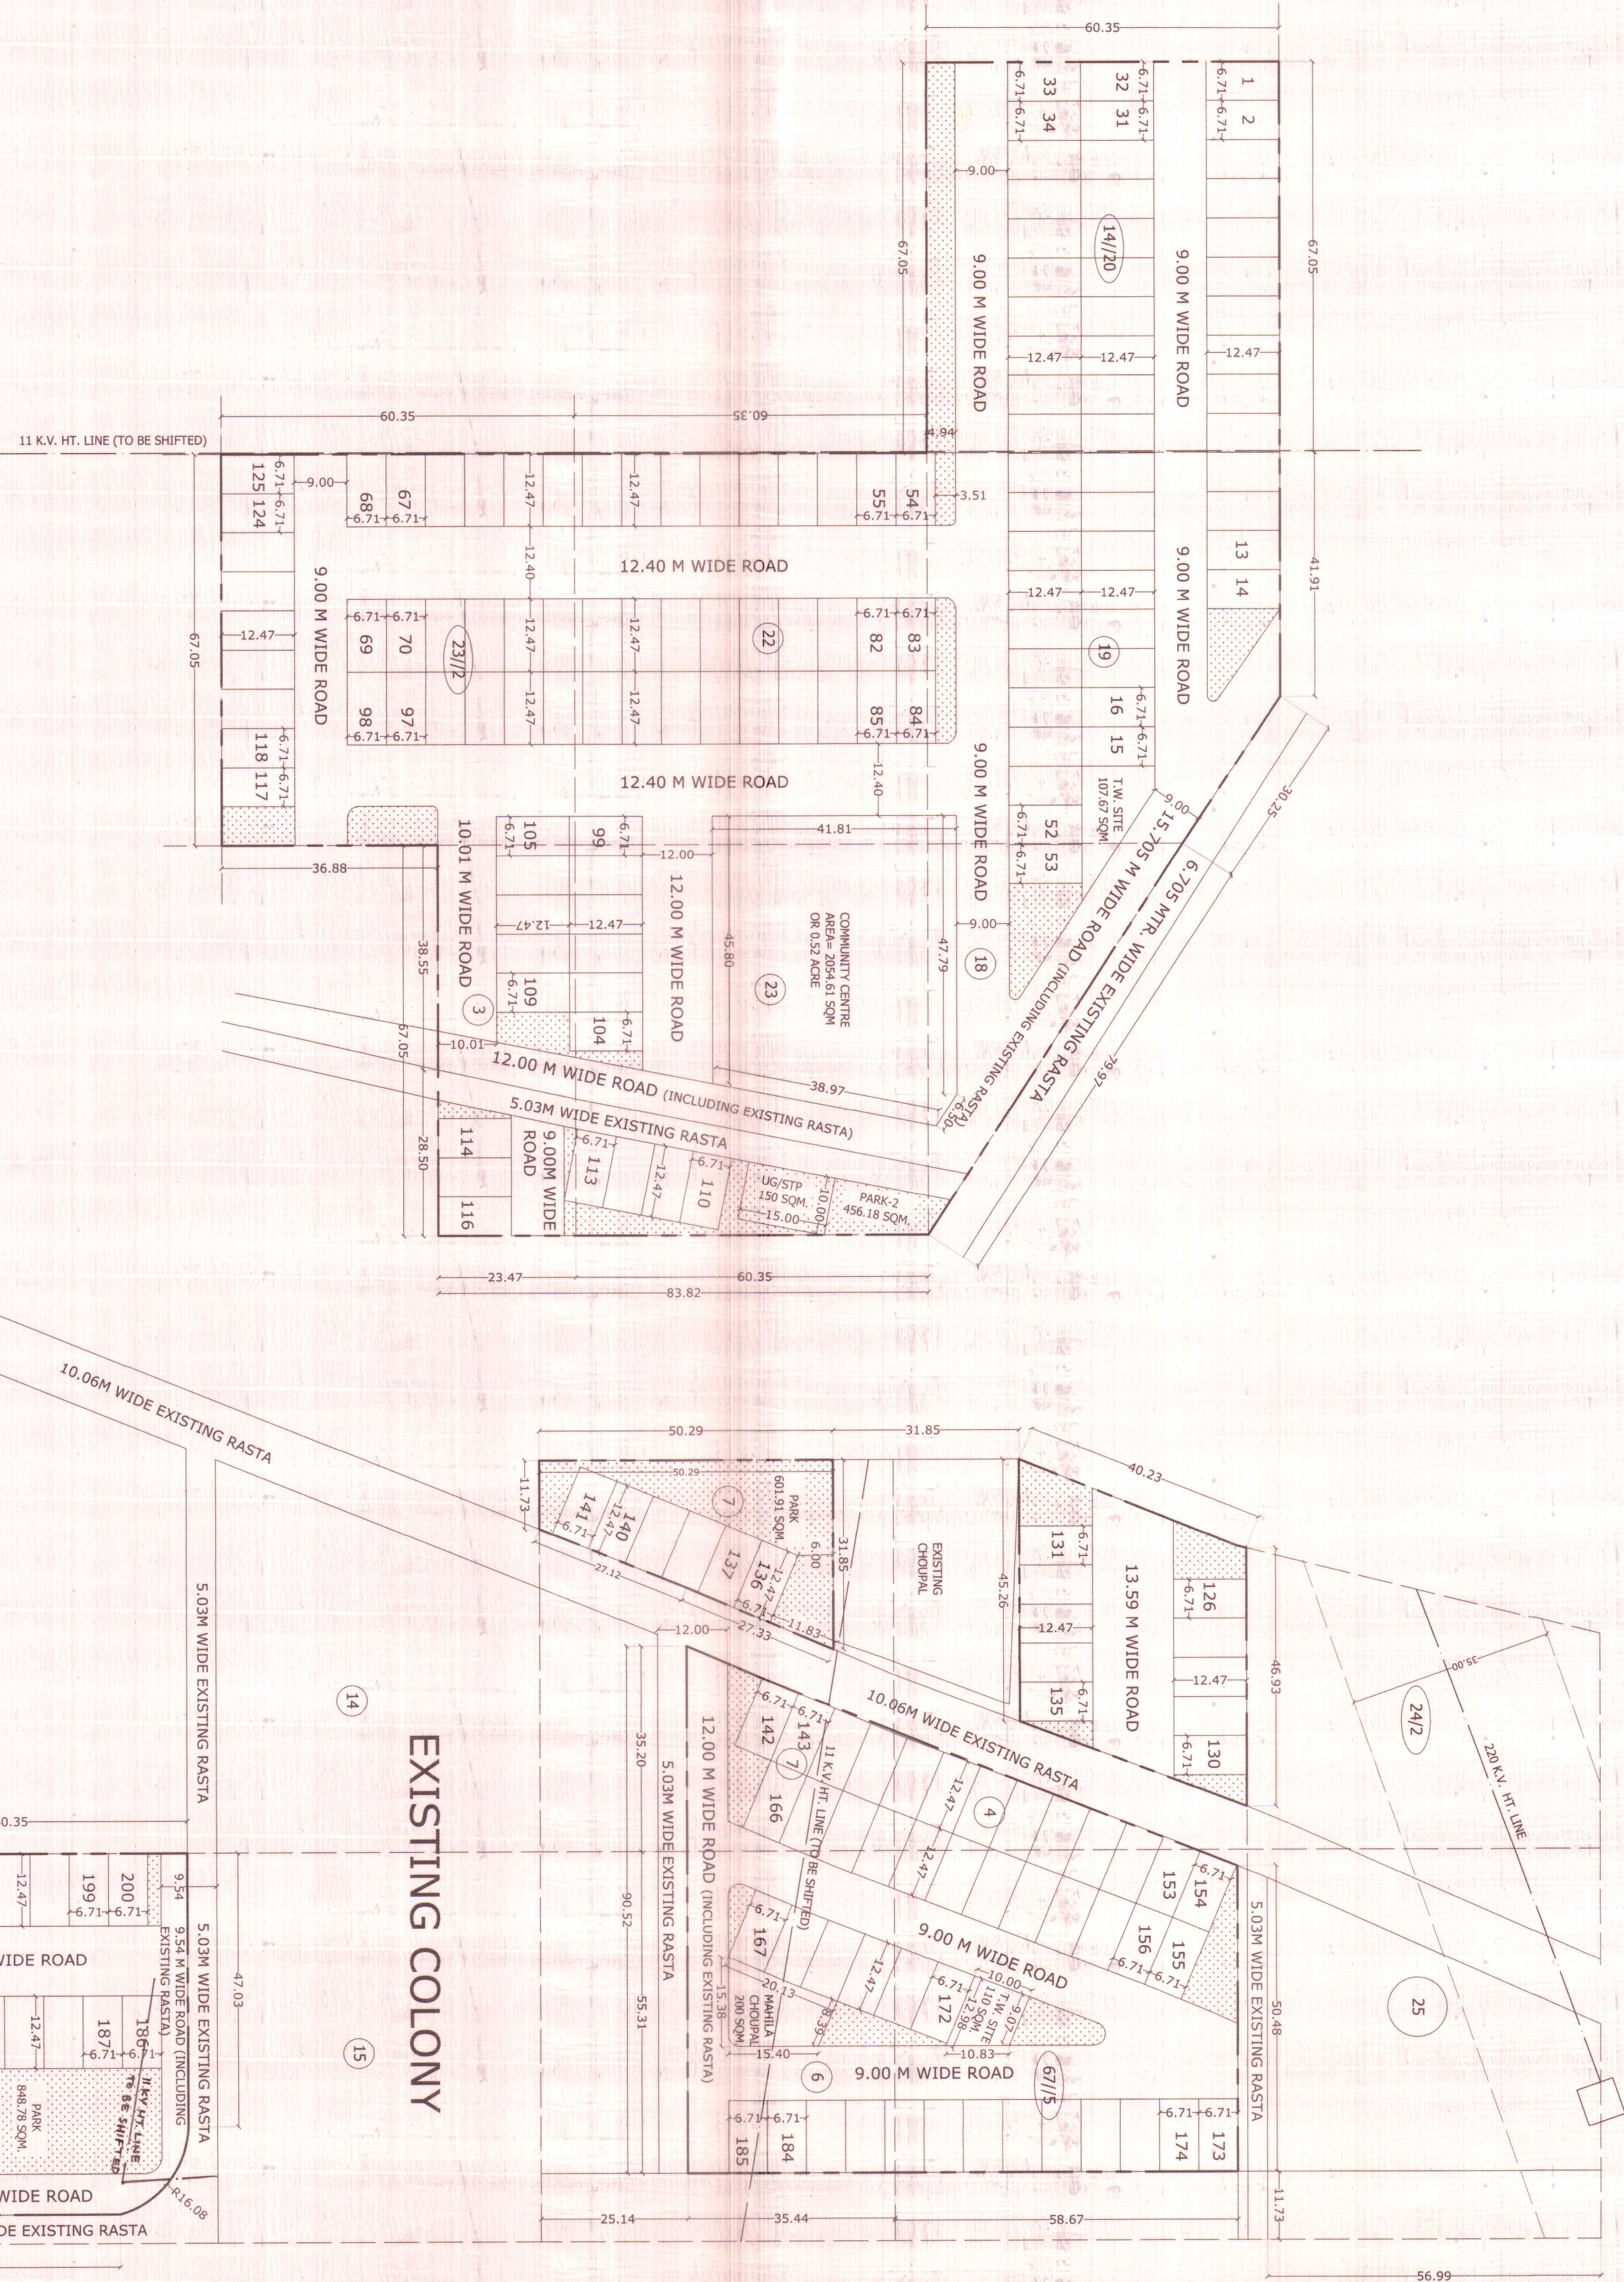

SUB DIVISIONAL OFFICER, NLOKHERI BLOCK, DISTRICT KARNAL PANCHAYAT RAJ DEPARTMENT, HARYANA, CHANDIGARH

B.D.P.O., NLOKHERI BLOCK, DISTRICT KARNAL

CHAIRPERSON "MMGAY-2.0" - CUM - SENIOR TOWN PLANNER PANCHKULA TOWN & COUNTRY PLANNING DEPARTMENT, HARYANA, CHANDIGARH