K A R N A L

LAYOUT PLAN OF HOUSING SCHEME UNDER "MUKHYAMANTRI GRAMIN AWAS YOJANA - 2.0" (MMGAY-2.0) AREA MEASURING 9.40 ACRES, COMPRISING IN KHASRA NOs. 65//18, 23, 68//4, 5, 6, 69//1, 2, 3, 8, 9, 10, 11, & 12 IN THE REVENUE ESTATE OF VILLAGE BHADSON, BLOCK-INDRI, DISTRICT KARNAL.

DETAILS OF PLOTTED AREA :-

SR.NO.	PARTICULAR	SIZE	NOS.	AREA
1.	RESI. PLOT	6.71X12.47 M	254	21253.12 SQM.
2.	COMMUNITY CENTRE	AS PER SITE	1	2348.66 SQM.
3.	MAHILA CHOUPAL	11.64X14.37 M	1	167.27 SQM.
4.	TUBE WELL	AS PER SITE	1	101.07SQM.
TOTAL PLOTTED AREA		= 23870.12 SQM. OR 5.898 ACRES		

DETAILS OF AREA :-

AREA OF SCHEME	= 9.40 ACRES
PLOTTED AREA	= 5.898 ACRES (62.74%)
AREA UNDER ROADS / PARKS / OPEN SPACES	= 3.502 ACRES

LEGEND :-

- SCHEME BOUNDARY
- HT. LINE
- KILLA LINE
- VILLAGE BOUNDARY
- PARK / OPEN SPACES

NOTE:-

1. ALL DIMENSIONS ARE IN METERS.
2. THIS LAYOUT PLAN HAS BEEN PREPARED ON THE BASIS OF SAJRA PLAN PROVIDED BY BDPO, INDRI.
3. THE KHASRA NOs. OF MMGAY-2.0 SCHEME FALLS OUTSIDE CONTROLLED AREA AND URBAN AREA OF DISTRICT KARNAL.
4. THIS SITE DOES NOT FALL IN NCZ SURVEY REPORT APPROVED BY DLSC AND SENT TO SLC.

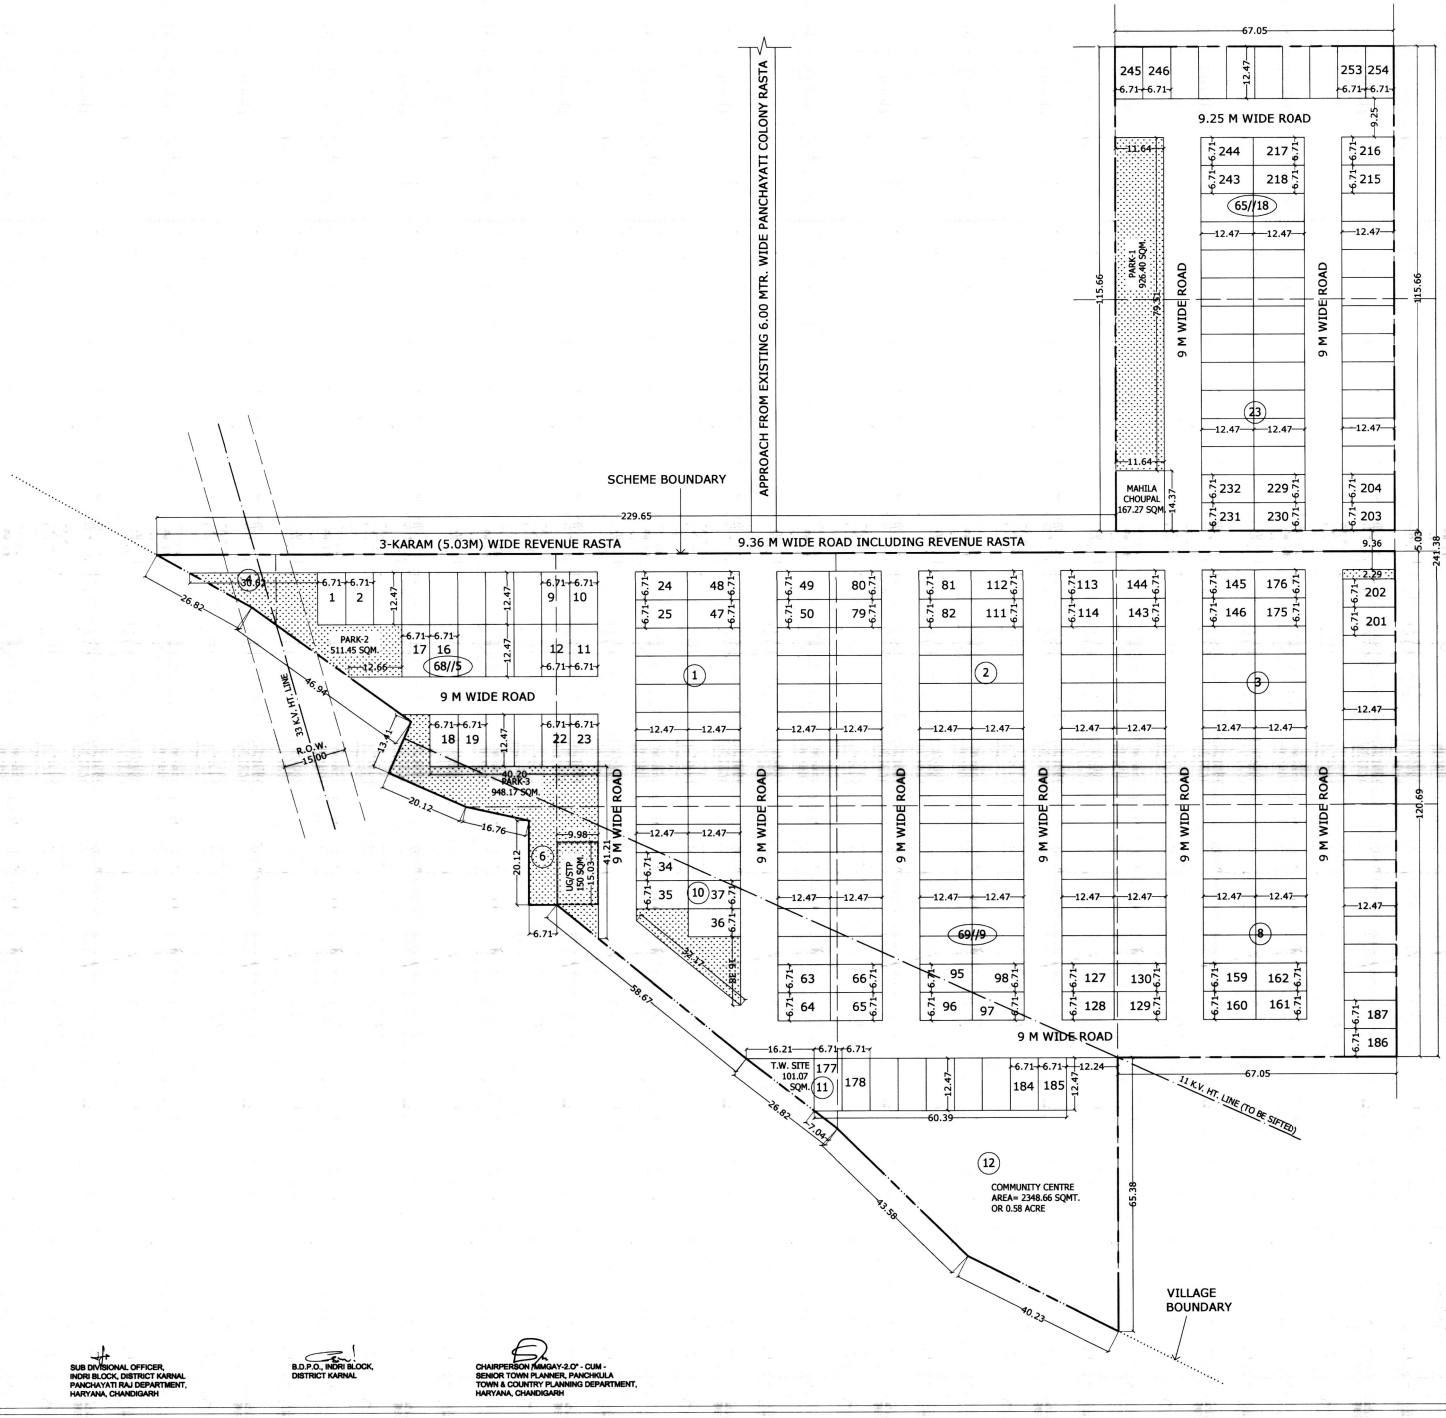

SCALE: 1 CM = 5 MTR. | NORTH

DRAWING NO. D.T.P. (K) 1749/2025 DATED:- 25.07.2025

DRAWN BY:-	DHANI RAM RANGA (JD)	
CHECKED BY:-	PARDEEP KUMAR (SD), RAMESH KUMAR (SD)	
PLANNING ASSISTANT	(VACANT)	MOHIT, J.E.
ASSTT. TOWN PLANNER	MOHIT SINGH	JOGINDER SINGH, PATWARI
DISTT. TOWN PLANNER	GUNJAN VERMA	

DEPTT.OF TOWN & COUNTRY PLANNING HARYANA

SUB DIVISIONAL OFFICER, INDRI BLOCK, DISTRICT KARNAL PANCHAYATI RAJ DEPARTMENT, HARYANA, CHANDIGARH

B.D.P.O., INDRI BLOCK, DISTRICT KARNAL

CHAIRPERSON MMGAY-2.0" - CUM - SENIOR TOWN PLANNER, PANCHKULA TOWN & COUNTRY PLANNING DEPARTMENT, HARYANA, CHANDIGARH