

KARNAL

LAYOUT PLAN OF HOUSING SCHEME UNDER "MUKHYAMANTRI GRAMIN AMAS YOLANA - 2.0" (MMGAY-2.0) AREA MEASURING 6.30 ACRES, COMPRISING IN KHASRA NOS. 50//10, 11, 20, 21, 51//3, 4, 5, 6, 7, 15, 16 MIN & 25 MIN IN THE REVENUE ESTATE OF VILLAGE DACHAR, BLOCK-MISSING, DISTRICT KARNAL.

DETAILS OF PLOTTED AREA :-

S.R.NO.	PARTICULAR	SIZE	NOS.	AREA
1.	RESID. PLOT	6.71X12.47 M	125	10459.21 SQM.
2.	COMMUNITY CENTRE	AS PER SITE	1	205.89 SQM.
3.	MAHILA CHOUPAL	13.42X12.47 M	1	167.34 SQM.
4.	TUBE WELL	AS PER SITE	1	142.89 SQM.
TOTAL PLOTTED AREA				= 12795.08 SQM. OR 3.162 ACRES


DETAILS OF AREA :-
AREA OF SCHEME = 6.30 ACRES
PLOTTED AREA = 3.162 ACRES (50.19%)
AREA UNDER ROADS / PARKS / OPEN SPACES = 3.138 ACRES

LEGEND :-

SCHEME BOUNDARY	---
HT. LINE	----
KULLA LINE	----
VILLAGE BOUNDARY	----
PARK / OPEN SPACES	----

NOTE:-
1. ALL DIMENSIONS ARE IN METERS.
2. THIS LAYOUT PLAN HAS BEEN PREPARED ON THE BASIS OF
3. SLABA PLAN PROVIDED BY BDO, MISSING.
3. URBAN AREA MISSING.
4. THE KHASRA NOS. OF MMGAY-2.0 SCHEME FALLS OUTSIDE
CONTROLLED AREA OF DISTRICT KARNAL.
5. THIS SITE DOES NOT FALL IN MCZ SURVEY REPORT
APPROVED BY DLSC AND SENT TO S.L.C.

SCALE: 1 CM = 5 MTR.	NORTH
DRAWING NO. D.T.P. (K) 1721 / 2025	DATED:- 10.07.2025
DRAWN BY:- RAJNEESH KUMAR (TRACER)	
CHECKED BY:- DHARMAN RAM RANGA (J.D)	PRADIP KUMAR (SD)
PLANNING ASSISTANT (VACANT)	RAJNEESH KUMAR (SD)
ASST. TOWN PLANNER	MOHIT SINGH
DIST. TOWN PLANNER	SATISH KUMAR
DEPTT. OF TOWN & COUNTRY PLANNING HARYANA	

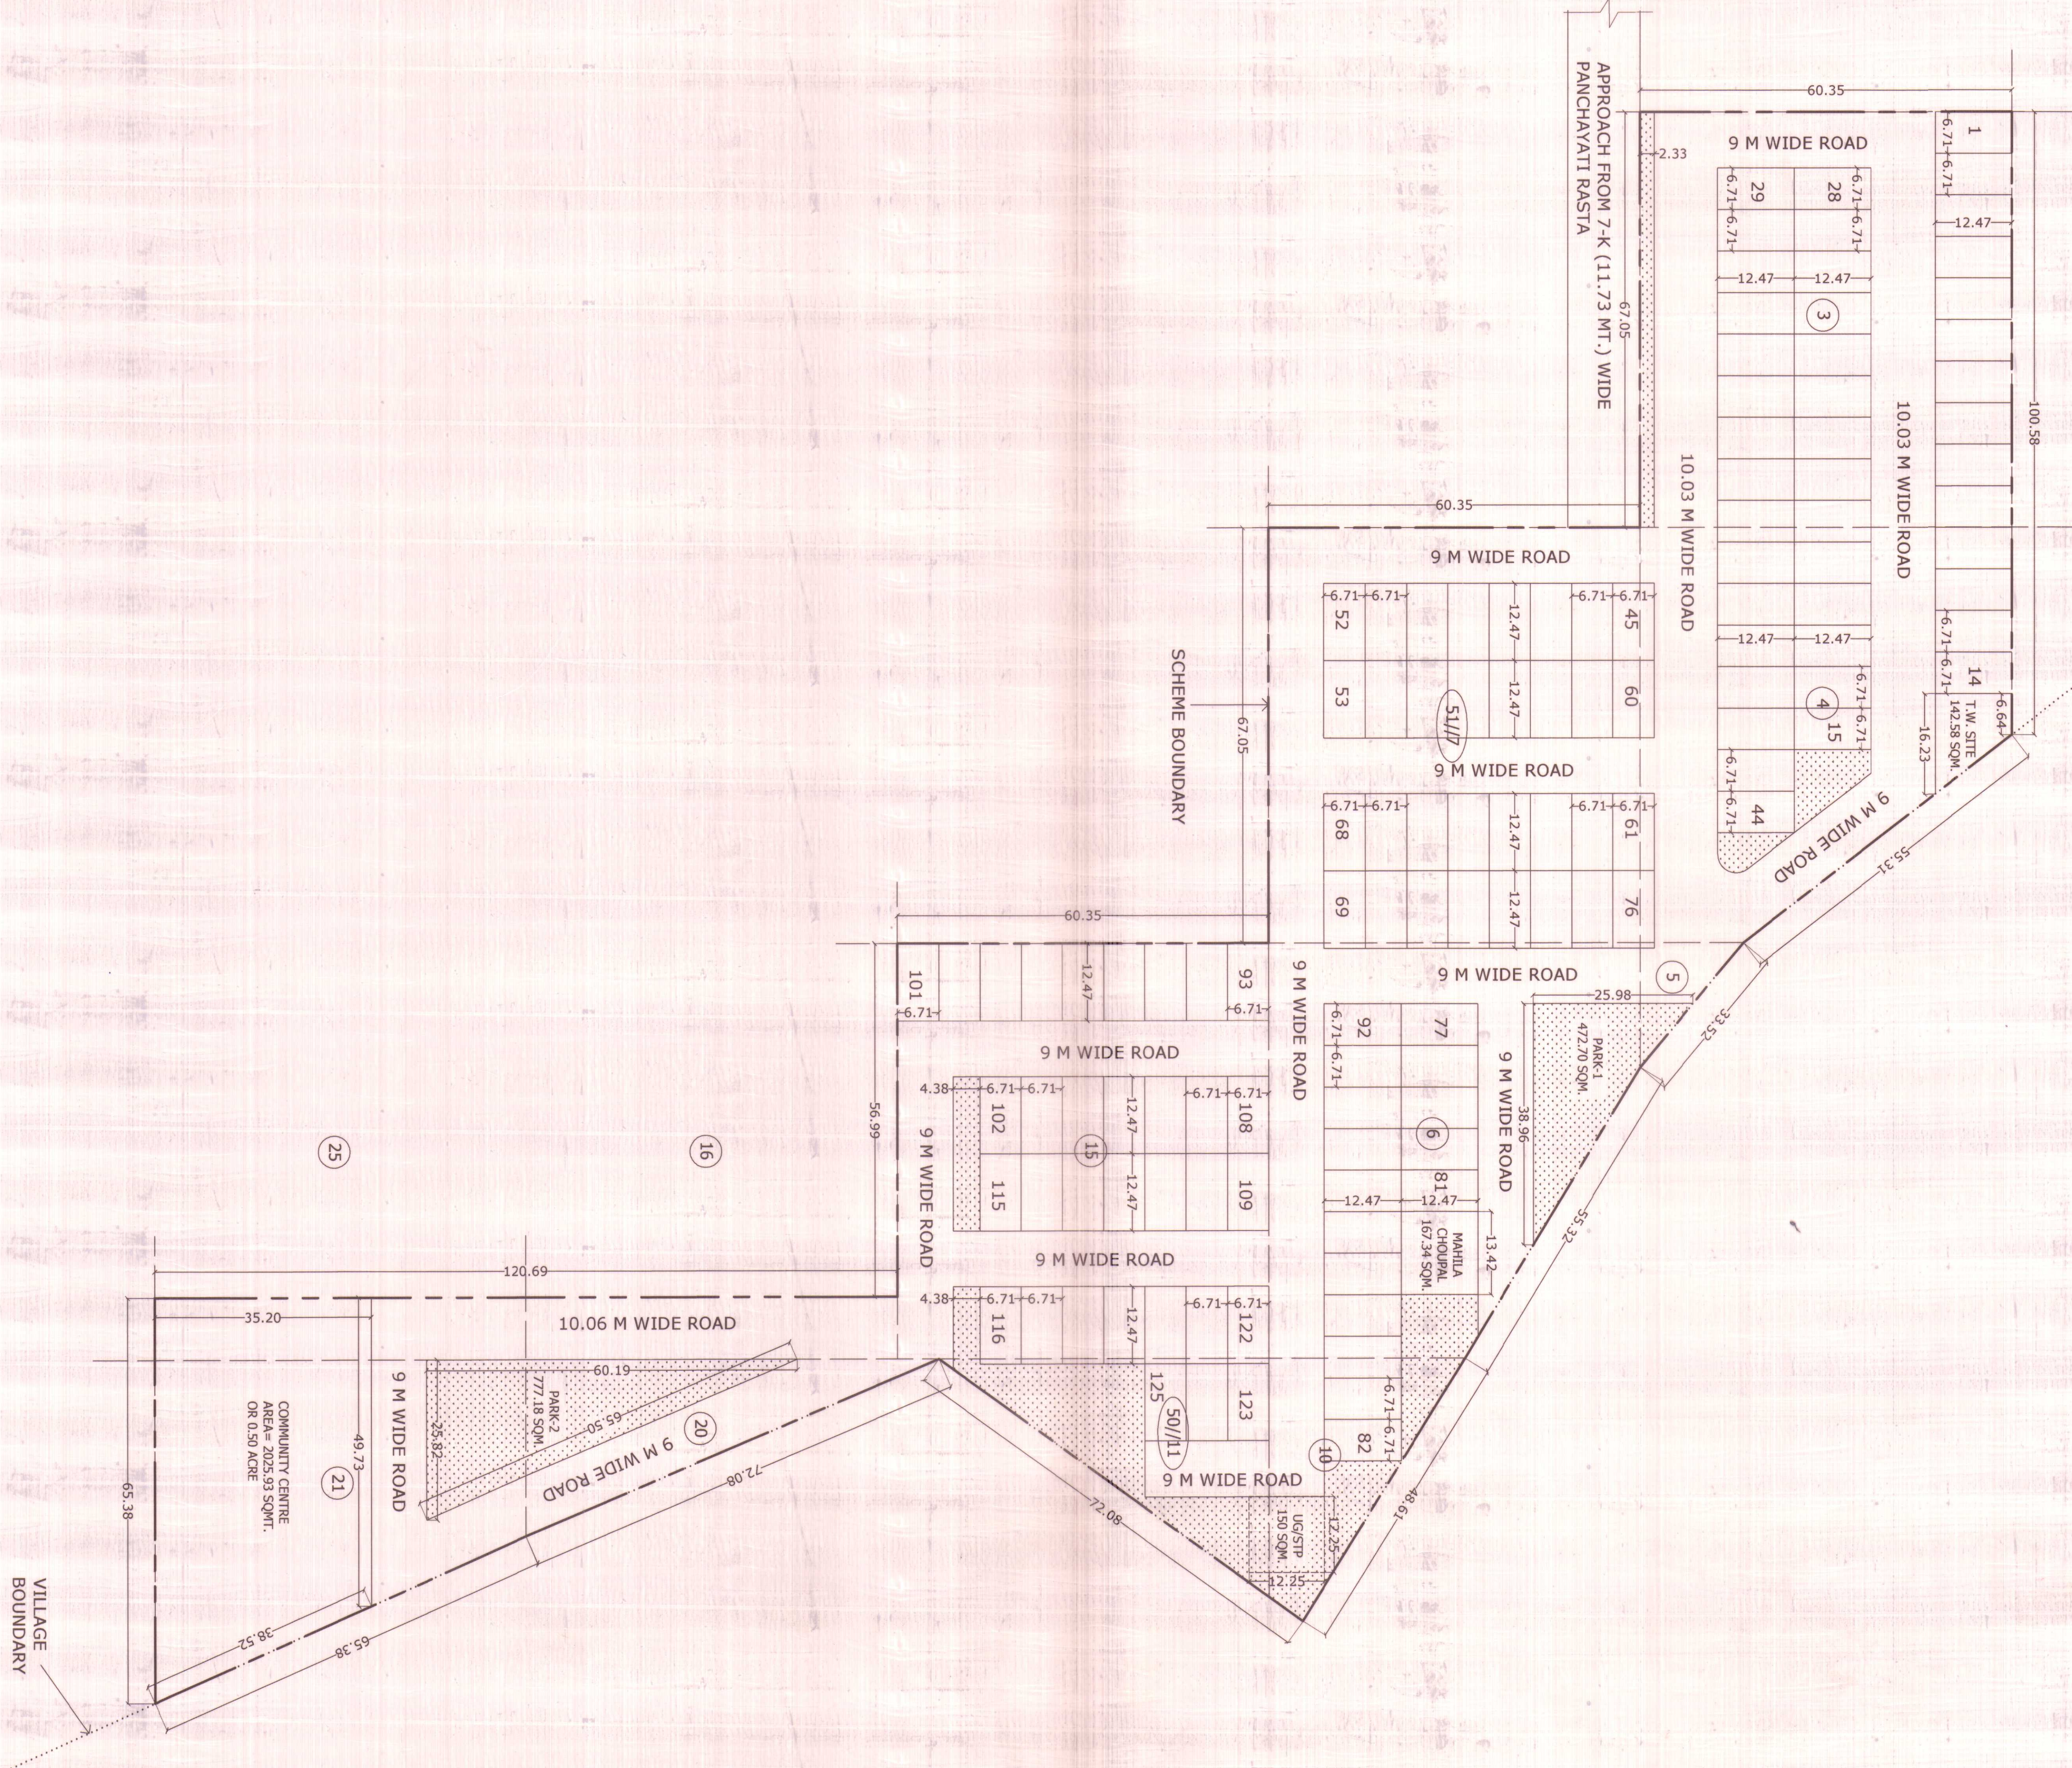

SUB DIVISIONAL OFFICER,
MISSING BLOCK, DISTRICT KARNAL,
HARYANA, CHANDIGARH

CHAIRPERSON, MMGAY-2.0, CLIM,
SENIOR TOWN PLANNER, PANCHKULA
TOWN & COUNTRY PLANNING DEPARTMENT,
HARYANA, CHANDIGARH