

LAYOUT PLAN OF HOUSING SCHEME UNDER "MUKHYAMANTRI GRAMIN AWAS YOJANA-EXTENSION" (MMGAY-E) AREA 3.82 ACRES COMPRISING IN KHASRA NOS. 6/1, 2, 3/1, 7/1/2 & 5 IN THE REVENUE ESTATE OF VILLAGE GORGARH (BEHLOLPUR VIRAN), BLOCK- INDRI, DISTRICT KARNAL.

SER. NO.	PARTICULAR	SIZE	NOS.	AREA
1.	RESI. PLOT	0.71X12.47 M	102	8534.71 SQM.
2.	MAHILA CHOUPAL	AS PER SITE	1	172.21 SQM.
3.	TUBE WELL	AS PER SITE	1	119.47 SQM.
TOTAL	PLOTTED AREA			= 8826.39 SQM. OR 2.161 ACRES

DETAILS OF AREA :-

AREA OF SCHEME	= 3.82 ACRES
PLOTTED AREA	= 2.181 ACRES (57.09%)
AREA UNDER ROADS / PARKS / OPEN SPACES	= 1.639 ACRES

LEGEND :-

	SCHEME BOUNDARY
	HT. LINE
	KILLA LINE
	VILLAGE BOUNDARY
	PARK / OPEN SPACES

NOTE:-

1. ALL DIMENSIONS ARE IN METERS.
2. THIS LAYOUT PLAN HAS BEEN PREPARED ON THE BASIS OF SAKRA PLAN PROVIDED BY BOPIO, INDI
3. THE KHASRA NOS. OF MHGAY-2.0 SCHEME FALLS OUTSIDE CONTROLLED AREA AND URBAN AREA OF DISTRICT KARNAL
4. THIS SITE DOES NOT FALL IN NCZ SURVEY REPORT APPROVED BY DCS AND SENT TO SLC.

SCALE: 1 CM = 5 MTR.	NORTH	
----------------------	-------	---

DRAWING NO. D.T.P. (K) 1736 / 2026 DATED:- 22.07.2025

Lepidota

DRAWN BY:-
RAKESH DODIA (FACER)
Date: 20/05/2024

CHECKED BY:-
DR. N. K. MONGRA (JD)
PARDEEP KUMAR (JD)

PLANNING ASSISTANT	RAMESH KUMAR (SD)	MOHT, J.E.
	(VACANT)	<i>18/06/03</i>

ASSTT. TOWN PLANNER


Mohit Singh

MOHIT SINGH

JOGINDER SINGH,
PATWARI

Siddam
DISTT. TOWN PLANNER
SATISH KUMAR

DEPTT.OF TOWN & COUNTRY PLANNING HARYANA

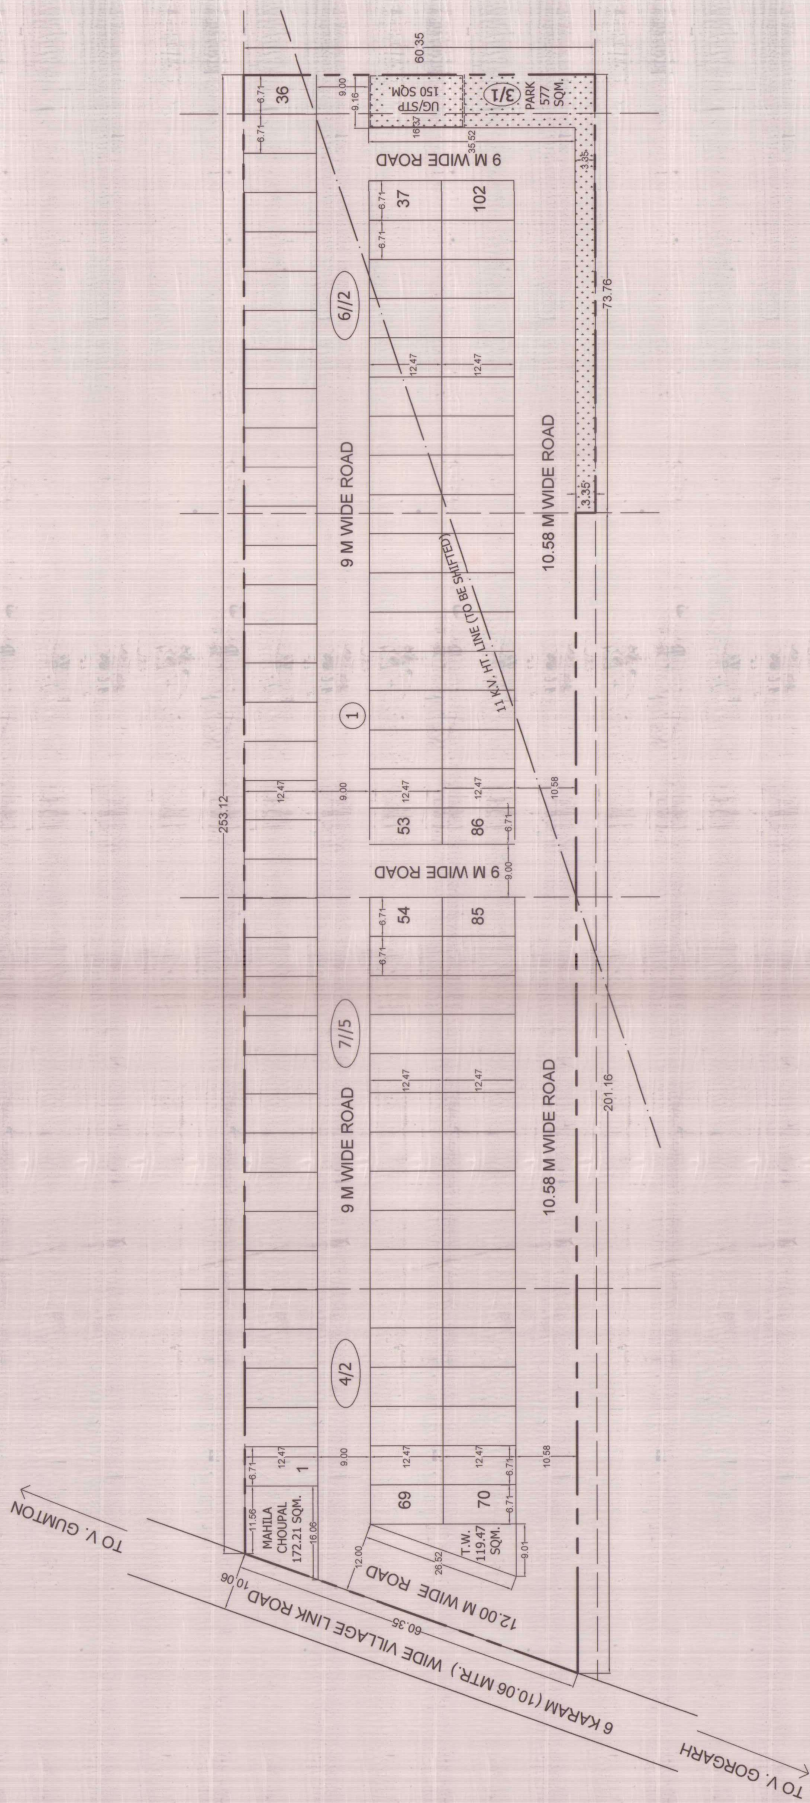

CHAIRPERSON "BAGAY-E" - CUM -
SENIOR TOWN PLANNER, PANORIKULA
TOWN & COUNTRY PLANNING DEPARTMENT,
HARYANA, CHANDIGARH

B.D.P.O., INDRA BLOCK,
DISTRICT KARNAL


SUB DIVISIONAL OFFICER,
INDRI BLOCK, DISTRICT KARNAL
PANCHAYATI RAJ DEPARTMENT,
HARYANA, CHANDIGARH