

KARNAL

LAYOUT PLAN OF HOUSING SCHEME UNDER "MUKHYAMANTRI GRAMIN AWAS YOJANA - 2.0" (MMGAY-2.0) AREA MEASURING 3.94 ACRES, COMPRISING IN KHASRA NOS. 42//16, 18/1, 23/2, 24 & 25 IN THE REVENUE ESTATE OF VILLAGE JAMBA, BLOCK-NILOKHERI, DISTRICT KARNAL.

DETAILS OF PLOTTED AREA :-

SR.NO.	PARTICULAR	SIZE	NOS.	AREA
1.	RESI. PLOT	6.71X12.47 M	104	8702.06 SQM.
2.	MAHILA CHOUPAL	AS PER SITE	1	182.05 SQM.
3.	TUBE WELL	AS PER SITE	1	129.09 SQM.
TOTAL PLOTTED AREA				= 9013.2 SQM. OR 2.227 ACRES

DETAILS OF AREA :-

AREA OF SCHEME	= 3.94 ACRES
PLOTTED AREA	= 2.227 ACRES (56.52%)
AREA UNDER ROADS / PARKS / OPEN SPACES	= 1.713 ACRES

LEGEND :-

SCHEME BOUNDARY	
HT. LINE	
KILLA LINE	
VILLAGE BOUNDARY	
PARK / OPEN SPACES	

NOTE:-

- ALL DIMENSIONS ARE IN METERS.
- THIS LAYOUT PLAN HAS BEEN PREPARED ON THE BASIS OF SAJRA PLAN PROVIDED BY BDPO, NILOKHERI.
- THE KHASRA NOS. OF MMGAY-2.0 SCHEME FALLS OUTSIDE CONTROLLED AREA AND URBAN AREA OF DISTRICT KARNAL.
- THIS SITE DOES NOT FALL IN NCZ SURVEY REPORT APPROVED BY DLSC AND SENT TO SLC.

SCALE: 1 CM = 5 MTR.

NORTH



DRAWING NO. D.T.P. (K) 1720 / 2025 DATED:- 10.07.2025

DRAWN BY:- RAJNEESH KUMAR (TRACER)


CHECKED BY:- DHANI RAM RANGA (JD) PARDEEP KUMAR (SD)

PLANNING ASSISTANT (VACANT)

ASSTT. TOWN PLANNER MOHIT SINGH

DISTT. TOWN PLANNER SATISH KUMAR

DEPTT.OF TOWN & COUNTRY PLANNING HARYANA

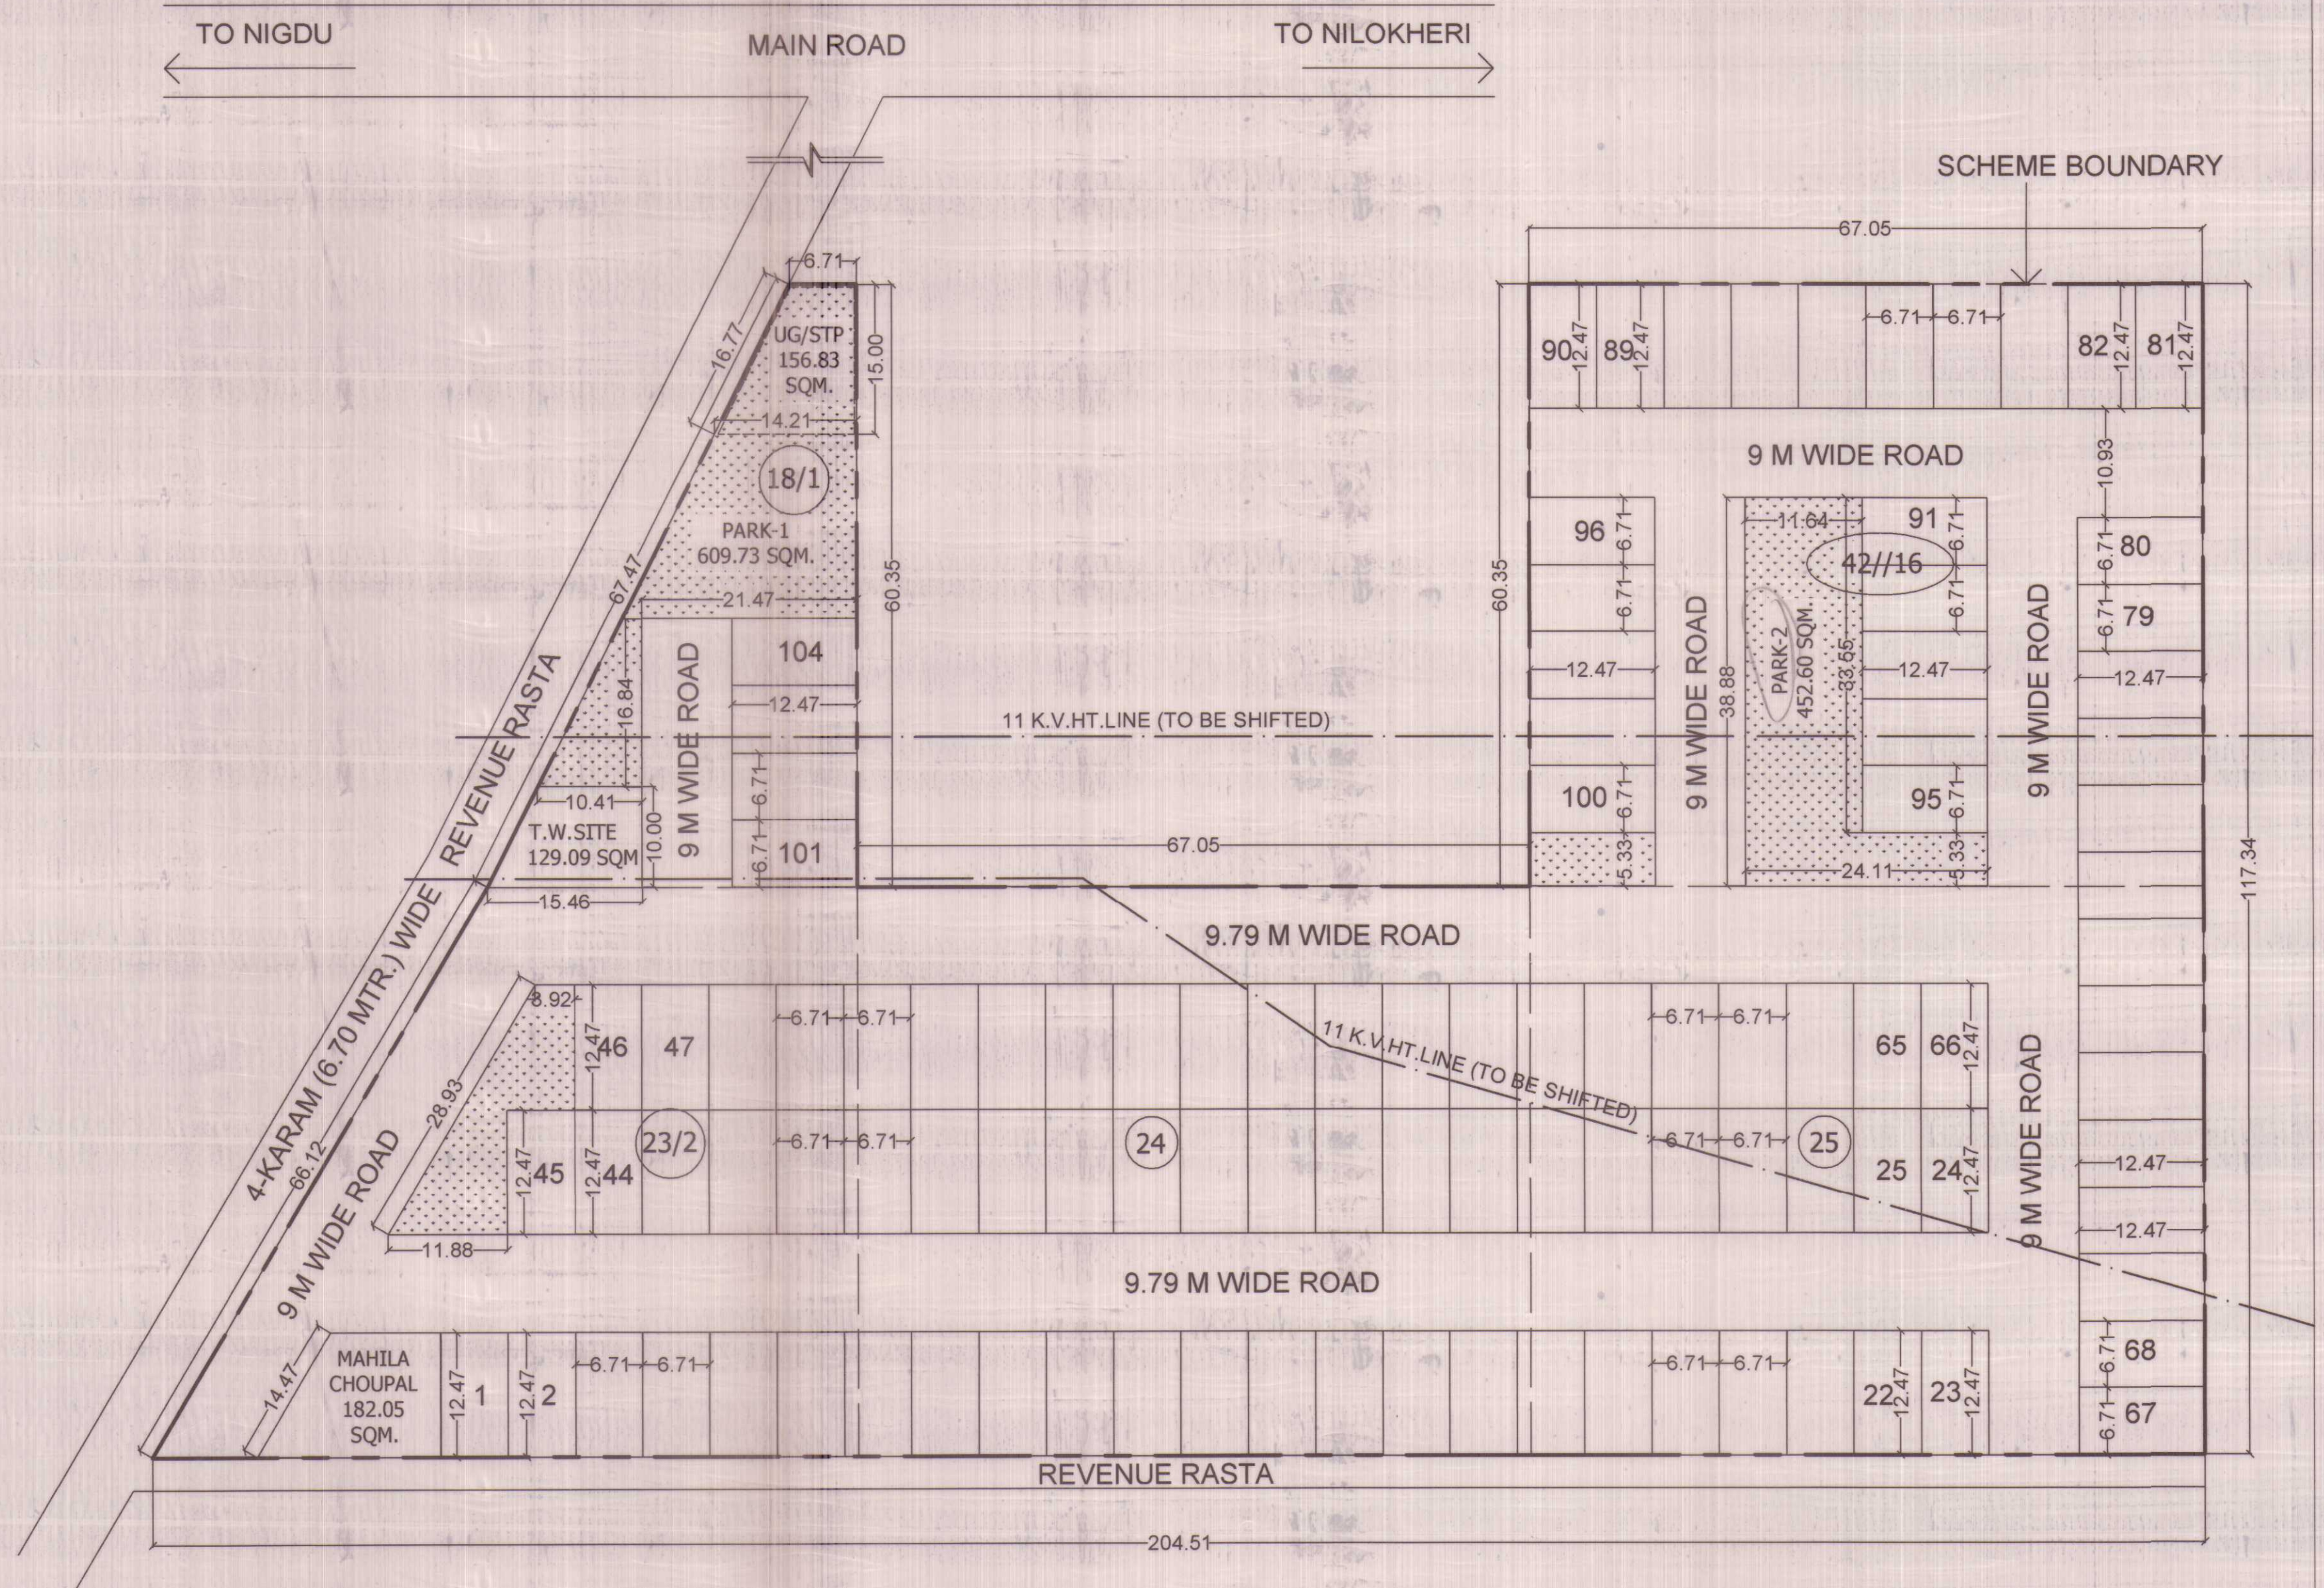

SUB DIVISIONAL OFFICER,
NILOKHERI BLOCK, DISTRICT KARNAL
PANCHAYATI RAJ DEPARTMENT,
HARYANA, CHANDIDGARH

B.D.P.O., NILOKHERI BLOCK,
DISTRICT KARNAL

CHAIRPERSON "MMGAY-2.0" - CUM -
SENIOR TOWN PLANNER, PANCHKULA
TOWN & COUNTRY PLANNING DEPARTMENT,
HARYANA, CHANDIDGARH