

KARNAL

LAYOUT PLAN OF HOUSING SCHEME UNDER
TALUKHMANTRI GRAMIN AWAS YOLANA -
20' (MANGAY-20) AREA MEASURING 14.50
ACRES COMPRISING IN KHASRA NOS. 139/17, 18,
23, 24 & 156/3, 4, 7, 8, 13, 14, 15, 16, 17, 18
AND 157/11, 20/2 IN THE REVENUE ESTATE OF
VILLAGE MUNK - BLOCK-MUNK DISTRICT
KARNAL (HARYANA).

DETAILS OF PLOTTED AREA

S.NO.	PARTICULAR	SIZE	NOS.	AREA
1.	RES. PLOT	4570.15 M	83	2081.08 SQM.
2.	COMMUNITY CENTRE	AS PER SITE	1	208.17 SQM.
3.	WATER TOWER	AS PER SITE	1	284.83 SQM.
4.	TUBE WELL	AS PER SITE	1	130.00 SQM.
TOTAL PLOTTED AREA = 2698.86 SQM. OR 7.14 ACRES				

DETAILS OF AREA

AREA OF SCHEME	= 14.50 ACRES
PLOTTED AREA	= 7.14 ACRES (44.50%)
AREA UNDER ROADS / PARKS / OPEN SPACES	= 7.46 ACRES

LEGEND

SCHEME BOUNDARY	
HT. LINE	
KOLLA LINE	
VILLAGE BOUNDARY	
PARK / OPEN SPACES	

NOTE

1. ALL DIMENSIONS ARE IN METERS.
2. THIS LAYOUT PLAN HAS BEEN PREPARED ON THE BASIS OF
SARANI PAM PROVIDED BY BORO MUNK.
3. THE KHASRA NOS. OF HANGA-20 SCHEME FALLS
OUTSIDE CONTROLLED AREA AND URBAN AREA OF DISTRICT
KARNAL.
4. THIS SITE DOES NOT FALL IN MCZ SURVEY REPORT
APPROVED BY DLSC AND SENT TO ETC.

SCALE: 1 CM = 5 MTR. NORTH

DRAWING NO. 01/P. (N) 17/04/2026 DATED-21.02.2026

DRAWN BY: D. K. R. P. M. (A. J. C.)


CHECKED BY: P. K. S. (A. J. C.)

PLANNING ASSISTANT: M. K. N.

ASSTT. TOWN PLANNER: M. K. S.

DEPT. TOWN PLANNER: G. D. S.

DEPT. OF TOWN & COUNTRY PLANNING HARYANA

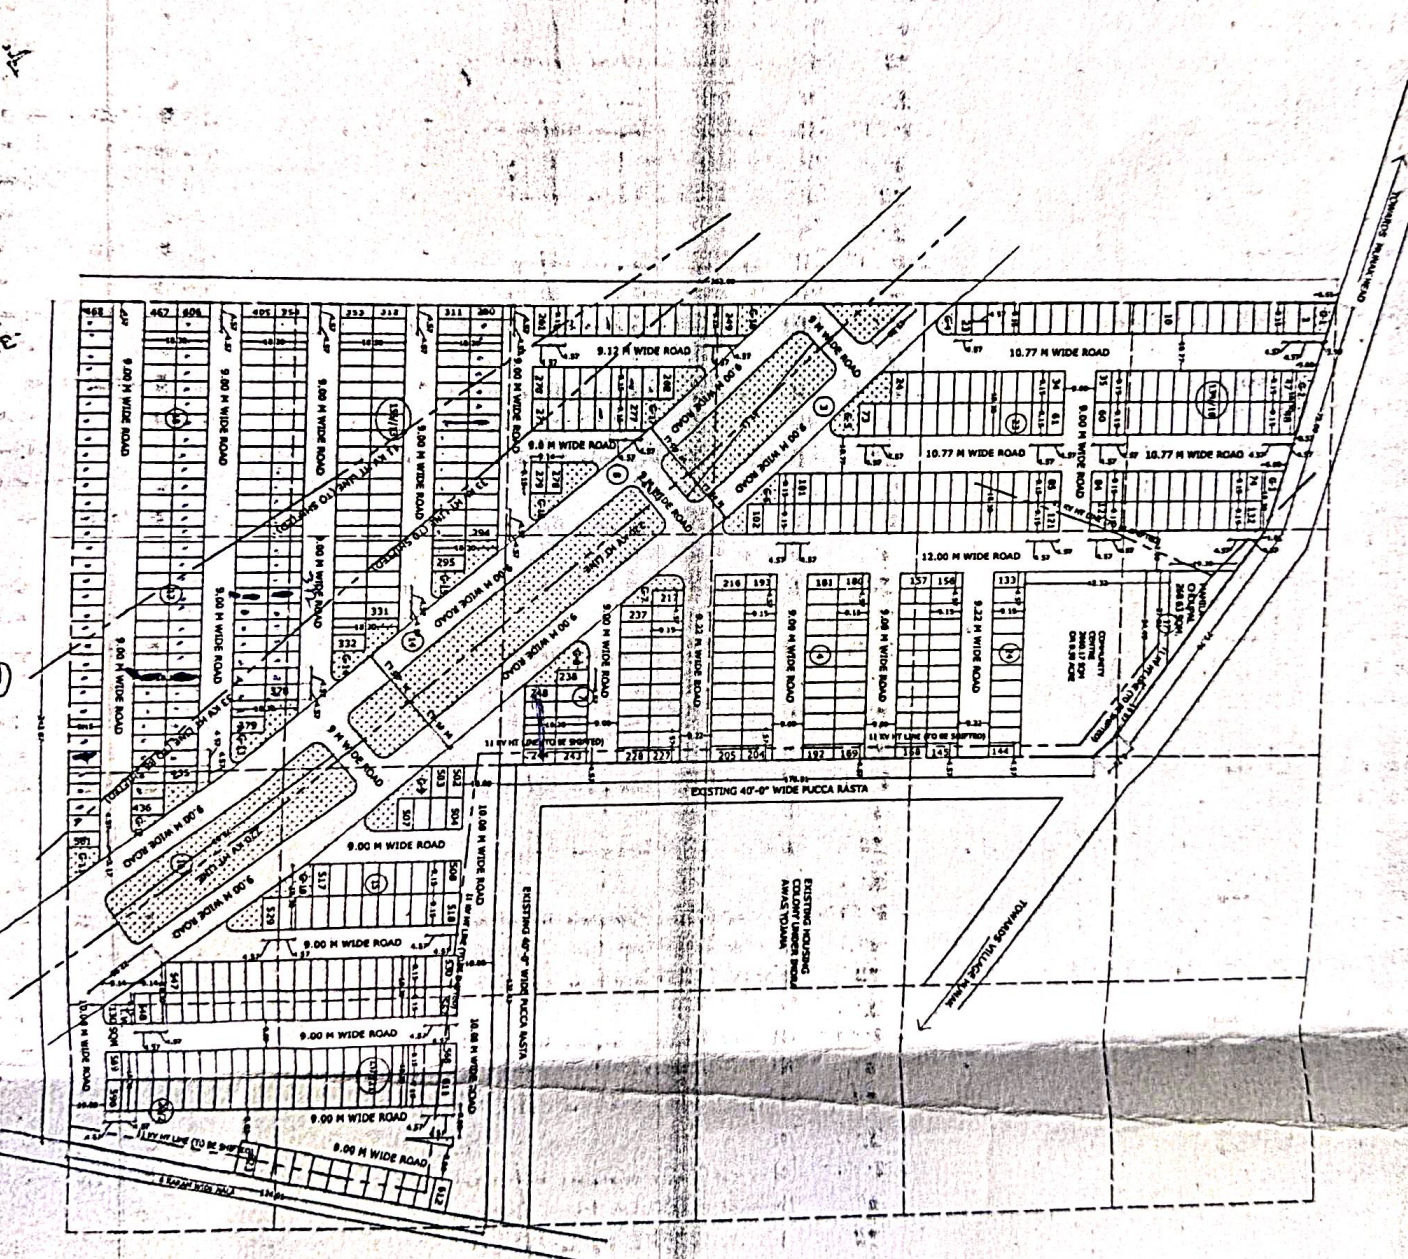

SUB DIVISIONAL OFFICER,
HARYANA CHANGIDGARH

B.D. S. J. KARNAL BLOCK,
DISTRICT KARNAL

CHANGIDGARH BLOCK,
TOWN & COUNTRY PLANNING DEPARTMENT,
HARYANA, CHANGIDGARH