

SONIPAT

LAYOUT - CUM - DEMARCATION PLAN OF
GRAM PANCHAYAT BUSANA SITE
LAND BEARING KH. NO. 52/16, 17, 24, 25 IN THE
REVENUESTATE OF VILLAGE BUSANA,
TEH. KHANPUR KALAN, DISTT. SONIPAT.

LEGEND:-
PROPOSED PLAN HOUSING FOR ALL UNDER
MUKHTYA MANTRI GRAMIN AWAS YOJNA
EXTENSION SHOWN THUS

DETAIL OF AREAS (AREA IN ACRE)
TOTAL AREA OF SITE 3.47 ACS.

DETAIL OF PLOTS

PLLOT SIZE	CATEGORY	PLLOT NOS	AREA UNDER PLOTS	AREA UNDER ROADS/GREEN / MAHILA CHOUPAL
6.71 X 12.47	100 SQ.YDS.	77	1.59 ACS.	1.88 ACS.
MAHILA CHOUPAL	200 SQ.YDS.	1	167.35 SQM.	-

NOTE:- THIS DRAWING IS PREPARED ON THE BASIS OF SAZRA PLAN
PROVIDED BY DDPO SONIPAT VIDE MEMO NO. 7398
DATED 07.07.2025

SCALE 1 C.M = 6.0 MT.



DRG.NO. D.T.P (S) 1687/25 DT. 07.07.2025

DRAWN BY :- (AJMER SINGH J.D)

SENIOR DRAFTSMAN :- (MANOJ SHARMA)


PLANNING ASSTT. (SANJAY KUMAR)

ASSTT. TOWN PLANNER:- (MANDEEP GULLA)

DISTT. TOWN PLANNER :- (AJMER SINGH)

SENIOR TOWN PLANNER :- (DHIRENDER SINGH)

DEPTT. OF T. & C. PLG. HARYANA

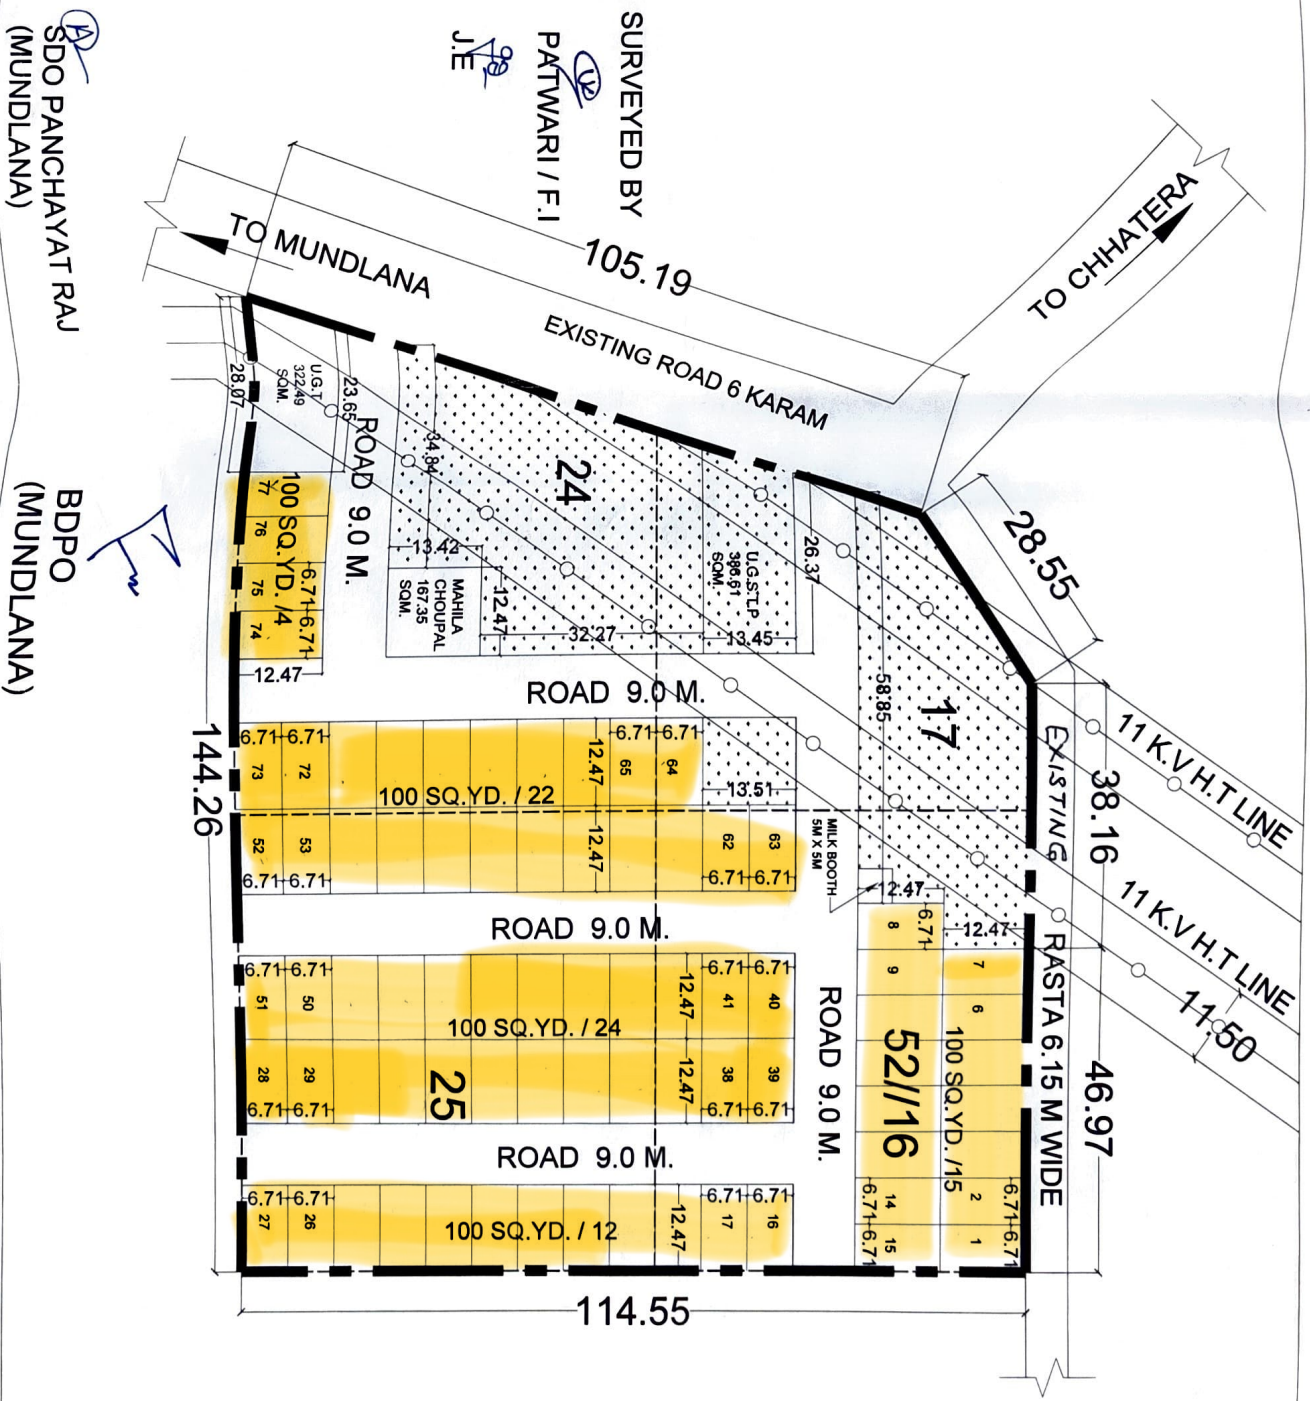

SURVEYED BY

PATWARI / F.I.

J.E.

TO MUNDLANA

TO CHHATERA

105.19

EXISTING ROAD 6 KARAM

24

ROAD 9.0 M.

ROAD 9.0 M.

MAHILA CHOUPAL
167.35 SQM.

100 SQ.YD. / 22

ROAD 9.0 M.

100 SQ.YD. / 24

100 SQ.YD. / 12

ROAD 9.0 M.

114.55

EXISTING

RASTA 6.15 M WIDE

46.97

38.16

28.55

11 K.V.H.T LINE

11 K.V.H.T LINE

11.50

144.26

SDO PANCHAYAT RAJ
(MUNDLANA)

BDPO
(MUNDLANA)