

YAMUNA NAGAR-JAGADHRI

VILLAGE - KHADRI


LAYOUT-CUM-DEMARICATION PLAN OF THE RESIDENTIAL PLOTTED COLONY UNDER MUKHYA MANTRI GRAMIN AWAS YOJANA - 2.0 (MMGAY-2.0) IN KHASRA NO. 93/5, 6, 94/1, 10 IN THE REVENUE ESTATE OF VILLAGE KHADRI, BLOCK -CHHACHHRAULI, DISTRICT YAMUNA NAGAR, (HARYANA).

AREA DETAIL:-
TOTAL LAND AREA 16187.73 SQM AS PER SURVEY

DETAIL OF PLOTS	SIZE OF PLOTS	TOTAL NOS.	AREA (SQM)
1	7.22 X 12.47	1	90.03
2 TO 16, 17 TO 27, 29 TO 46, 48 TO 51 & 53 TO 106	6.71 X 12.47	101	8480.79
16 & 28	7.108 X 12.47	2	177.20
67 & 82	7.11 X 12.47	2	177.32
TOTAL		106	8895.34

- FACILITIES PROVIDED**
1. STP 306.13 SQM.
 2. MAHILA CHOUPAL 187.38 SQM.
 3. ELECTRIC TRANSFORMER 83.67 SQM.
 4. MILK & VEGETABLE BOOTH 72.25 SQM.
 5. TUBE-WELL 85.61 SQM.
 6. I.G. 1 NO. 102.00 SQM.
 7. PARK 638.79 SQM.

AREA UNDER PLOTS = 8895.34 SQM (64.95)
AREA UNDER PUBLIC FACILITIES = 735.04 SQM
AREA UNDER PARK, I.G AND ROAD = 6557.35 SQM

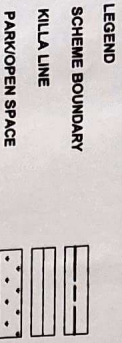

NOTE:-
THIS DRAWING HAS BEEN PREPARED ON THE BASIS OF SURVEY CUM SITE PLAN SUPPLIED BY DIRECTOR GENERAL, HOUSING FOR ALL THROUGH E-MAIL DATED 24.06.2025 SITE PLAN NO. : HARASCI/RLB/DPH/ YAMUNA NAGAR/ CHHACHHRAULI/KHADRI-33294/0001.

DRG. NO. DTP(Y) 159 / 2025 DATED 28.06.2025

SCALE: 1CM = 06 MTR



DRAWN BY RADHIKA TRICER.


FIELD INVESTIGATOR ANIL KUMAR

JUNIOR ENGINEER

CHECKED BY

MANINDER SINGH, P.A.

DEPTT. OF TOWN & COUNTRY PLANNING HARYANA

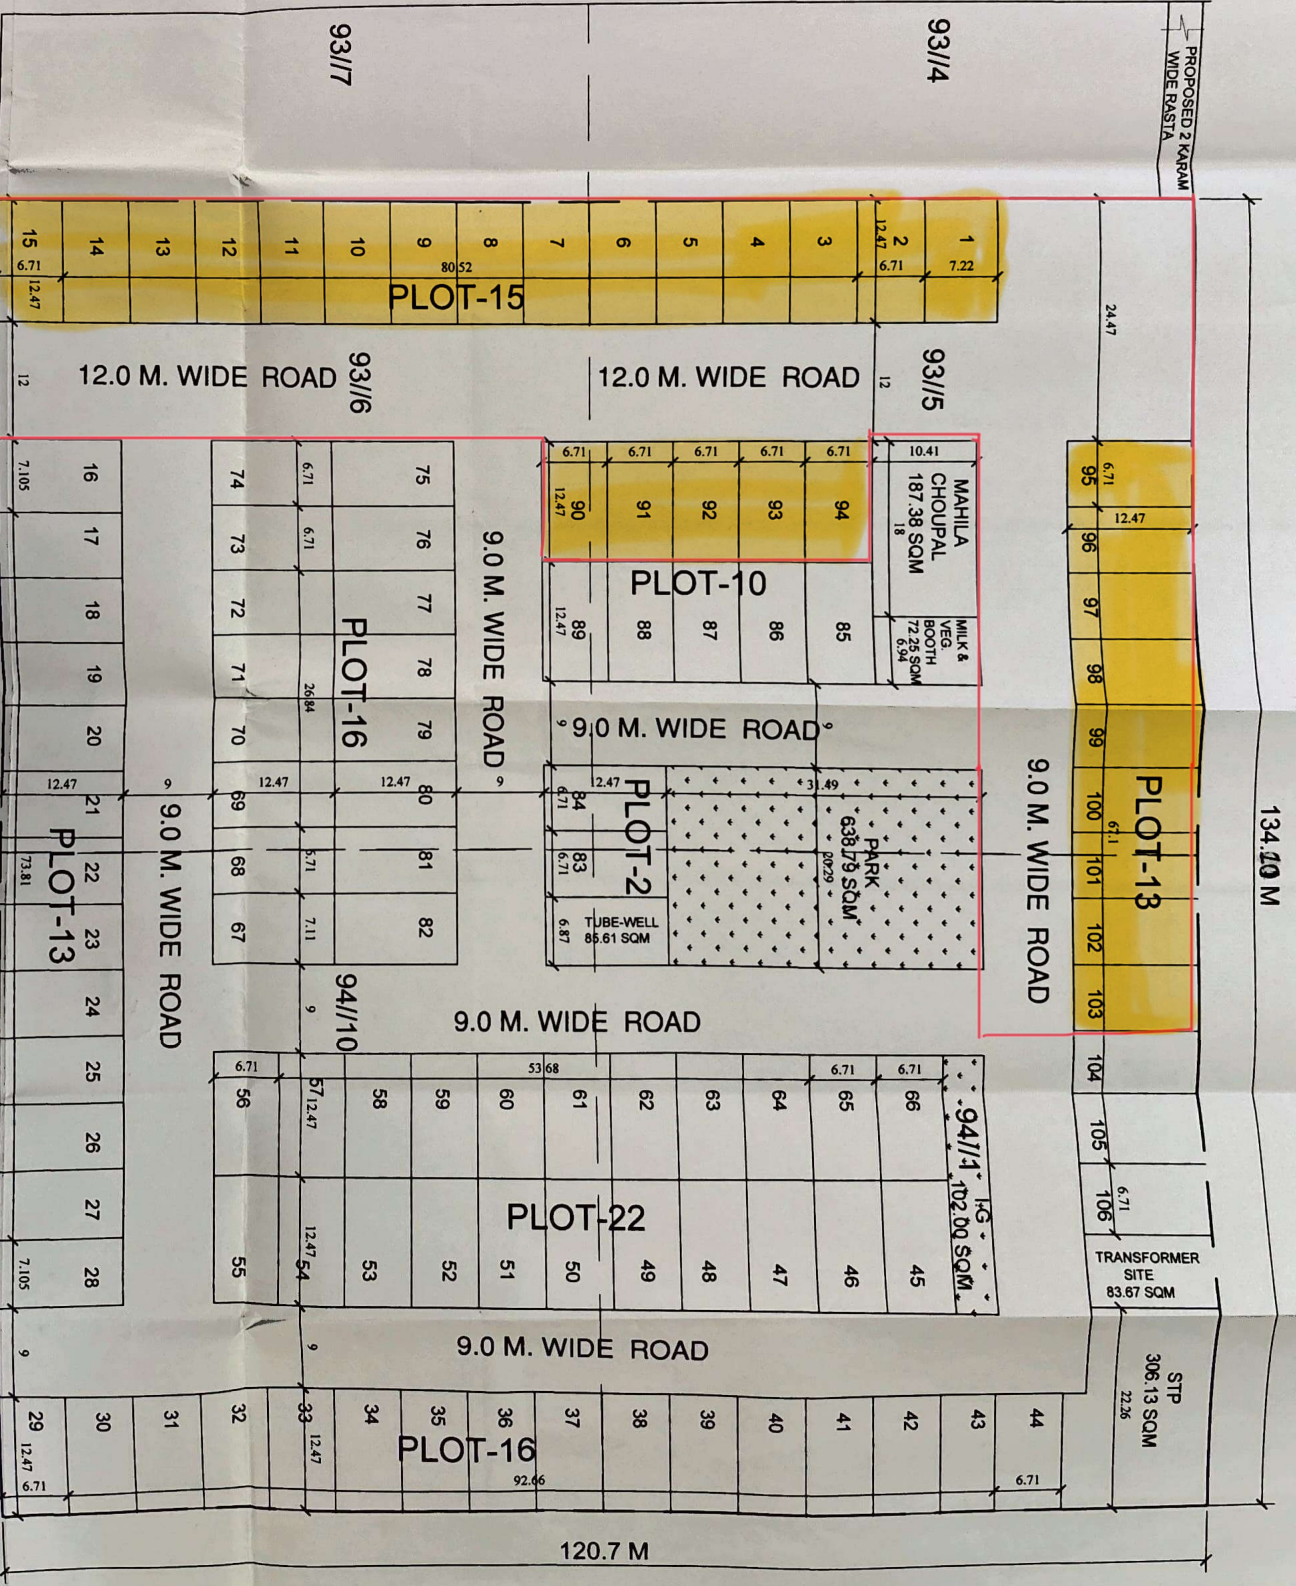

DISTRICT TOWN PLANNER (MEMBER)
YAMUNA NAGAR

BLOCK DEVELOPMENT & PANCHAYAT OFFICER, (MEMBER),
YAMUNA NAGAR

SUB DIVISIONAL OFFICER
PANCHAYATI RAJ (MEMBER),
YAMUNA NAGAR.

SENIOR TOWN PLANNER, (CHAIRMAN)
PANCHKULA