

2.57—
AGRICULTURE ZONE

SONIPAT

LAYOUT - CUM - DEMARCATION PLAN OF GRAM PANCHAYAT
SOHTI SITE

LAND BEARING KH. NO.64//11/1,11/3,20,21,22,23,65//2,3,4
IN THE REVENUE ESTATE OF VILLAGE SOHTI, TEHSIL
KHARKHODA, DISTT. SONIPAT.

LEGEND:-
PROPOSED PLAN HOUSING FOR ALL UNDER
MUKHYA MANTRI GRAMIN AWAS YOJNA
EXTENSION SHOWN THUS

DETAIL OF AREAS (AREA IN ACRE)

TOTAL AREA OF SITE 7.97 ACS.

DETAIL OF PLOTS

PLOT SIZE	CATEGORY	PLOT NOS	AREA UNDER PLOTS	AREA UNDER ROADS/GREEN / MAHILACHOUPAL /COMMUNITY CENTRE
6.71 X 12.47	100 SQ.YDS.	205	4.24 ACS.	3.73 ACS.

MAHILA
CHOUPAL 200 SQ.YDS. 1 168.58 SQM. -

COMMUNITY 0.5 ACS. 1 2258.50 SQM. -

NOTE:- THIS DRAWING IS PREPARED ON THE BASIS OF S.A. PLAN
PROVIDED BY DDPO, SONIPAT VIDE MEMO NO. 20
DATED 02.01.2025

SCALE 1 C.M = 6.0MT.

DRG.NO. D.T.P (S)1651/25 DT. 14.01.2025

CHEKED BY:- (AJMER SINGH)


PLANNING ASSTT. (SANJAY KUMAR)


ASSTT. TOWN PLANNER:- (ANIL KUMAR)

DISTT. TOWN PLANNER :- (AJMER SINGH)

SENIOR TOWN PLANNER :- (DHIRENDER SINGH)

DEPTT. OF T. & C. PLG. HARYANA

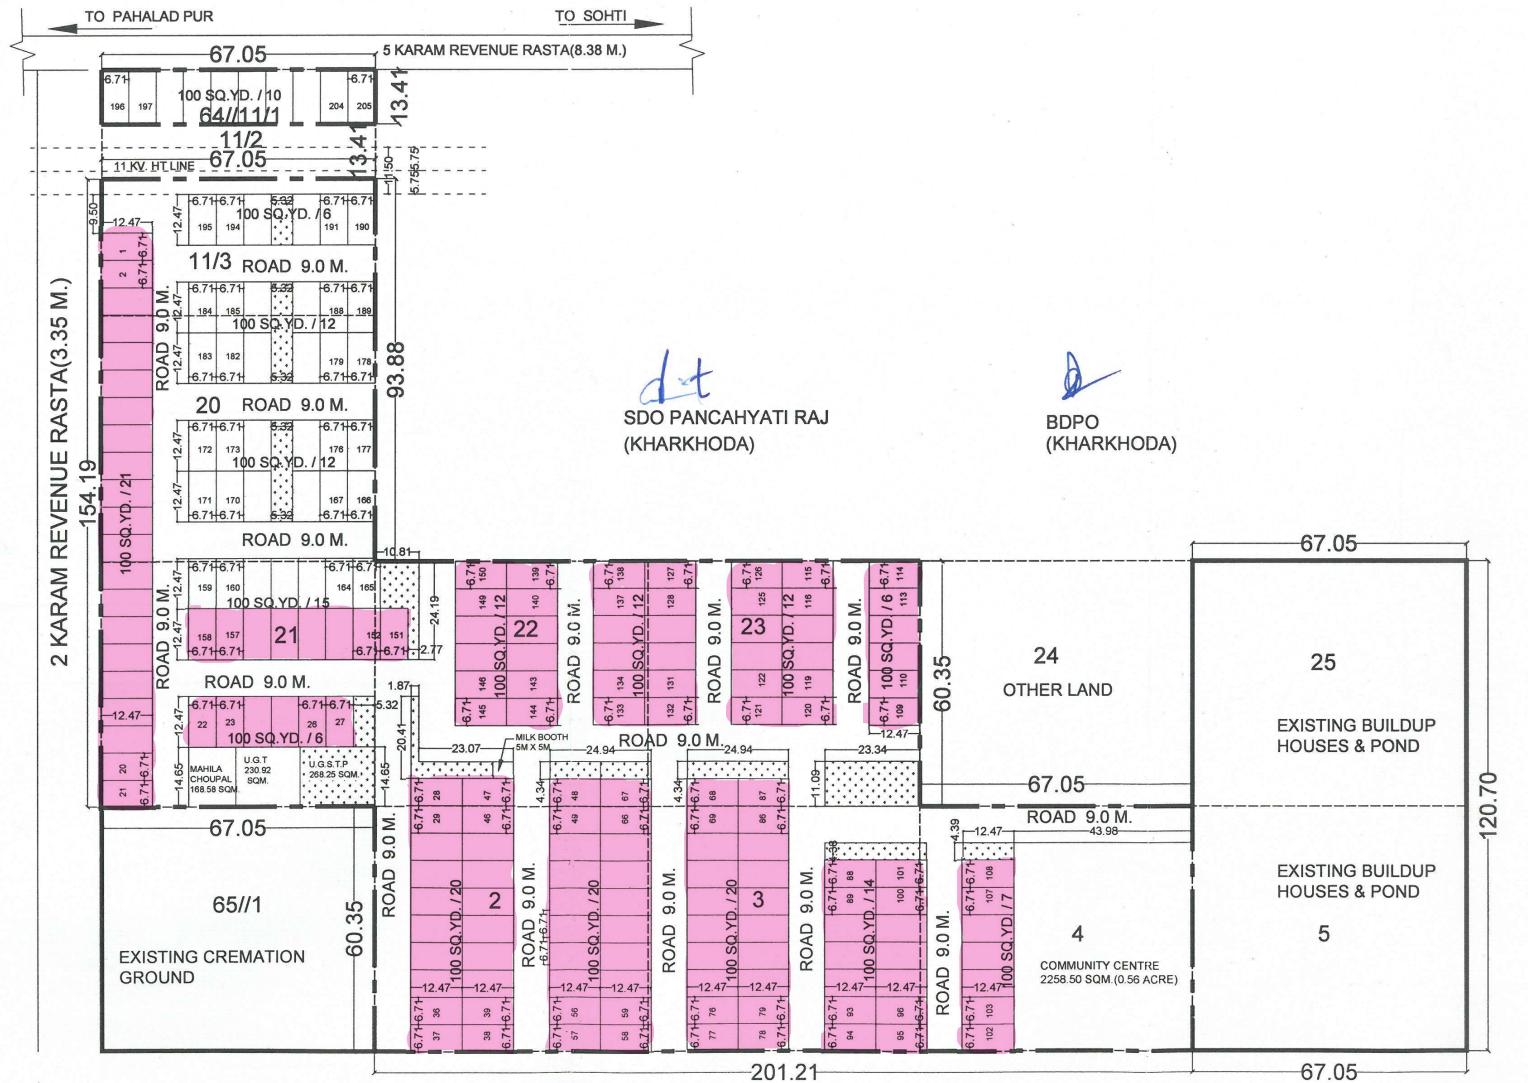

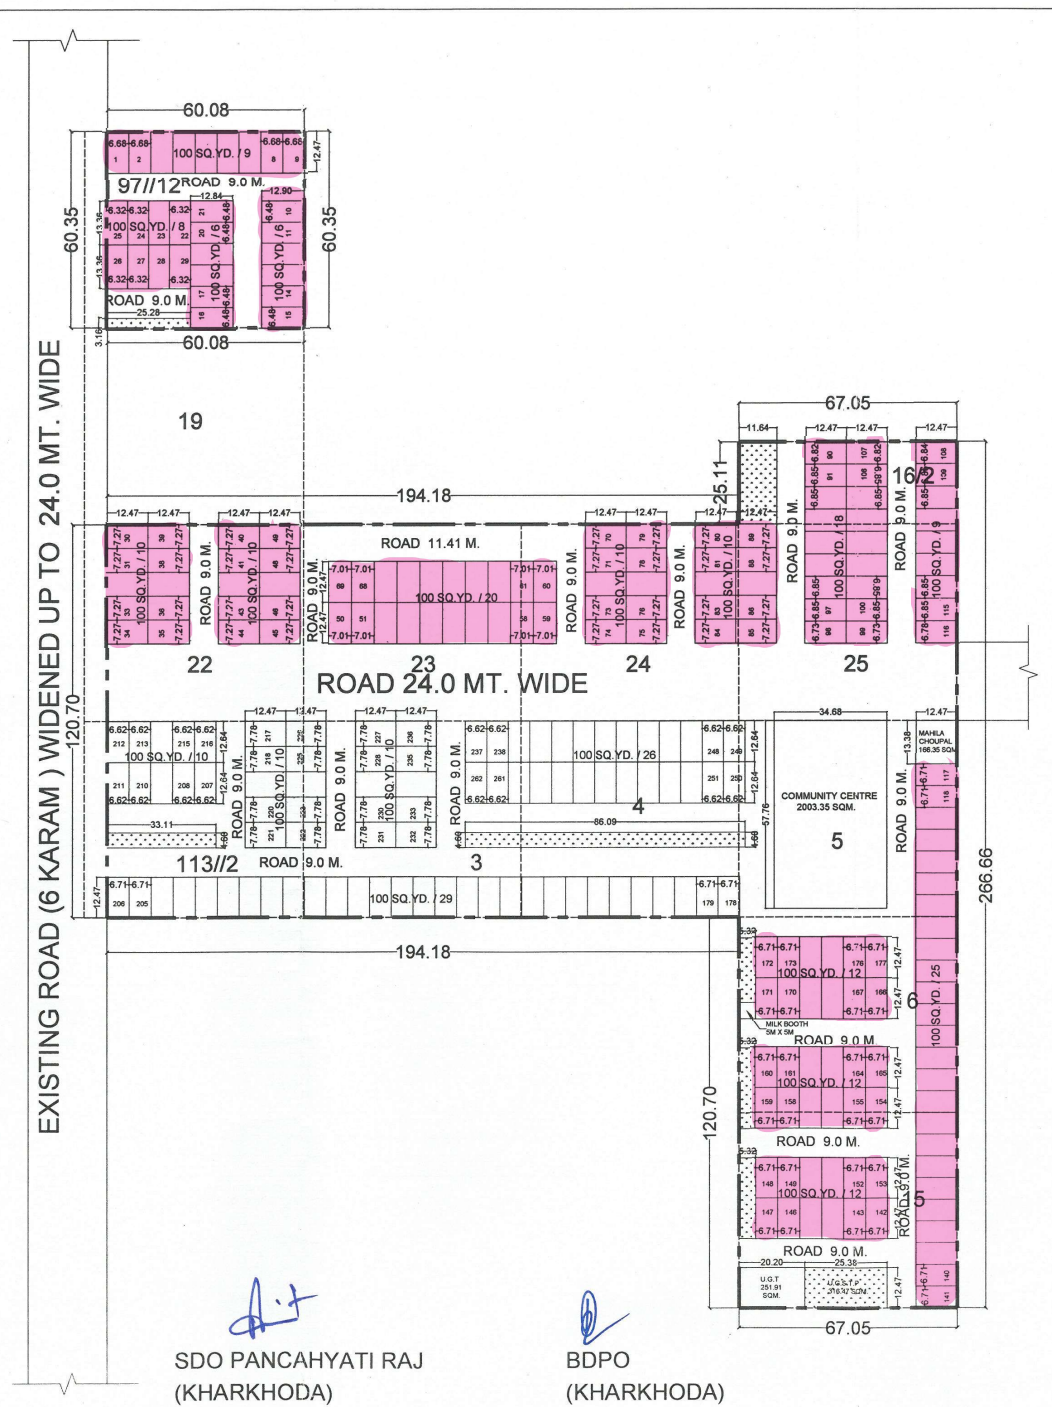

SONIPAT

LAYOUT - CUM - DEMARCATION PLAN OF GRAM PANCHAYAT RATTAN GARH SITE

LAND BEARING KH. NO. 12//12/2, 19, 22, 23 IN THE REVENUE ESTATE OF VILLAGE BAGRU TEH. & DISTT. SONIPAT

LEGEND:-

PROPOSED PLAN HOUSING FOR ALL UNDERMUKHYA MANTRI GRAMIN AWAS YOJNA EXTENSION SHOWN THUS

DETAIL OF AREAS (AREA IN ACRE)

TOTAL AREA OF SITE 3.12 ACS.

DETAIL OF PLOTS

PLOT SIZE	CATEGORY.	PLOT NOS	AREA UNDER PLOTS	AREA UNDER ROADS/ GREEN/MAHILA CHOUPAL
6.71 X 12.47	100 SQ.YDS. 90		1.86 ACS.	1.26 ACS.
MAHILA CHOUPAL	200 SQ.YDS. 1		168.97 SQM.	-

NOTE:- THIS DRAWING IS PREPARED ON THE BASIS OF SAZRA PLAN PROVIDED BY DDPO, SONIPAT VIDE MEMO NO. 20 DATED 02.01.2025

SCALE 1 C.M = 6.0MT.



DRG.NO. D.T.P (S) 1649/25 DT. 14.01.2025

CHEKED BY:- (AJMER SINGH J.D.)

PLANNING ASSTT. (SANJAY KUMAR)

ASSTT. TOWN PLANNER:- (MANDEEP GULIA)


DISTT. TOWN PLANNER :- (AJMER SINGH)

SENIOR TOWN PLANNER :- (DHIRENDER SINGH)

DEPTT. OF T. & C. PLG. HARYANA

SDO PANCAHYATI RAJ (SONIPAT)

BDPO (SONIPAT)

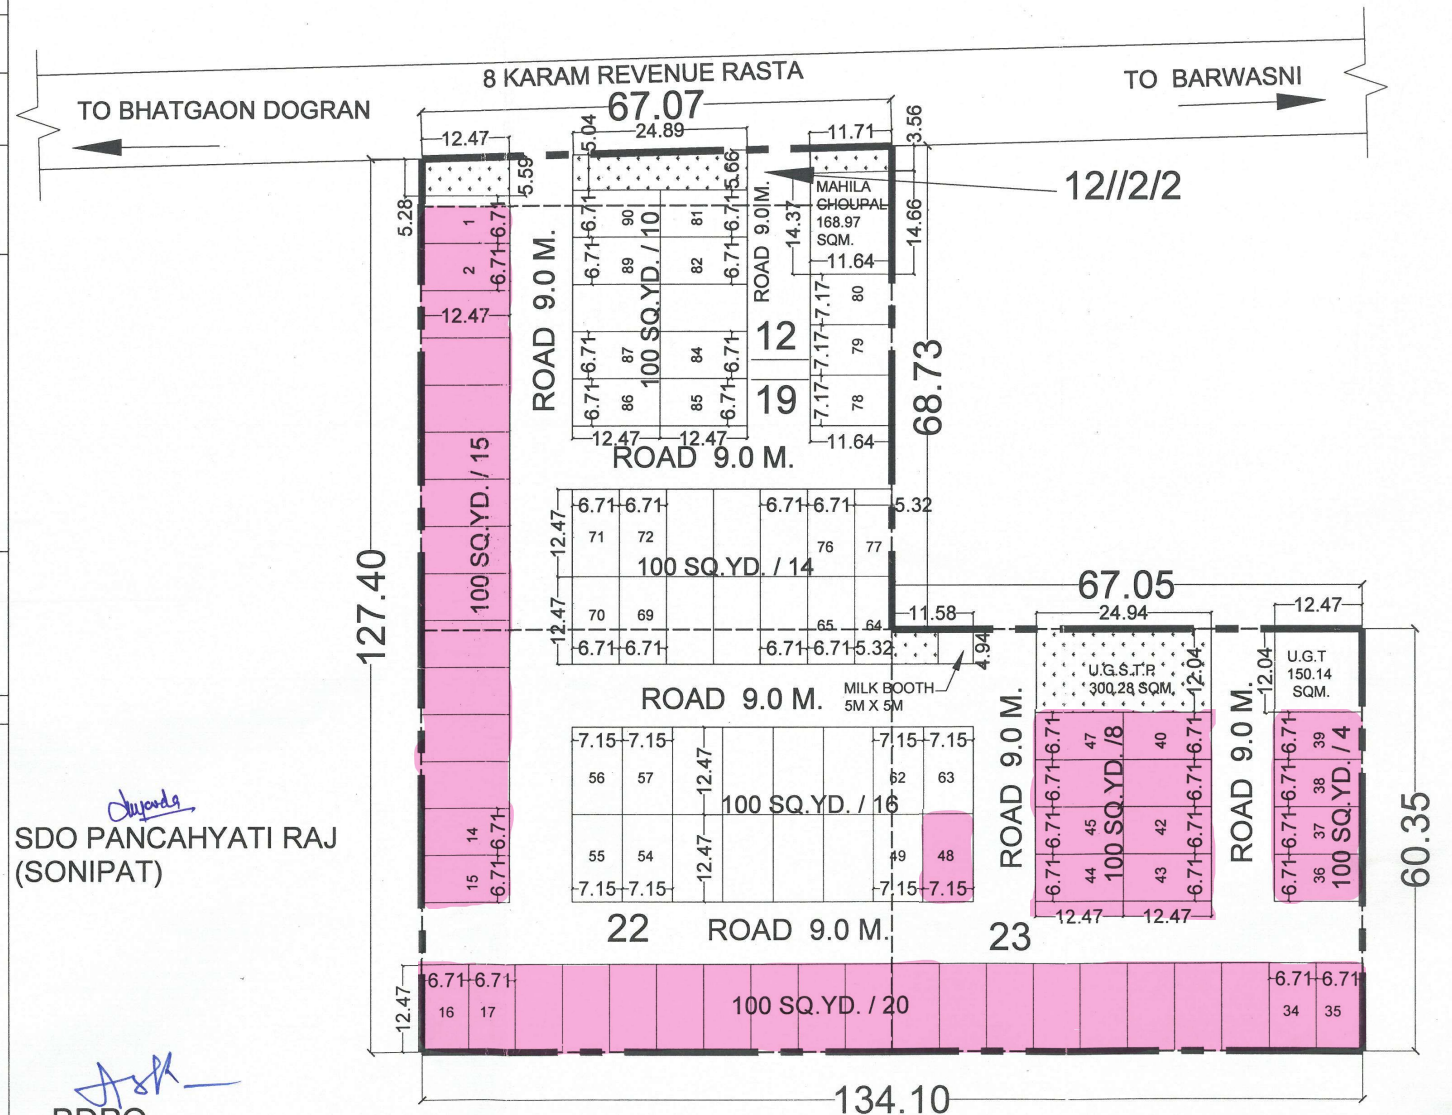

SONIPAT

LAYOUT - CUM - DEMARCATION PLAN OF GRAM
PANCHAYAT JAKHAULI SITE

LAND BEARING KH. NO. 145//5,6,7,8,15 IN THE REVENUE
ESTATE OF VILLAGE JAKHAULI, TEHSIL RAI,
DISTT. SONIPAT.

LEGEND:-

PROPOSED PLAN HOUSING FOR ALL UNDER
MUKHYA MANTRI GRAMIN AWAS YOJNA
EXTENSION SHOWN THUS



DETAIL OF AREAS

(AREA IN ACRE)

TOTAL AREA OF SITE

4.85 ACS.

DETAIL OF PLOTS

PLOT SIZE	CATEGORY.	PLOT NOS	AREA UNDER PLOTS	AREA UNDER ROADS / GREEN/MAHILA CHOUPAL
6.71 X 12.47	100 SQ.YDS.	137	2.83 ACS.	2.02 ACS.
MAHILA CHOUPAL	200 SQ.YDS.	1	174.60 SQM.	-

NOTE:- THIS DRAWING IS PREPARED ON THE BASIS OF **SAZRA** PLAN
PROVIDED BY DDPO, SONIPAT VIDE MEMO NO. 20
DATED 02.01.2025

SCALE 1 C.M = 6.0MT.



DRG.NO. D.T.P (S)1648/25

DT. 14.01.2025

DRAWN BY :-

(AJMER SINGH J.D.)

PLANNING ASSTT.

(SANJAY KUMAR)

ASSTT. TOWN PLANNER:-

(MANDEEP GULIA)

DISTT. TOWN PLANNER :-

(AJMER SINGH)

SENIOR TOWN PLANNER :-

(DHIRENDER SINGH)

DEPTT. OF T. & C. PLG. HARYANA



SONIPAT

LAYOUT - CUM - DEMARCATION PLAN OF GRAM PANCHAYAT BAJIDPUR SABOLI SITE

LAND BEARING KH. NO. 6//25, 7//5, 6, 14, 15 IN THE REVENUE ESTATE OF VILLAGE BAJIDPUR SABOLI TEH. RAI, DISTT. SONIPAT

LEGEND:-
PROPOSED PLAN HOUSING FOR ALL UNDER MUKHYA MANTRI GRAMIN AWAS YOJNA EXTENSION SHOWN THUS


DETAIL OF AREAS		(AREA IN ACRE)
TOTAL AREA OF SITE		3.13 ACS.
DETAIL OF PLOTS		
PLOT SIZE	CATEGORY. PLOT NOS	AREA UNDER PLOTS ROADS/GREEN / MAHILA CHOUPAL
6.71 X 12.47 100 SQ.YDS.	85	1.76 ACS.
MAHILA CHOUPAL	200 SQ.YDS. 1	167.92 SQM.

NOTE:- THIS DRAWING IS PREPARED ON THE BASIS OF 'SAZRA' PLAN PROVIDED BY DDPO, SONIPAT VIDE MEMO NO. 20 DATED 02.01.2025

SCALE 1 C.M = 6.0MT.



DRG.NO.	D.T.P (S)/1647/25	DT. 14.01.2025
DRAWN BY :-	 (AJMER SINGH J.D.)	
PLANNING ASSTT.	 (SANJAY KUMAR)	
ASSTT. TOWN PLANNER:-	 (MANDEEP GULIA)	
DISTT. TOWN PLANNER :-	 (AJMER SINGH)	
SENIOR TOWN PLANNER :-	 (DHIRENDER SINGH)	
DEPTT. OF T. & C. PLG. HARYANA		

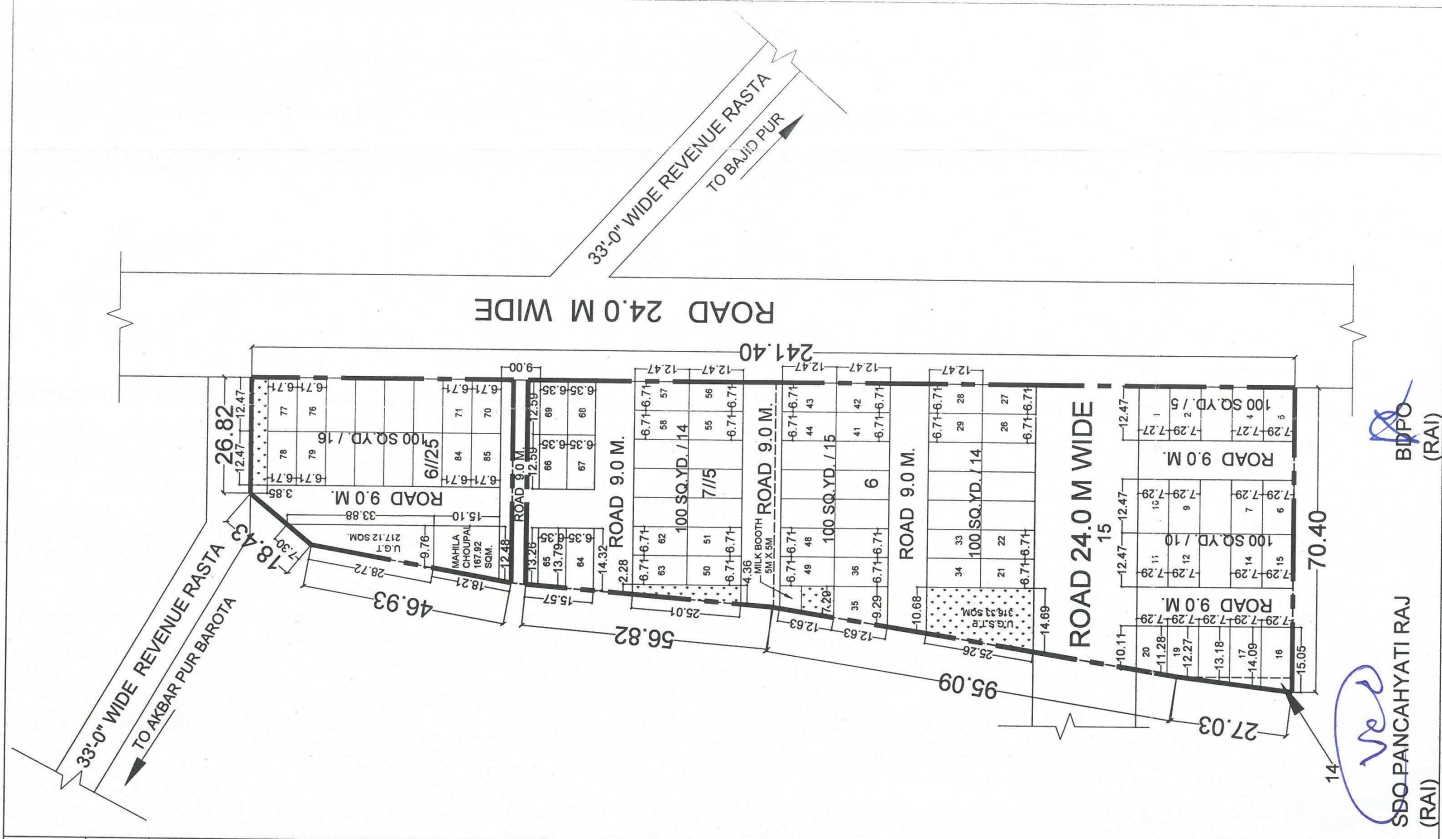

LAYOUT - CUM - DEMARCATION PLAN OF
GRAM PANCHAYAT KHIZARPUR AHIR SITE

LAND BEARING KH. NO. 30//5,6,31//1,2,10 IN THE
REVENUE STATE OF VILLAGE KHIZARPUR AHIR,
TEH. GANAUR, DISTT. SONIPAT.

LEGEND:-

PROPOSED PLAN HOUSING FOR ALL UNDER
MUKHYA MANTRI GRAMIN AWAS YOJNA
EXTENSION SHOWN THUS

DETAIL OF AREAS

(AREA IN ACRE)

TOTAL AREA OF SITE

4.40 ACS.

DETAIL OF PLOTS

PLOT SIZE	CATEGORY.	PLOT NOS	AREA UNDER PLOTS	AREA UNDER ROADS/GREEN / MAHILA CHOUPAL
6.71 X 12.47	100 SQ.YDS.	127	2.62 ACS.	1.78 ACS.

MAHILA	200 SQ.YDS.	1	170.91 SQM.
--------	-------------	---	-------------

NOTE:- THIS DRAWING IS PREPARED ON THE BASIS OF SAZRAPLAN PROVIDED BY DDPO, SONIPAT VIDE MEMO NO. 20 DATED 02.01.2025

SCALE 1 C.M = 6.0MT.



DRG.NO. D.T.P (S) 1646/25

DT.14.01.2025

DRAWN BY :-

(AJMER SINGH J.D)

PLANNING ASSTT.

(SANJAY KUMAR)

ASSTT. TOWN PLANNER:-

(KAPIL RAO)

DISTT. TOWN PLANNER :-

(AJMER SINGH)

SENIOR TOWN PLANNER :-

(DHIRENDER SINGH)

DEPTT. OF T. & C. PLG. HARYANA

