


SECTOR - 9, DADRI

AREA = 6.50 ACRES, PLOTS = 512, 1 MARLA PLOT = 30 SQ YDS

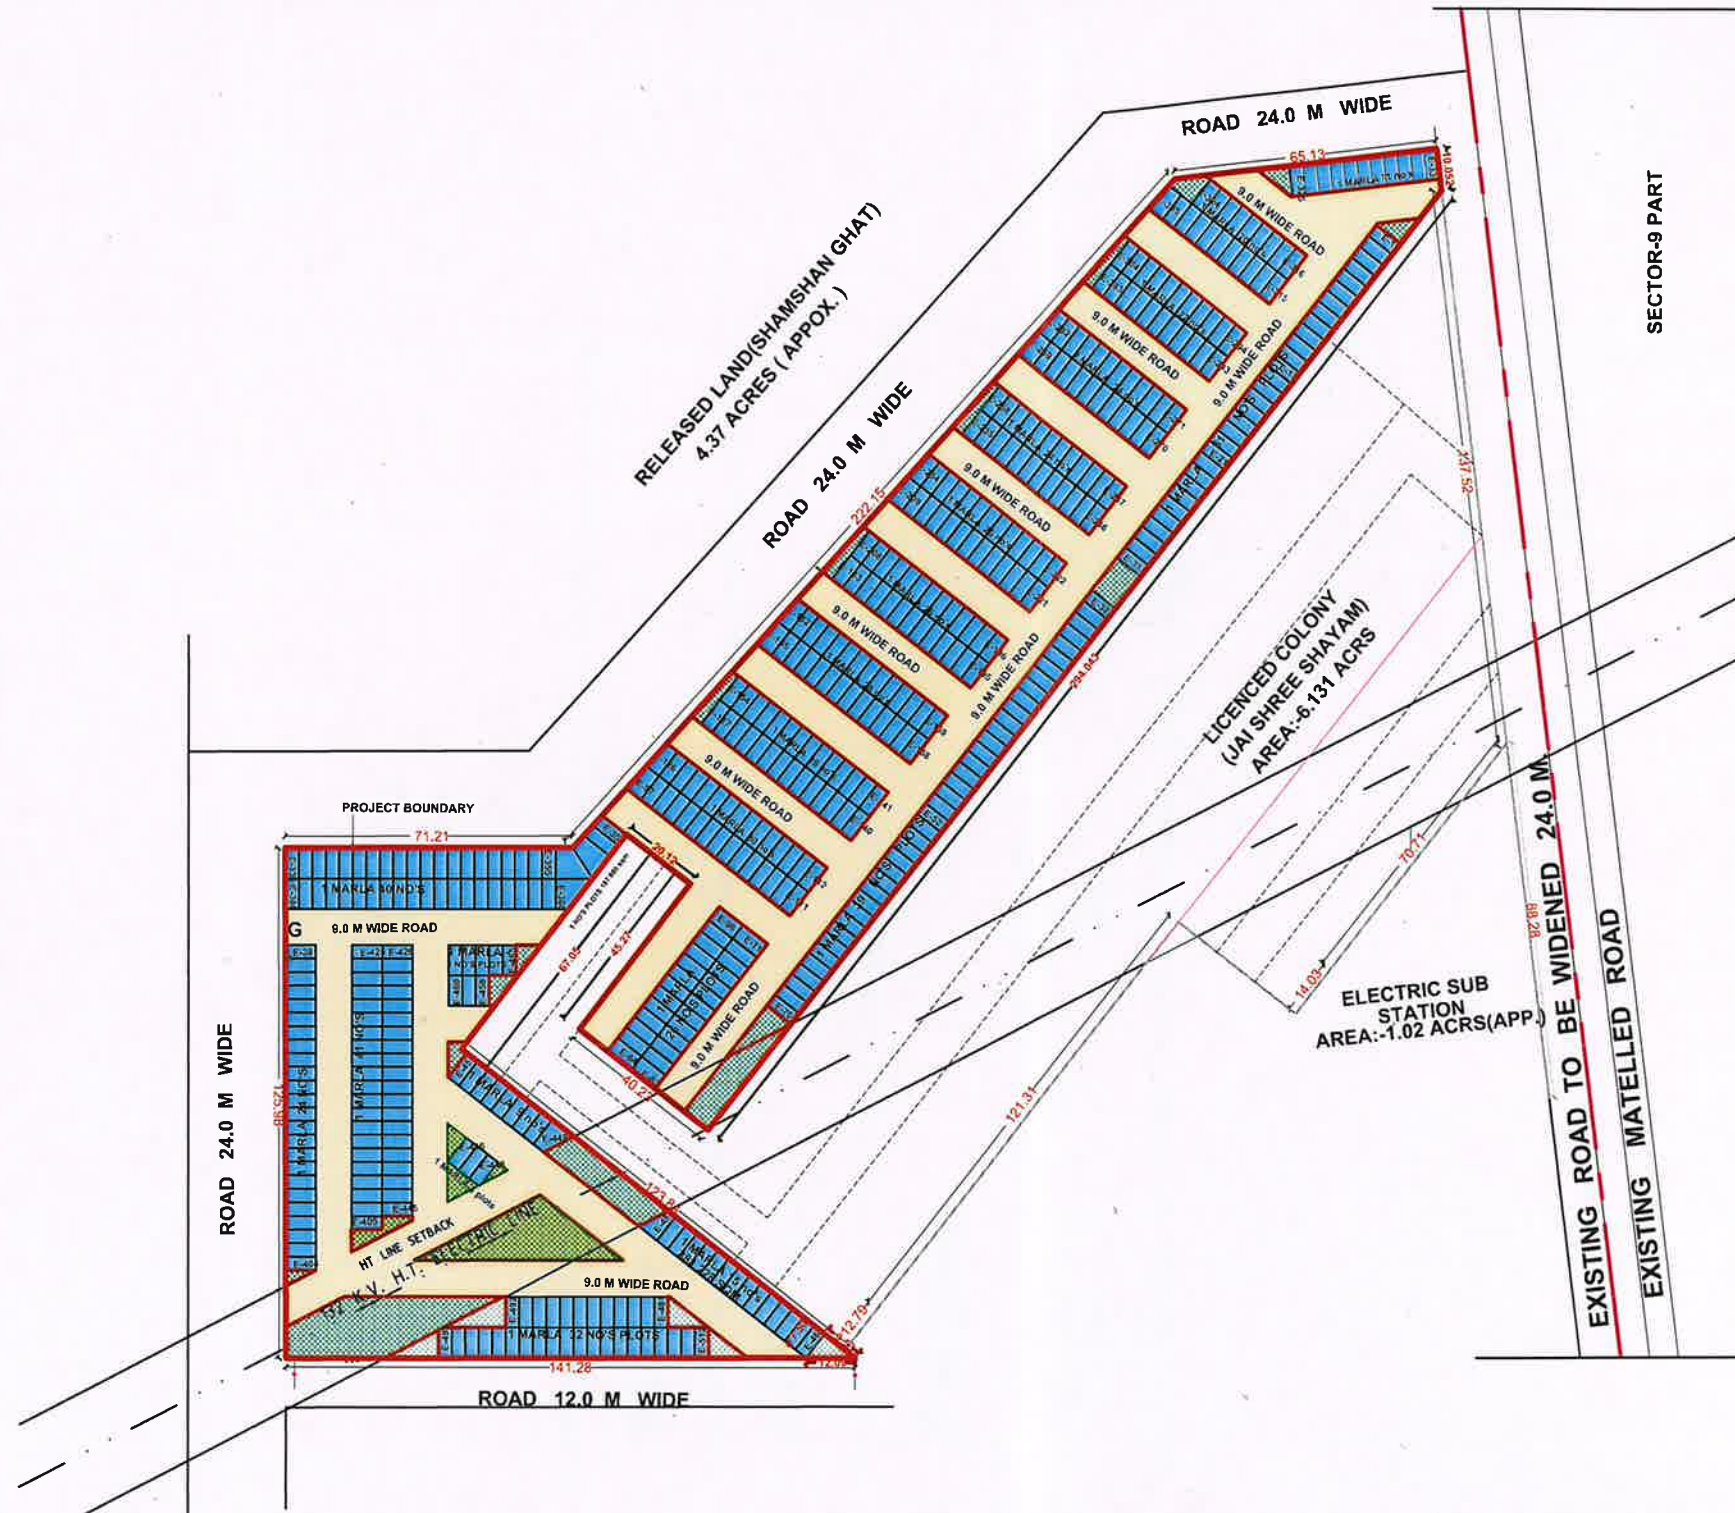

AREA DETAIL

AREA IN ACRES

TOTAL SITE AREA = 26288.865 SQM. (6.50 acre)

AREA UNDER HT LINE = 2620.30 SQM 0.64 ACRES

TOTAL BALANCE AREA = 23717.52 SQM 5.86 ACRES

PERMISSIBLE 60% AREA = 14230.51 SQM 3.51 ACRES

ACHIEVED PLOTTABLE AREA = 13259.485 sqm. 3.27 acre (55.90 %).

ACHIEVED GREEN AREA = 764.799 SQM. 0.189 ACRES (2.90 %).

ACHIEVED GREEN AREA UNDER HT LINE = 1424.731 SQM. 0.35 ACRES (5.409 %).

DETAIL OF PLOTS

PLOT SIZE = 3.350M x 7.50M

CATEGORY = 1 MARLA

TOTAL NO'S PLOTS = 512 NO'S



CHIEF ADMINISTRATOR - sd-

SECRETARY - [Signature]

CHIEF ENGINEER - [Signature]

SENIOR TOWN PLANNER - [Signature]

ARCHITECT - [Signature]

ASSISTANT TOWN PLANNER - [Signature]

HBH

PROPOSAL FOR TENTATIVE LAYOUT PLAN FOR 1 MARLA PLOTS UNDER MUKHYAMANTRI AWAS YOJANA SECTOR-9 DADRI

DEALT BY

SCALE

JOB NO. DATE DRG. NO.