
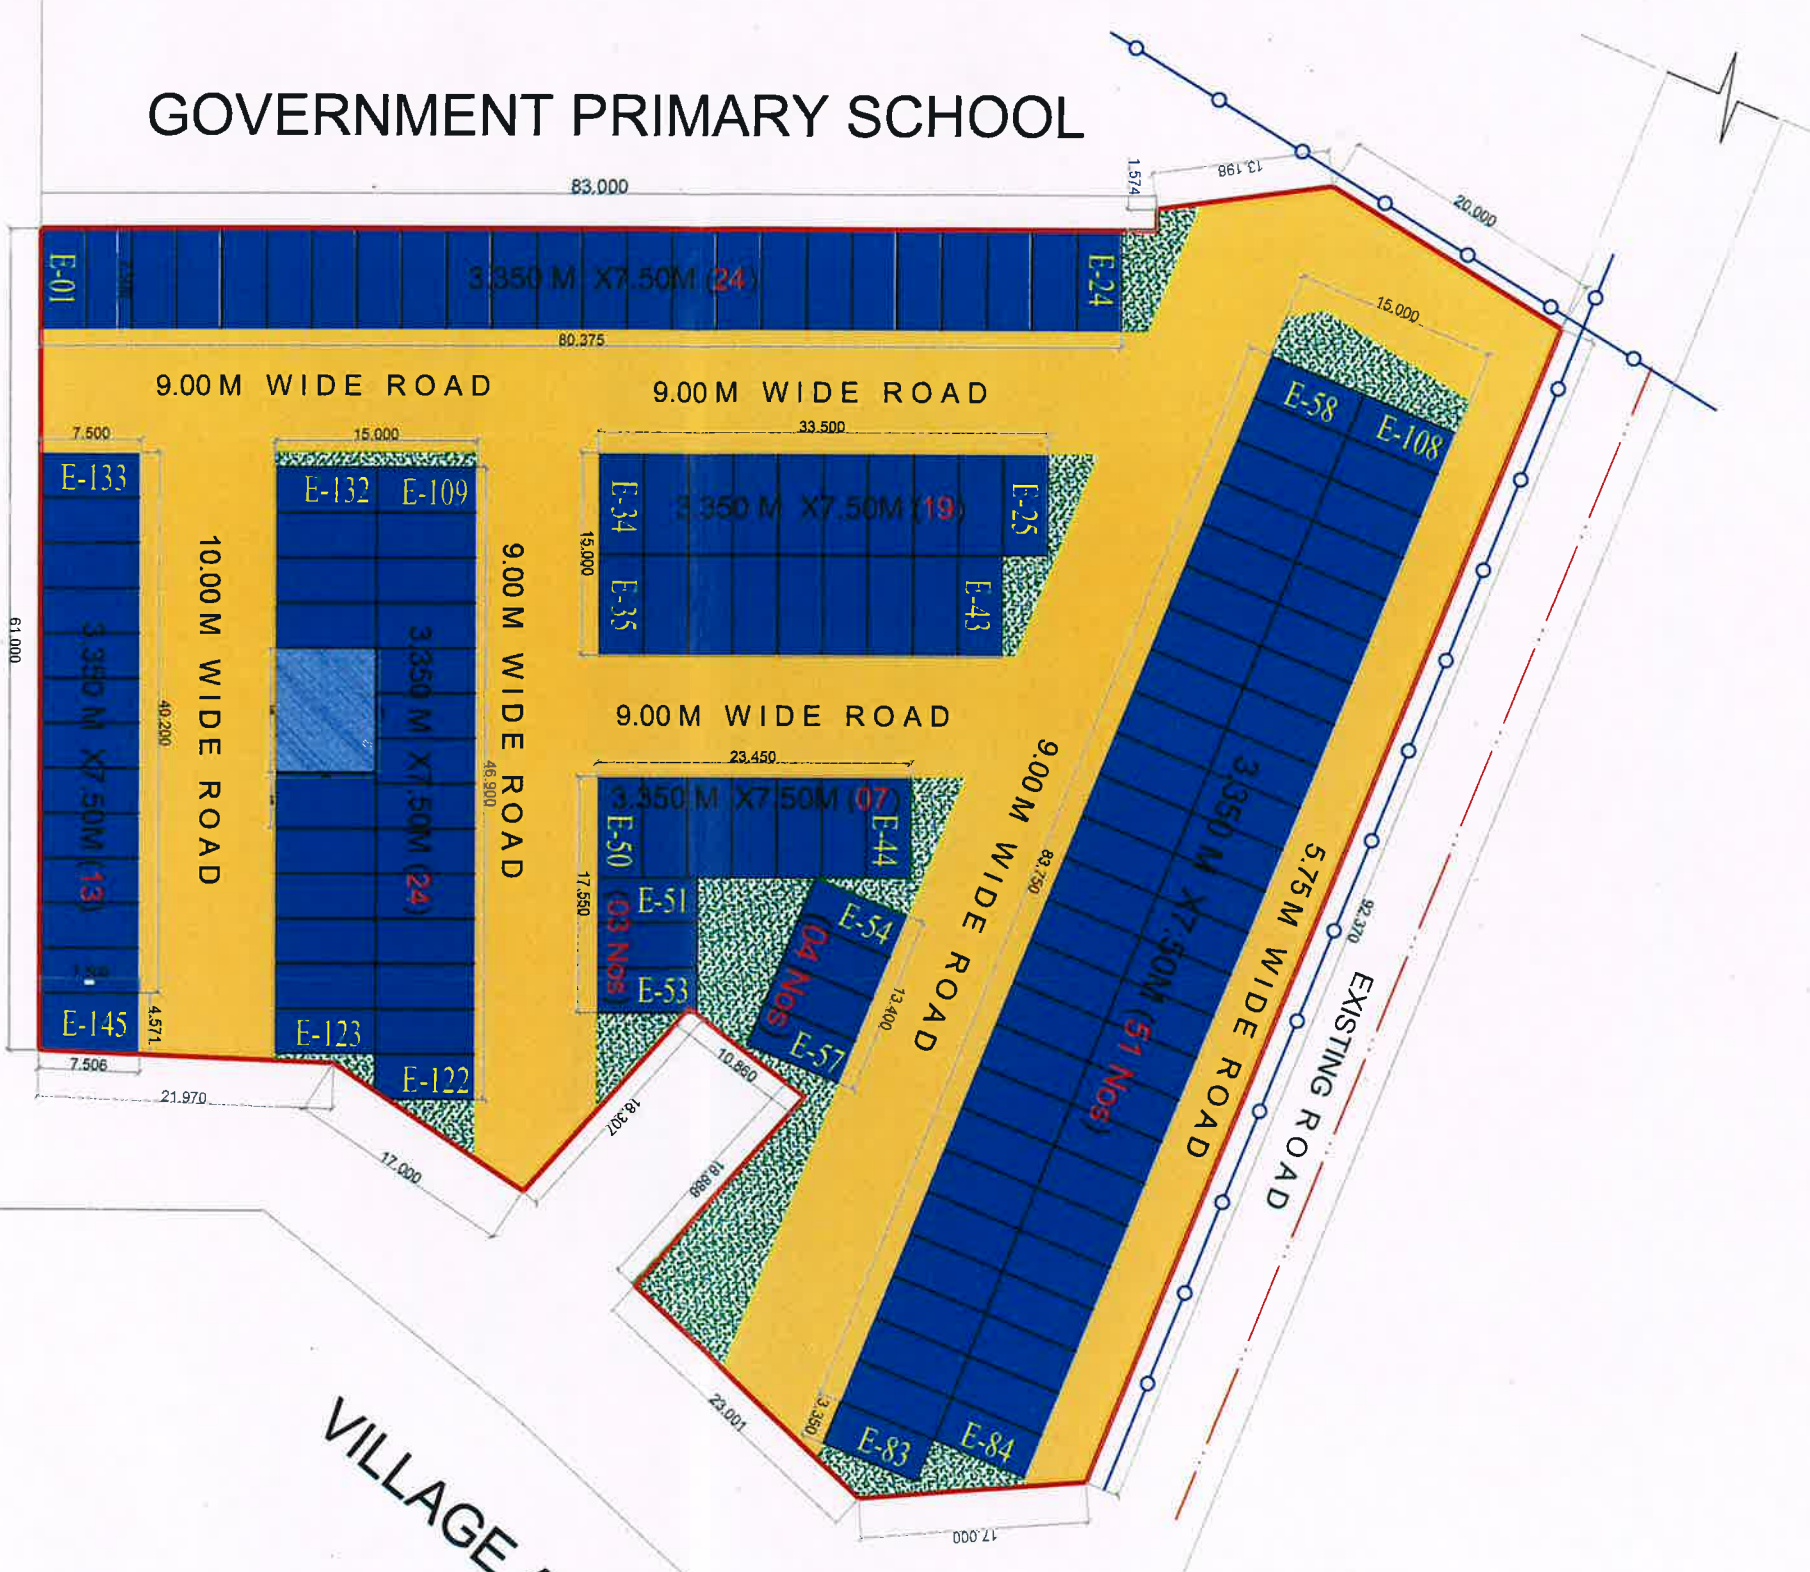


AREA=1.84 ACRES, PLOTS=145 NOS., 1MARLA =30SQ.YDS.

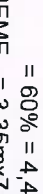

AREA DETAIL TOTAL AREA OF PLOT = 7483.72 SQ.M. OR 1.84 ACRES PERMISSIBLE GROUND COVERAGE = 60% = 4,490.23 SQ. M. AREA ACHIEVED UNDER PLOTTED SCHEME = 3.35mx7.50m=25.125 SQ.M TOTAL AREA ACHIEVED@145 PLOTS = 3,631.60 Sqm@48.52% TOTAL NO OF PLOTS = 145 PLOTS GREEN AREA = 445.46 SQ.M @ 5.95%		HBH <u>PROPOSAL FOR TENTATIVE LAYOUT</u> <u>PLAN FOR 1-MARLA PLOTS UNDER</u> <u>MUKHYAMANTRI AWAS YOJANA</u> <u>IN SECTOR-22, YAMUNANAGAR-</u> <u>JAGADHRI (MC) (SITE-1)</u>	
1. SCHEME BOUNDARY WALL 2. H.T. ELECTRIC POLE LINE 3. VOLT L.T LINE 4. L.T SETBACK LINE 5. PROPOSED 1-MARLA PLAN 6. PROPOSED GREEN AREA		CHIEF ADMINISTRATOR - <i>[Signature]</i> SECRETARY <i>[Signature]</i> CHIEF ENGINEER <i>[Signature]</i> SENIOR TOWN PLANNER <i>[Signature]</i> ARCHITECT <i>[Signature]</i> ASSISTANT TOWN PLANNER <i>[Signature]</i>	Job.no. date : diag.no. 
DEALT BY			