

KARNAL

LAYOUT PLAN OF HOUSING SCHEME UNDER "MUKHYAMANTRI GRAMIN AWAS YOJANA - 2.0" (MMGAY-2.0) AREA MEASURING 16 BIGHA (13489.36 SQM.) COMPRISING IN KHASRA NOS. 750, 753, 754, 760 & 761 IN THE REVENUE ESTATE OF VILLAGE BAROTA, BLOCK-CHIRAO, DISTRICT KARNAL.

DETAILS OF PLOTTED AREA :-

SR.NO.	PARTICULAR	SIZE	NOS.
1.	RESI. PLOT	6.71X12.47 M	86 7195.93 SQM.
2.	MAHILA CHOUPAL	9.97 X 16.87M	1 168.19 SQM.
3.	TUBE WELL	9.97 X 12.56 M	1 125.22 SQM.

TOTAL PLOTTED AREA = 7489.34 SQM.

DETAILS OF AREA :-

AREA OF SCHEME	= 16 BIGHA OR 13489.36 SQM.
PLOTTED AREA	= 7489.34 SQM. (55.52%)
AREA UNDER ROADS / PARKS / OPEN SPACES	= 6000.02 SQM.

LEGEND :-

SCHEME BOUNDARY

HT. LINE

KILLA LINE

VILLAGE BOUNDARY

PARK / OPEN SPACES

NOTE:-

- ALL DIMENSIONS ARE IN METERS.
- THIS LAYOUT PLAN HAS BEEN PREPARED ON THE BASIS OF SAJRA PLAN PROVIDED BY BDPO, CHIRAO.
- THE KHARSA NOS. OF MMGAY-2.0 SCHEME DOES NOT FALL IN ANY CONTROLLED AREA OF DISTRICT KARNAL AND FALLS IN URBAN AREA KARNAL.
- THIS SITE DOES NOT FALL IN NCZ SURVEY REPORT APPROVED BY DLSC AND SENT TO SLC.

SCALE: 1 CM = 5 MTR.

NORTH



DRAWING NO. D.T.P (K) 1760 / 2025 DATED 15.09.2025

DRAWN BY:-

RAJNEESH KUMAR (TRACER)

CHECKED BY:-

DHANI RAM RANGA (JD)

PARDEEP KUMAR (SD)

PLANNING ASSISTANT

(VACANT)


ASSTT. TOWN PLANNER

MOHIT SINGH

DISTT. TOWN PLANNER

GUNJAN VERMA

DEPTT.OF TOWN & COUNTRY PLANNING HARYANA

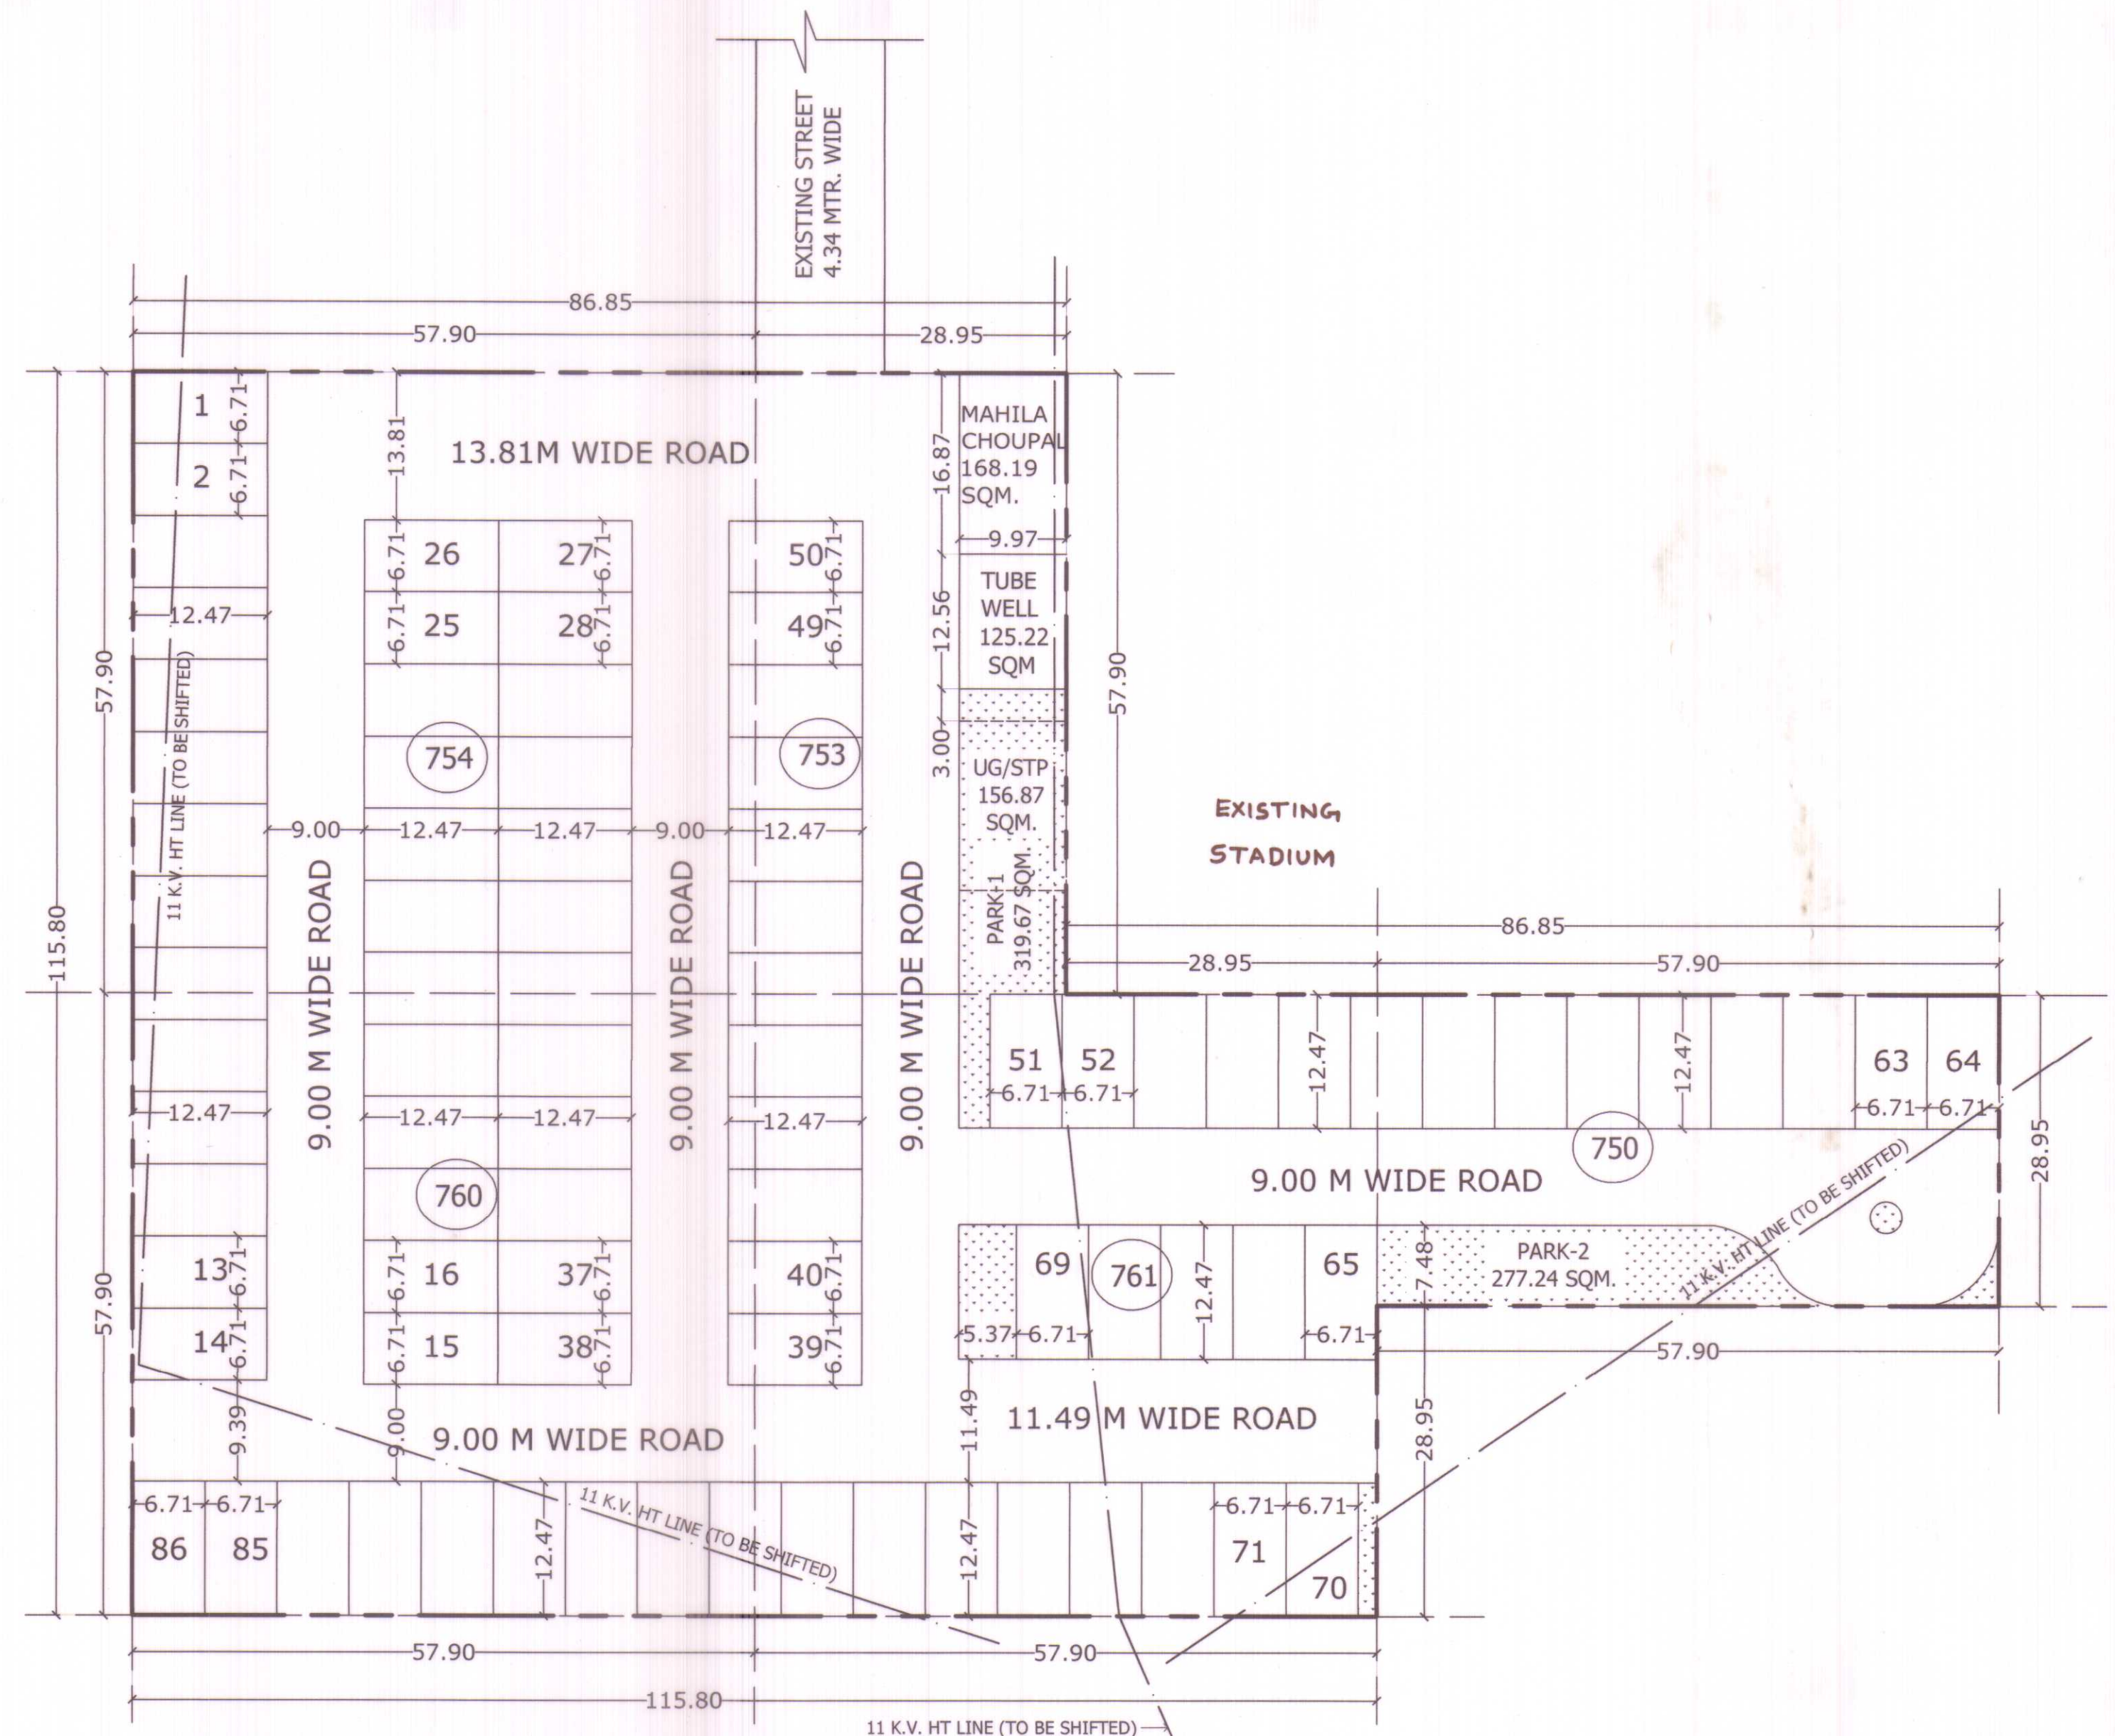

SUB DIVISIONAL OFFICER,
CHIRAO BLOCK, DISTRICT KARNAL
PANCHAYATI RAJ DEPARTMENT,
HARYANA, CHANDIGARH

B.D.P.O., CHIRAO BLOCK,
DISTRICT KARNAL

CHAIRPERSON "MMGAY-2.0" - CUM -
SENIOR TOWN PLANNER, PANCHKULA
TOWN & COUNTRY PLANNING DEPARTMENT,
HARYANA, CHANDIGARH