

LAYOUT CUM DEMARCATION PLAN OF MUKHYA
MANTRI GRAMIN AWAS YOJNA-2.0 IN KHASRA
NOS. 61//14,17,18,23,24 OF VILLAGE RATTA
KHERA IN DISTRICT FATEHABAD

DETAILS OF AREA:-

TOTAL AREA OF SCHEME = 5.00 ACRES

TOTAL AREA OF PLOTS = 2.87 ACRES

AREA OF MAHILA CHOUPAL = 0.04 ACRES


AREA UNDER ROADS/OPEN SPACES = 2.09 ACRES

TOTAL PLOTABLE AREA=11630.64 SQM.(57.49%)

SR.	CATEGORY	SIZE OF PLOTS (IN MTR)	NO OF PLOTS	TOTAL AREA (IN SQM.)
1.	100 SQ. YDS.	6.71 X 12.47 M.	139	11630.64
2.	200 SQ. YDS. MAHILA CHAUPAL	12.47 X 13.42	1	167.35
TOTAL			140	11797.99

NOTE:-

THE PLOTS FALLING UNDER THE ROW OF H.T. LINE PLOTS NOS 1-2,
3-11, 14-16, 19-22, 25-27, 33-36, 46-48, 52-55, 60-62, 66-69
71-80, 83-85, 90, 95-108 & MAHILA CHOPAL MAY NOT BE ALLOTTED
UNTIL THE H.T. LINES GET SHIFTED.

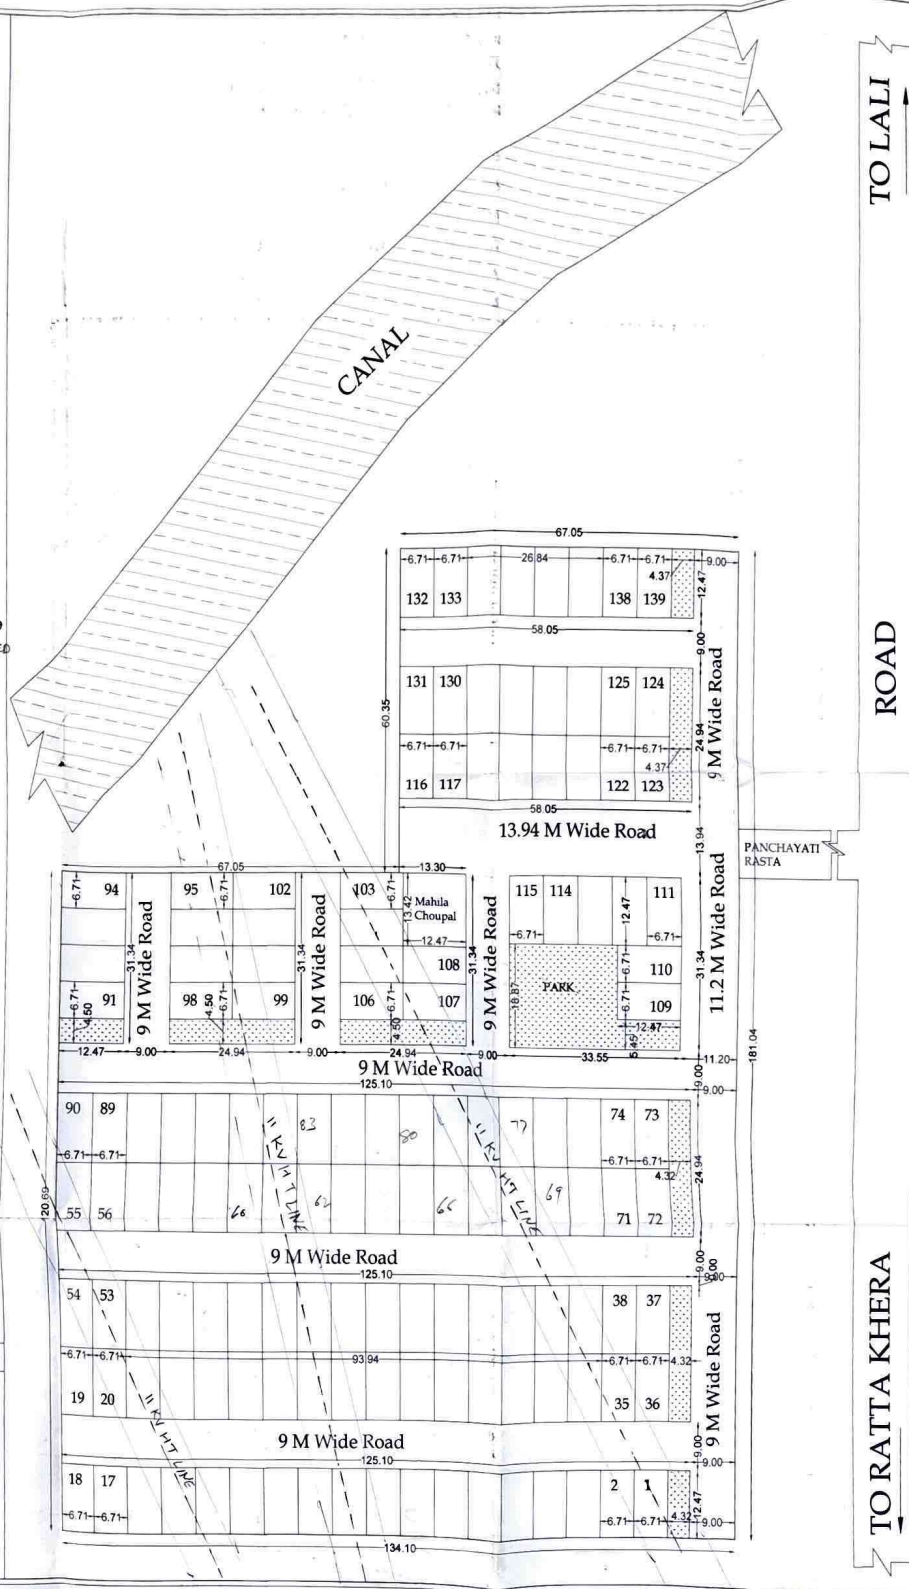

SCALE :- 1cm = 5 m

DRAWING NO. DTP(F)/316/2025

DATED:04.07.2025

DISTRICT TOWN PLANNER,
FATEHABAD

SUB-DIVISION OFFICER,
PANCHAYATI RAJ, FATEHABAD

SENIOR TOWN PLANNER,
HISAR CIRCLE HISAR

BLOCK DEVELOPMENT
& PANCHAYAT OFFICER,
FATEHABAD