

J H A J J A R

LAYOUT CUM DEMARCATION PLAN OF M.M.G.A.Y SITE
IN KILL NO.- 127/6, 15, 16, 17, 25 REVENUE ESTATE
DULHERA, DISTRICT JHAJJAR.

LEGEND -

DETAIL OF AREA	AREA IN ACRES
TOTAL SITE AREA	05.00 ACRE
NET AREA PLANNED	05.00 "
AREA UNDER PLOTS	02.269 "
AREA UNDER MAHILA CHOUPAL	00.043 "
AREA UNDER STP	00.043 "
AREA UNDER COMMUNITY CENTRE	00.550 "
AREA UNDER ROADS & PARKS.	02.095 "

CATEGORY	SIZE OF PLOTS	AREA OF PLOTS	TOTAL PLOT	TOTAL AREA
100 SQY	12.10MX7.30M	88.33 SQM.	104	9186.32 SQM.
				2.269ACRS.

SCHEME BOUNDARY SHOWN THUS




PARK SHOWN THUS



NOTE - 1. THIS DRAWING HAS BEEN PREPARED OF BASIS OF SAZRA
PLAN/OUTER DIMENSION PLAN RECEIVED FROM BLOCK DEVELOPMENT
PANCHAYAT OFFICE JHAJJAR, VIDE MEMO NO-2823 DATED -30-05-2025

SCALE - 1CM=5MTR

(in meters)

 

DRAWING NO. - DTP (JH) 753/2025, DT. 12.06.2025

DRAWN BY

(NARINDER AG)

CHECKED BY

(SANDHEEP KUMAR JI)

Sr. DRAUGHTSMAN

(JUDITHA)

JE

ASSTT. TOWN PLANNER

(SANTOSH KUMAR)

DISTT. TOWN PLANNER

(MADHUSH CHARYA)


SENIOR TOWN PLANNER
ROHTAK

(SANDHEEP KUMAR)

DEPTT. OF T & C, PLANNING HARYANA

SDE

BDPO

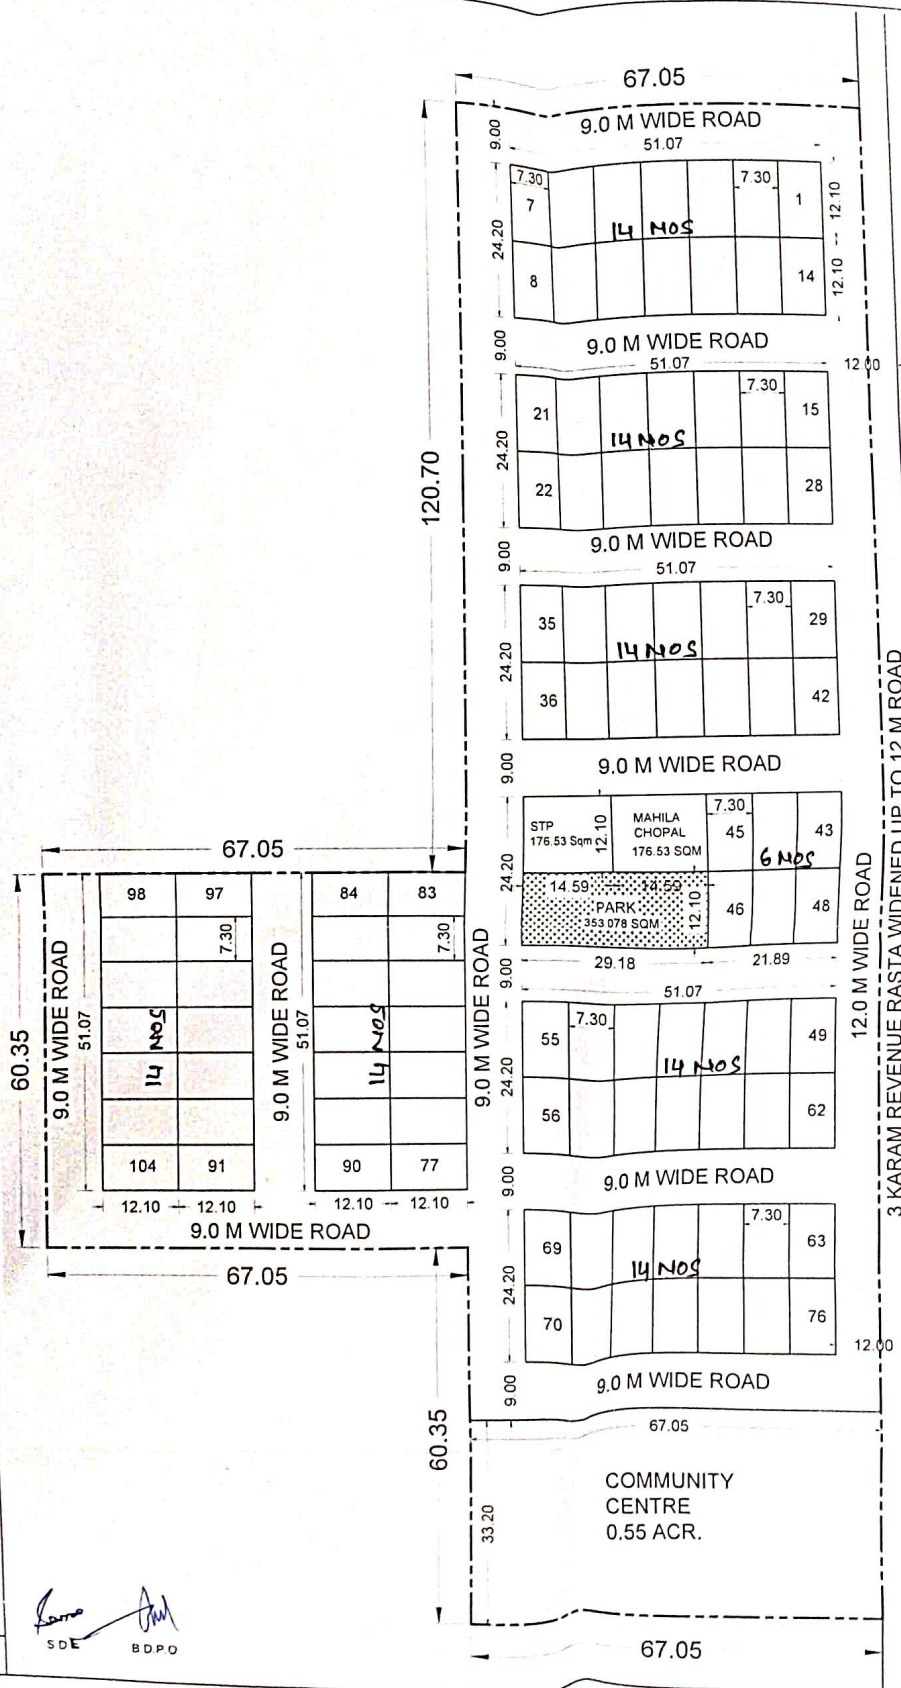

241.40