

KARNAL

LAYOUT PLAN OF HOUSING SCHEME UNDER "MUKHYAMANTRI GRAMIN AWAS YOJANA - 2.0" (MMGAY-2.0) AREA MEASURING 3.50 ACRES, COMPRISING IN KHASRA NOS. 816, 817, 818, 819, 820 IN THE REVENUE ESTATE OF VILLAGE BHUSLI, BLOCK- KARNAL, DISTRICT KARNAL.

DETAILS OF PLOTTED AREA :-

SR.NO.	PARTICULAR	SIZE	NOS.
1.	RESI. PLOT	6.71 X 12.47 M	85 7112.26 SQM.
2.	MAHILA CHOUPAL	AS PER SITE	1 167.96 SQM.
3.	TUBE WELL	AS PER SITE	1 140.23 SQM.

TOTAL PLOTTED AREA = 7420.45 SQM. OR 1.834 ACRES

DETAILS OF AREA :-

AREA OF SCHEME	= 3.50 ACRES
PLOTTED AREA	= 1.834 ACRES (52.40%)
AREA UNDER ROADS / PARKS / OPEN SPACES	= 1.666 ACRES

LEGEND :-

SCHEME BOUNDARY	
HT. LINE	
KILLA LINE	
VILLAGE BOUNDARY	
PARK / OPEN SPACES	

NOTE:-

- ALL DIMENSIONS ARE IN METERS.
- THIS LAYOUT PLAN HAS BEEN PREPARED ON THE BASIS OF SAJRA PLAN PROVIDED BY BDPO, KARNAL.
- THE KHASRA NOS. OF MMGAY-2.0 SCHEME FALLS OUTSIDE ANY CONTROLLED AREA DECLARED IN DISTRICT KARNAL WHEREAS, THESE KH. NO. FALLS WITHIN URBAN AREA KARNAL.
- THIS SITE DOES NOT FALL IN NCZ SURVEY REPORT APPROVED BY DLSC AND SENT TO SLC.

SCALE: 1 CM = 5 MTR.

NORTH



DRAWING NO. D.T.P (K) 1773 / 2025 DATED 29.12.2025

DRAWN BY:-

RAJNEESH KUMAR (TRACER)

CHECKED BY:-

DHANI RAM RANGA (JD)

PLANNING ASSISTANT

(VACANT)


ASSTT. TOWN PLANNER

MOHIT SINGH

DISTT. TOWN PLANNER

GUNJAN VERMA

DEPTT.OF TOWN & COUNTRY PLANNING HARYANA

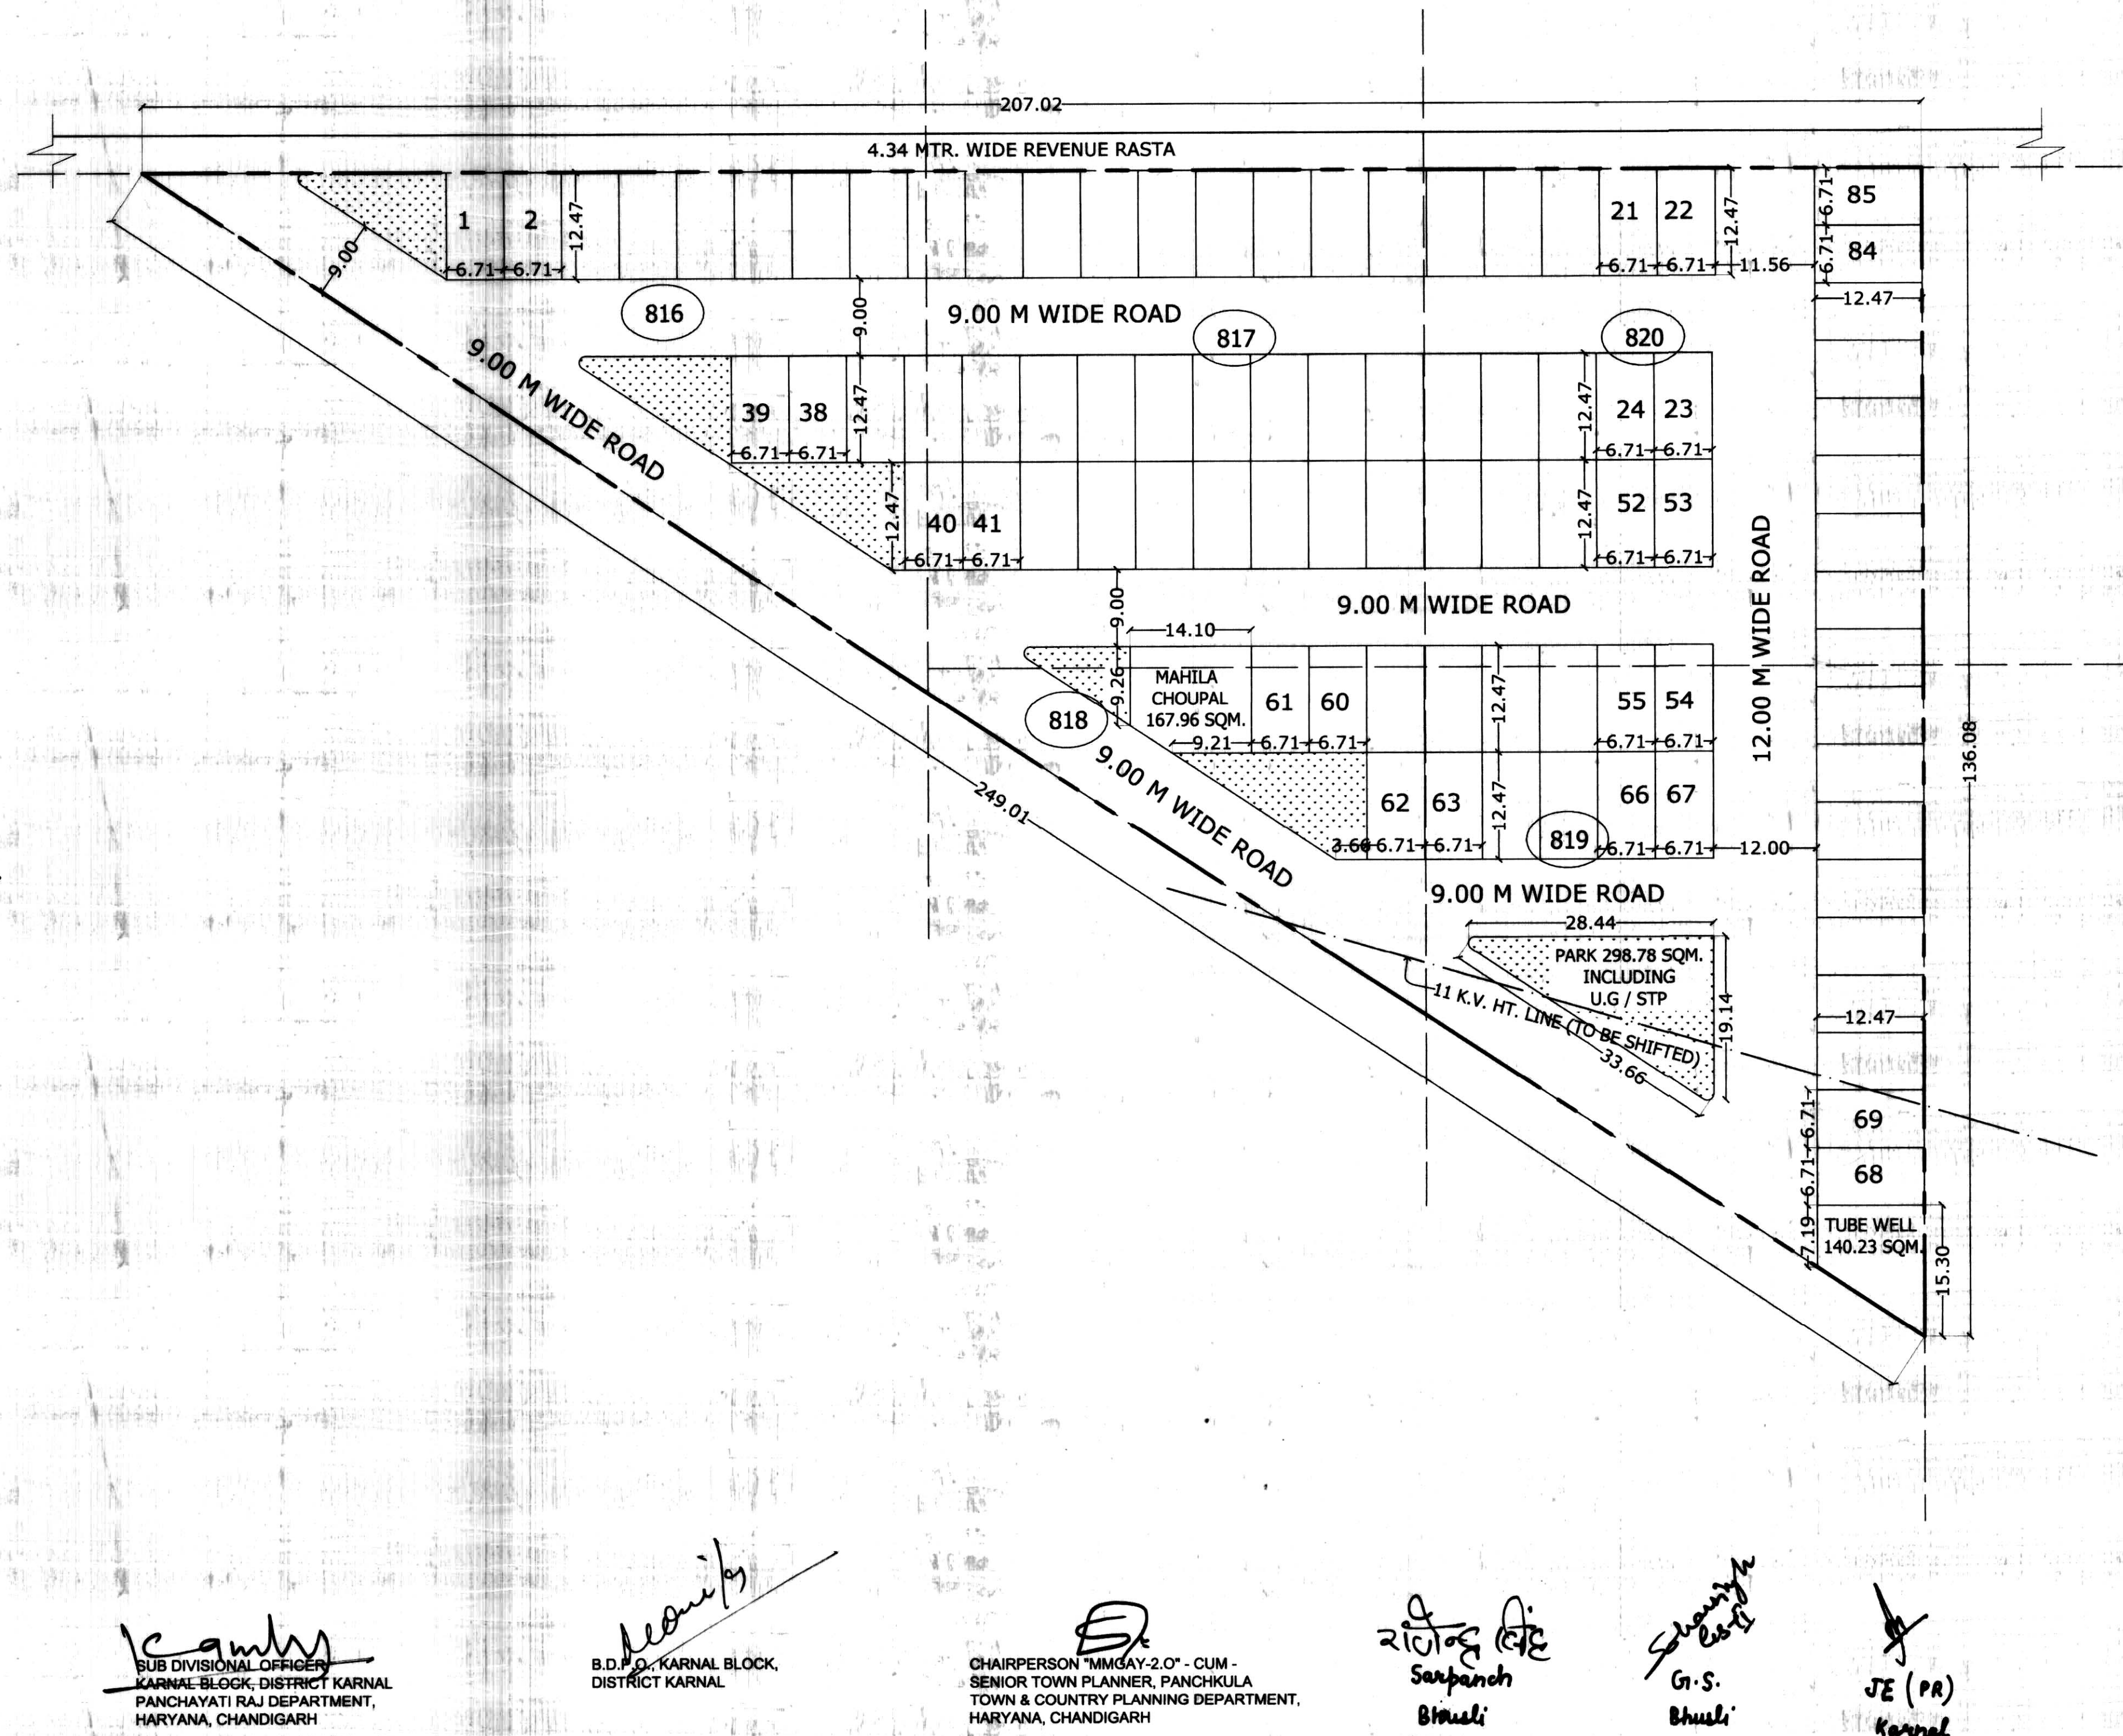

SUB DIVISIONAL OFFICER
KARNAL BLOCK, DISTRICT KARNAL
PANCHAYATI RAJ DEPARTMENT,
HARYANA, CHANDIGARH

B.D.P.O., KARNAL BLOCK,
DISTRICT KARNAL

CHAIRPERSON "MMGAY-2.0" - CUM -
SENIOR TOWN PLANNER, PANCHKULA
TOWN & COUNTRY PLANNING DEPARTMENT,
HARYANA, CHANDIGARH

Sarpanch
Bhushi
Gram Panchayat
Vill-Bhusli, Distt. Karnal

G.S.
Bhushi

JE (PR)
Karnal