

KARNAL

LAYOUT PLAN OF HOUSING SCHEME UNDER "MUKHYAMANTRI GRAMIN AWAS YOJANA - 2.0" (MMGAY-2.0) AREA MEASURING 3.07 ACRES, COMPRISING IN KHASRA NOS. 6/21 MIN. 22 MIN. 11/21, 9/2, 12/1, & 19/2 IN THE REVENUE ESTATE OF VILLAGE DADUPUR, BLOCK-NILOKHERI, DISTRICT KARNAL.

DETAILS OF PLOTTED AREA :-		
S.R.NO.	PARTICULAR	SIZE
1.	RESI. PLOT	6.71 X 12.47 M
2.	MAHILA CHOUPAL	13.23 X 12.47 M
3.	TUBE WELL	AS PER SITE

TOTAL PLOTTED AREA = 5122.6 SQM OR 1.39 ACRES

AREA OF SCHEME = 3.07 ACRES
PLOTTED AREA = 1.39 ACRES (45.28%)
AREA UNDER ROADS / PARKS / OPEN SPACES = 1.68 ACRES

LEGEND :-	
SCHEME BOUNDARY	=====
HT. LINE	-----
KILLA LINE	-----
VILLAGE BOUNDARY	-----
PARK / OPEN SPACES	

- NOTE:-
1. ALL DIMENSIONS ARE IN METERS.
 2. THIS LAYOUT PLAN HAS BEEN PREPARED ON THE BASIS OF SAIRA PLAN PROVIDED BY BPO, NILOKHERI AND SITE PLAN PROVIDED BY PANCHAYAT SECRETARY OF GRAM PANCHAYAT DADUPUR.
 3. THE KHASRA NOS. OF MMGAY-2.0 SCHEME FALLS OUTSIDE CONTROLLED AREA AND URBAN AREA OF DISTRICT KARNAL.
 4. THIS SITE DOES NOT FALL IN NCZ SURVEY REPORT APPROVED BY DLSC AND SENT TO S.L.C.

SCALE: 1 CM = 5 MTR NORTH

DRAWING NO. D.T.P. (K) 1756 / 2025 DATED 13.08.2025

DRAWN BY:- RAJNESH KUMAR (TRACER)


CHECKED BY:- DHANI RAM RANGA (JD) PARDEEP KUMAR (SD)

PLANNING ASSISTANT (VACANT) RAMESH KUMAR (SD) ANKUR, E.I.

ASSTT. TOWN PLANNER MOHIT SINGH

DISTT. TOWN PLANNER GUNJAN VERMA

DEPTT. OF TOWN & COUNTRY PLANNING HARYANA

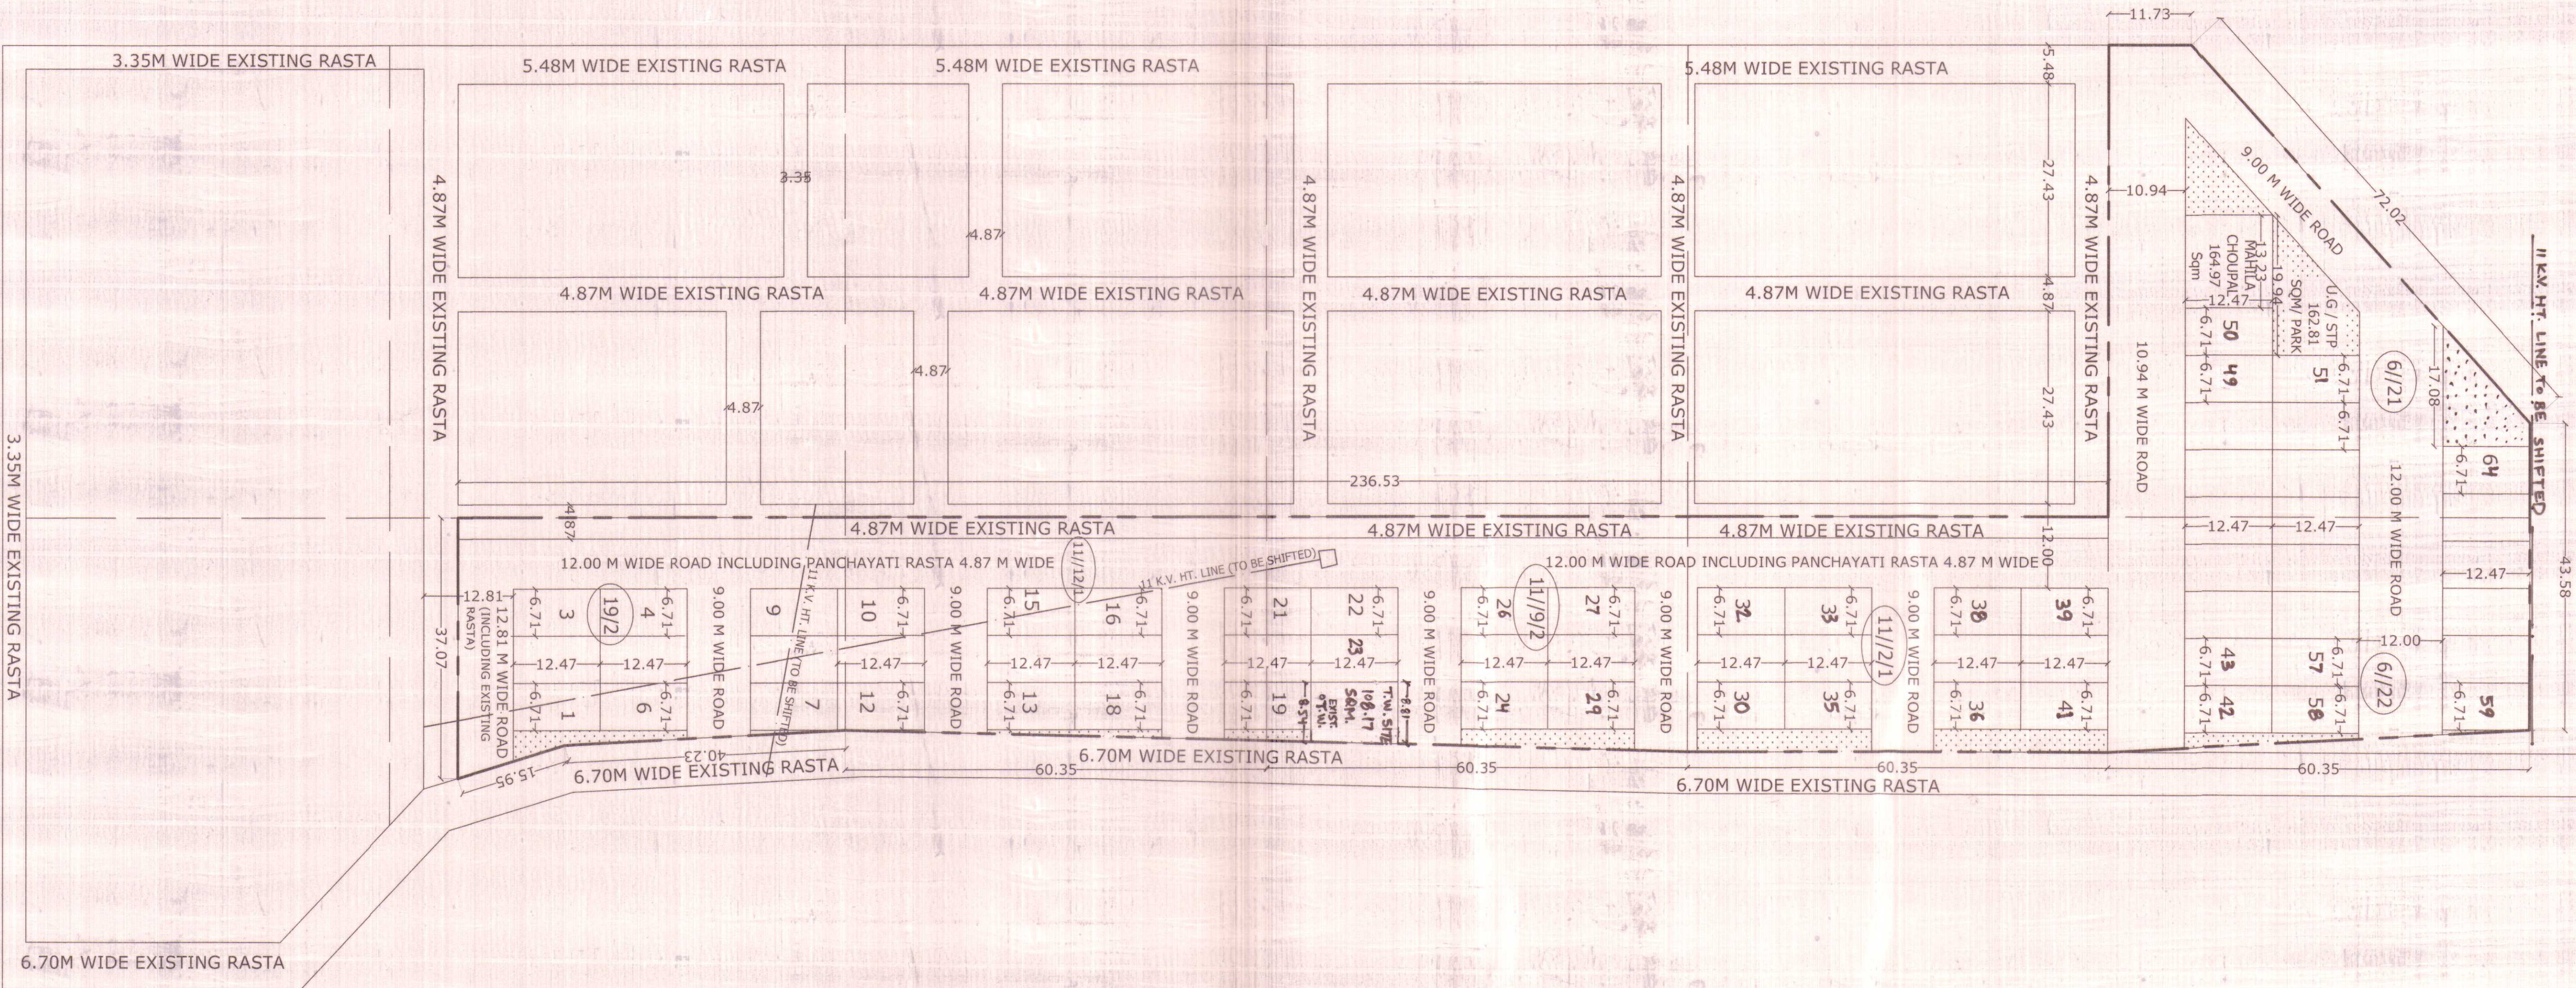

SUB DIVISIONAL OFFICER, NILOKHERI BLOCK, DISTRICT KARNAL, PANCHAYATI RAJ DEPARTMENT, HARYANA, CHANDIGARH

B.D.P.O., NILOKHERI BLOCK, DISTRICT KARNAL

CHAIRPERSON MMGAY-2.0 - CUM - SENIOR TOWN PLANNER, PANCHAYATI TOWN & COUNTRY PLANNING DEPARTMENT, HARYANA, CHANDIGARH