


KARNAL

LAYOUT PLAN OF HOUSING SCHEME UNDER "MUKHYAMANTRI GRAMIN AWAS YOJANA - 2.0" (MMGAY-2.0) AREA MEASURING 3.81 ACRES, COMPRISING IN KHASRA NOS. 8/16, 7, 8, 13, 14 & 15 IN THE REVENUE ESTATE OF VILLAGE GARHI SADAN, BLOCK-INDRI, DISTRICT KARNAL.

DETAILS OF PLOTTED AREA :-			
S.R.NO.	PARTICULAR	SIZE	NOS. AREA
1.	RESI. PLOT	6.71X12.47 M	100 8387.37 SQM.
2.	MAHILA CHOUPAL	13.42X12.47 M	1 167.34 SQM.
3.	TUBE WELL	8.25X12.47 M	1 102.87 SQM.
TOTAL PLOTTED AREA		= 8637.58 SQM. OR 2.134 ACRES	
DETAILS OF AREA :-			
AREA OF SCHEME		= 3.81 ACRES	
PLOTTED AREA		= 2.134 ACRES (56.01%)	
AREA UNDER ROADS / PARKS / OPEN SPACES		= 1.676 ACRES	
LEGEND :-			
SCHEME BOUNDARY			
HT. LINE			
KILLA LINE			
VILLAGE BOUNDARY			
PARK / OPEN SPACES			
NOTE:-			
1. ALL DIMENSIONS ARE IN METERS.			
2. THIS LAYOUT PLAN HAS BEEN PREPARED ON THE BASIS OF			
3. SAIPA PLAN PROVIDED BY BOPO, MDR.			
3. THE KHASRA NOS. OF MMGAY-2.0 SCHEME FALLS IN			
URBAN AREA (MDR)			
4. THE KHASRA NOS. OF MMGAY-2.0 SCHEME FALLS OUTSIDE			
CONTROLLED AREA OF DISTRICT CARNAL			
5. THIS SITE DOES NOT FALL IN NCZ SURVEY REPORT			
APPROVED BY DLSC AND SENT TO SLC.			
SCALE: 1 CM = 5 MTR.		NORTH	
DRAWING NO. D.T.P. (K) 1727 / 2025 DATED:- 10.07.2025			
DRAWN BY:-		RAJNEESH KUMAR (TRACER)	
CHECKED BY:-		DHANI RAM RANGA (JD) PARDEEP KUMAR (SD)	
PLANNING ASSISTANT		RAMESH KUMAR (SD) ROHIT J.E.	
ASSTT. TOWN PLANNER		MOHIT SINGH JOGINDER SINGH, PATWARI	
DISTT. TOWN PLANNER		SATISH KUMAR	
DEPTT. OF TOWN & COUNTRY PLANNING HARYANA			

VILLAGE BOUNDARY

SCHEME BOUNDARY

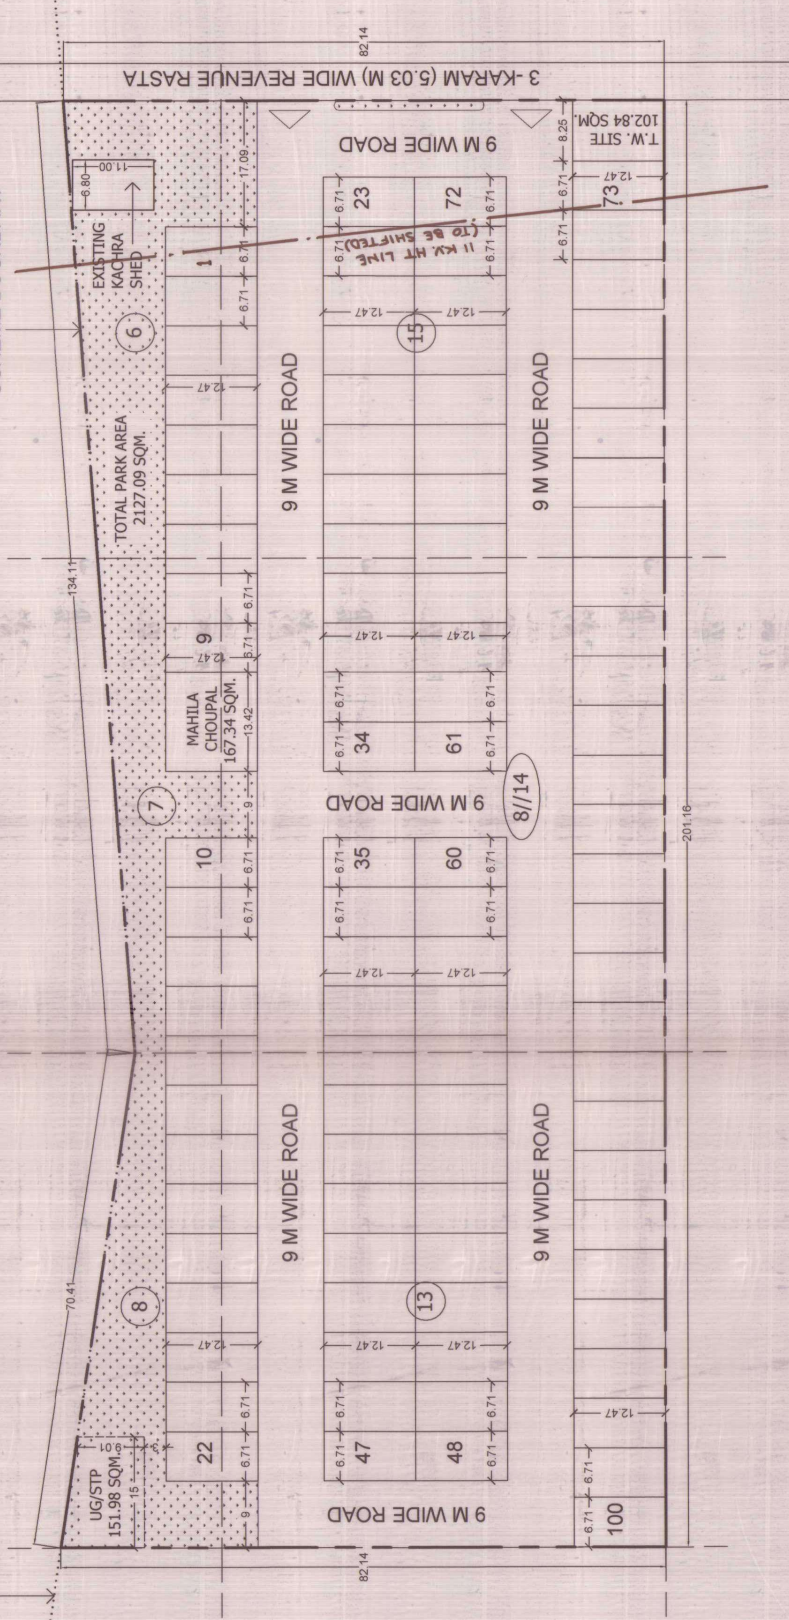

CHAMPDEVI MAHESHWARI, C.O. CLM,
SENIOR TOWN PLANNER, PANCHKULA
TOWN & COUNTRY PLANNING DEPARTMENT,
HARYANA, CHANDIGARH

S.D. CHANDI BLOCK,
DISTRICT KARNAL

SUB DIVISIONAL OFFICER,
PANCHKULA BLOCK, DISTRICT KARNAL,
PANCHAYATI RAJ DEPARTMENT,
HARYANA, CHANDIGARH