

KARNAL

**LAYOUT PLAN OF HOUSING SCHEME UNDER
"MUKHYAMANTRI GRAMIN AWAS YOJANA - 2.0"
(MMGAY-2.0) AREA MEASURING 3.00 ACRES,
COMPRISING IN KHASRA NOS. 54//4, 5, 6 IN THE
REVENUE ESTATE OF VILLAGE MOHIDINPUR,
BLOCK-KARNAL, DISTRICT KARNAL.**

DETAILS OF PLOTTED AREA :-

SR.NO.	PARTICULAR	SIZE	NOS.	AREA
1.	RESI. PLOT	6.71X12.47 M	79	6610.22 SQM.
2.	MAHILA CHOUPAL	8.64 X19.50 M	1	168.48 SQM.
3.	TUBE WELL	8.64X 14.50 M	1	125.28 SQM.
TOTAL PLOTTED AREA		= 6903.98 SQM. OR 1.706 ACRES		

DETAILS OF AREA :-

AREA OF SCHEME	= 3.00 ACRES
PLOTTED AREA	= 1.706 ACRES (56.87%)
AREA UNDER ROADS / PARKS / OPEN SPACES	= 1.294 ACRES

LEGEND :-

SCHEME BOUNDARY	
KILLA LINE	
VILLAGE BOUNDARY	
PARK / OPEN SPACES	

NOTE:-

1. ALL DIMENSIONS ARE IN METERS.
2. THIS LAYOUT PLAN HAS BEEN PREPARED ON THE BASIS OF SHAJRA PLAN PROVIDED BY BDPO, KARNAL.
3. THE KHASRA Nos. OF MMGAY-2.0 SCHEME FALLS WITHIN DECLARED CONTROLLED AREA -VI, KARNAL (IN ABEYANCE) AND WITHIN URBAN AREA KARNAL.
4. THIS SITE DOES NOT FALL IN NCZ SURVEY REPORT APPROVED BY DLSC AND SENT TO SLC.

SCALE: 1 CM = 5 MTR.

NORTH



DRAWING NO. D.T.P (K) 1783 / 2026 DATED 30.01.2026

DRAWN BY:-

RAJNEESH KUMAR (TRACER)

CHECKED BY:-

DHANI RAM RANGA (JD)

PLANNING ASSISTANT

(VACANT)


ASSTT. TOWN PLANNER

MOHIT SINGH

DISTT. TOWN PLANNER

GUNJAN VERMA

DEPTT.OF TOWN & COUNTRY PLANNING HARYANA

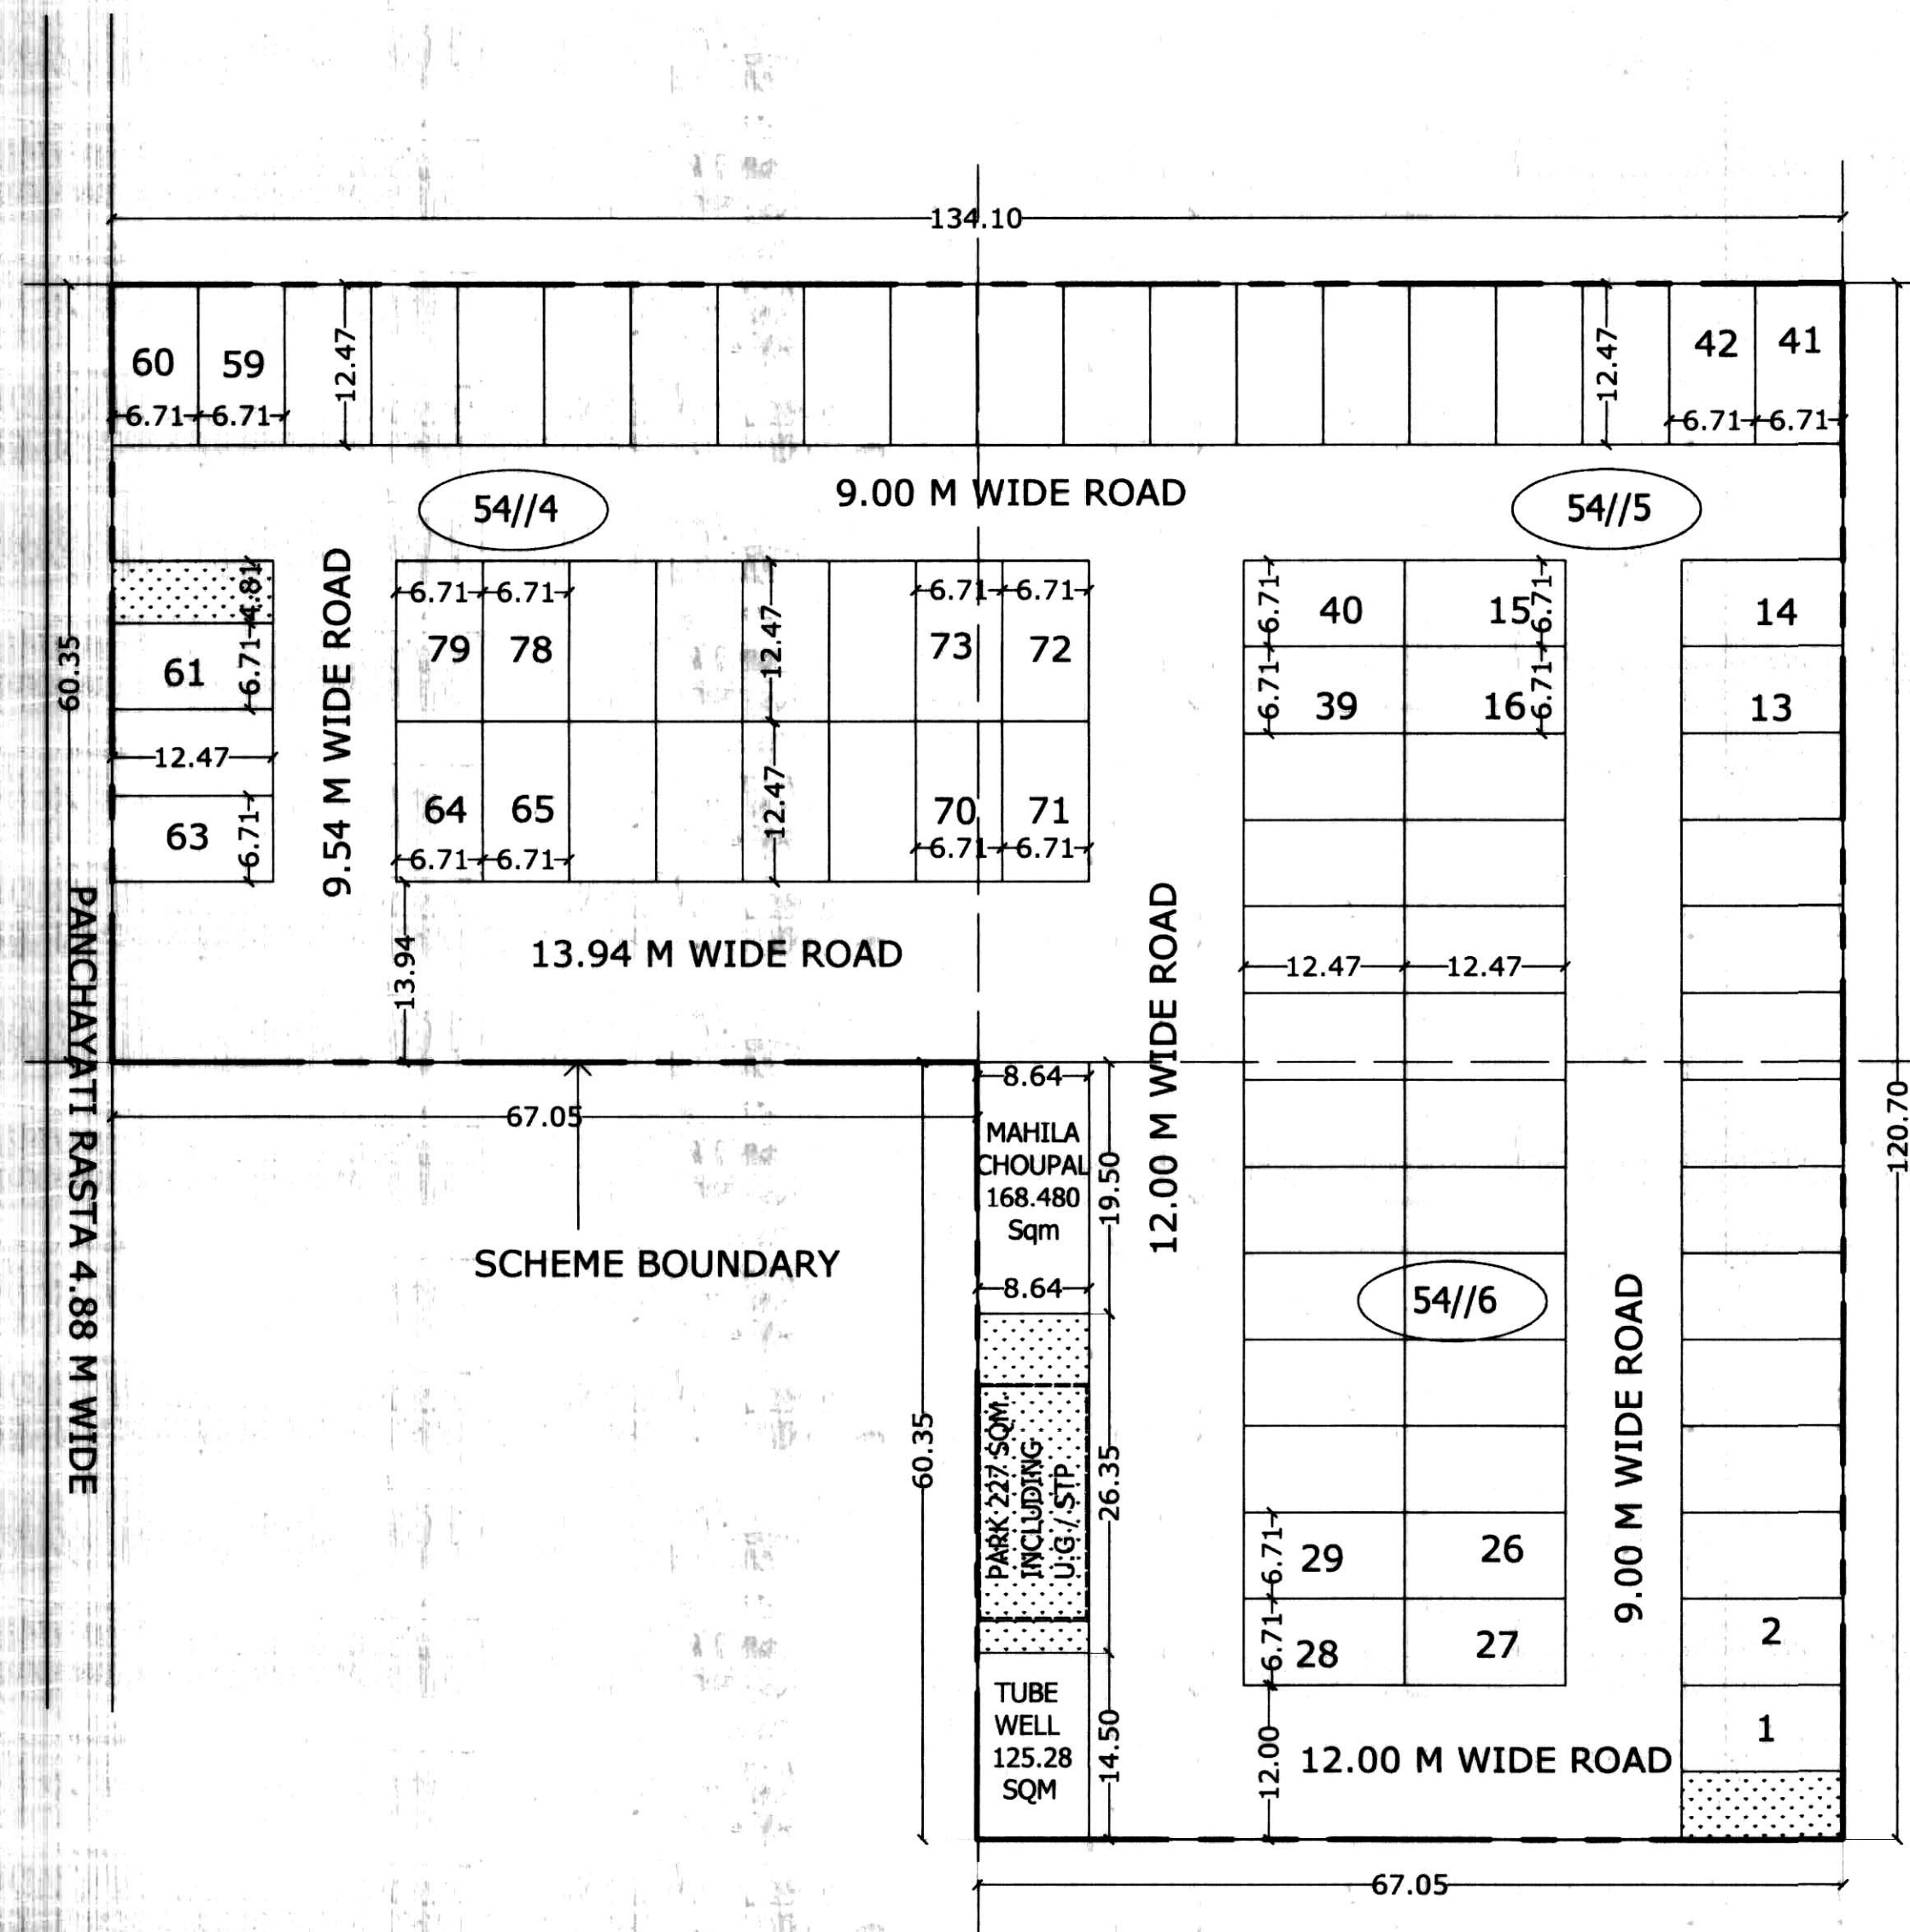

SUB-DIVISIONAL OFFICER
KARNAL BLOCK, DISTRICT KARNAL
PANCHAYATI RAJ DEPARTMENT,
HARYANA, CHANDIDGARH

B.D.P.O., KARNAL BLOCK
DISTRICT KARNAL

CHAIRPERSON "MMGAY-2.0" - CUM -
SENIOR TOWN PLANNER, PANCHKULA
TOWN & COUNTRY PLANNING DEPARTMENT,
HARYANA, CHANDIGARH