

KARNAL

LAYOUT PLAN OF HOUSING SCHEME UNDER "MUKHYAMANTRI GRAMIN AWAS YOJANA - 2.0" (MMGAY-2.0) AREA MEASURING 10.00 ACRES, COMPRISING IN KHASRA NOS. 9// 11, 12, 13, 18, 19, 20 21, 22, 23 & 24 IN THE REVENUE ESTATE OF VILLAGE PABANA HASANPUR, BLOCK-MUNAK, DISTRICT KARNAL.

DETAILS OF PLOTTED AREA :-

SR.NO.	PARTICULAR	SIZE	NOS.	AREA
1.	RESI. PLOT	6.71X12.47 M	263	22006.183 SQM.
2.	MAHILA CHOUPAL	8.94 X19.00 M	1	169.86 SQM.
3.	TUBE WELL	6.57 X19.00 M	1	124.83 SQM.
4.	COMMUNITY CENTER	35.55X 58.88 M	1	2093.184 SQM.
TOTAL PLOTTED AREA				= 24394.057 SQM. OR 6.02 ACRES

DETAILS OF AREA :-

AREA OF SCHEME	= 10.00 ACRES
PLOTTED AREA	= 6.02 ACRES (60.20%)
AREA UNDER ROADS / PARKS / OPEN SPACES	= 3.98 ACRES

LEGEND :-

SCHEME BOUNDARY	---
HT. LINE	---
KILLA LINE	---
VILLAGE BOUNDARY	---
PARK / OPEN SPACES	---

NOTE:-

- ALL DIMENSIONS ARE IN METERS.
- THIS LAYOUT PLAN HAS BEEN PREPARED ON THE BASIS OF SAJRA PLAN PROVIDED BY BDO, MUNAK.
- THE KHARSA NOS. OF MMGAY-2.0 SCHEME FALLS OUTSIDE CONTROLLED AREA AND URBAN AREA OF DISTRICT KARNAL.
- THIS SITE DOES NOT FALL IN NCZ SURVEY REPORT APPROVED BY DLSC AND SENT TO SLC.

SCALE: 1 CM = 5 MTR. NORTH

DRAWING NO. D.T.P. (K) 1746 / 2025 DATED:- 25.07.2025

DRAWN BY:- RAJNEESH KUMAR (TRACER)


CHECKED BY:- DHANI RAM RANGA (JD) PARDEEP KUMAR (SD)

PLANNING ASSISTANT (VACANT) RAMESH KUMAR (SD) ANIL KUMAR (FD)

ASSTT. TOWN PLANNER MOHIT SINGH

DISTT. TOWN PLANNER GUNJAN VERMA

DEPTT.OF TOWN & COUNTRY PLANNING HARYANA

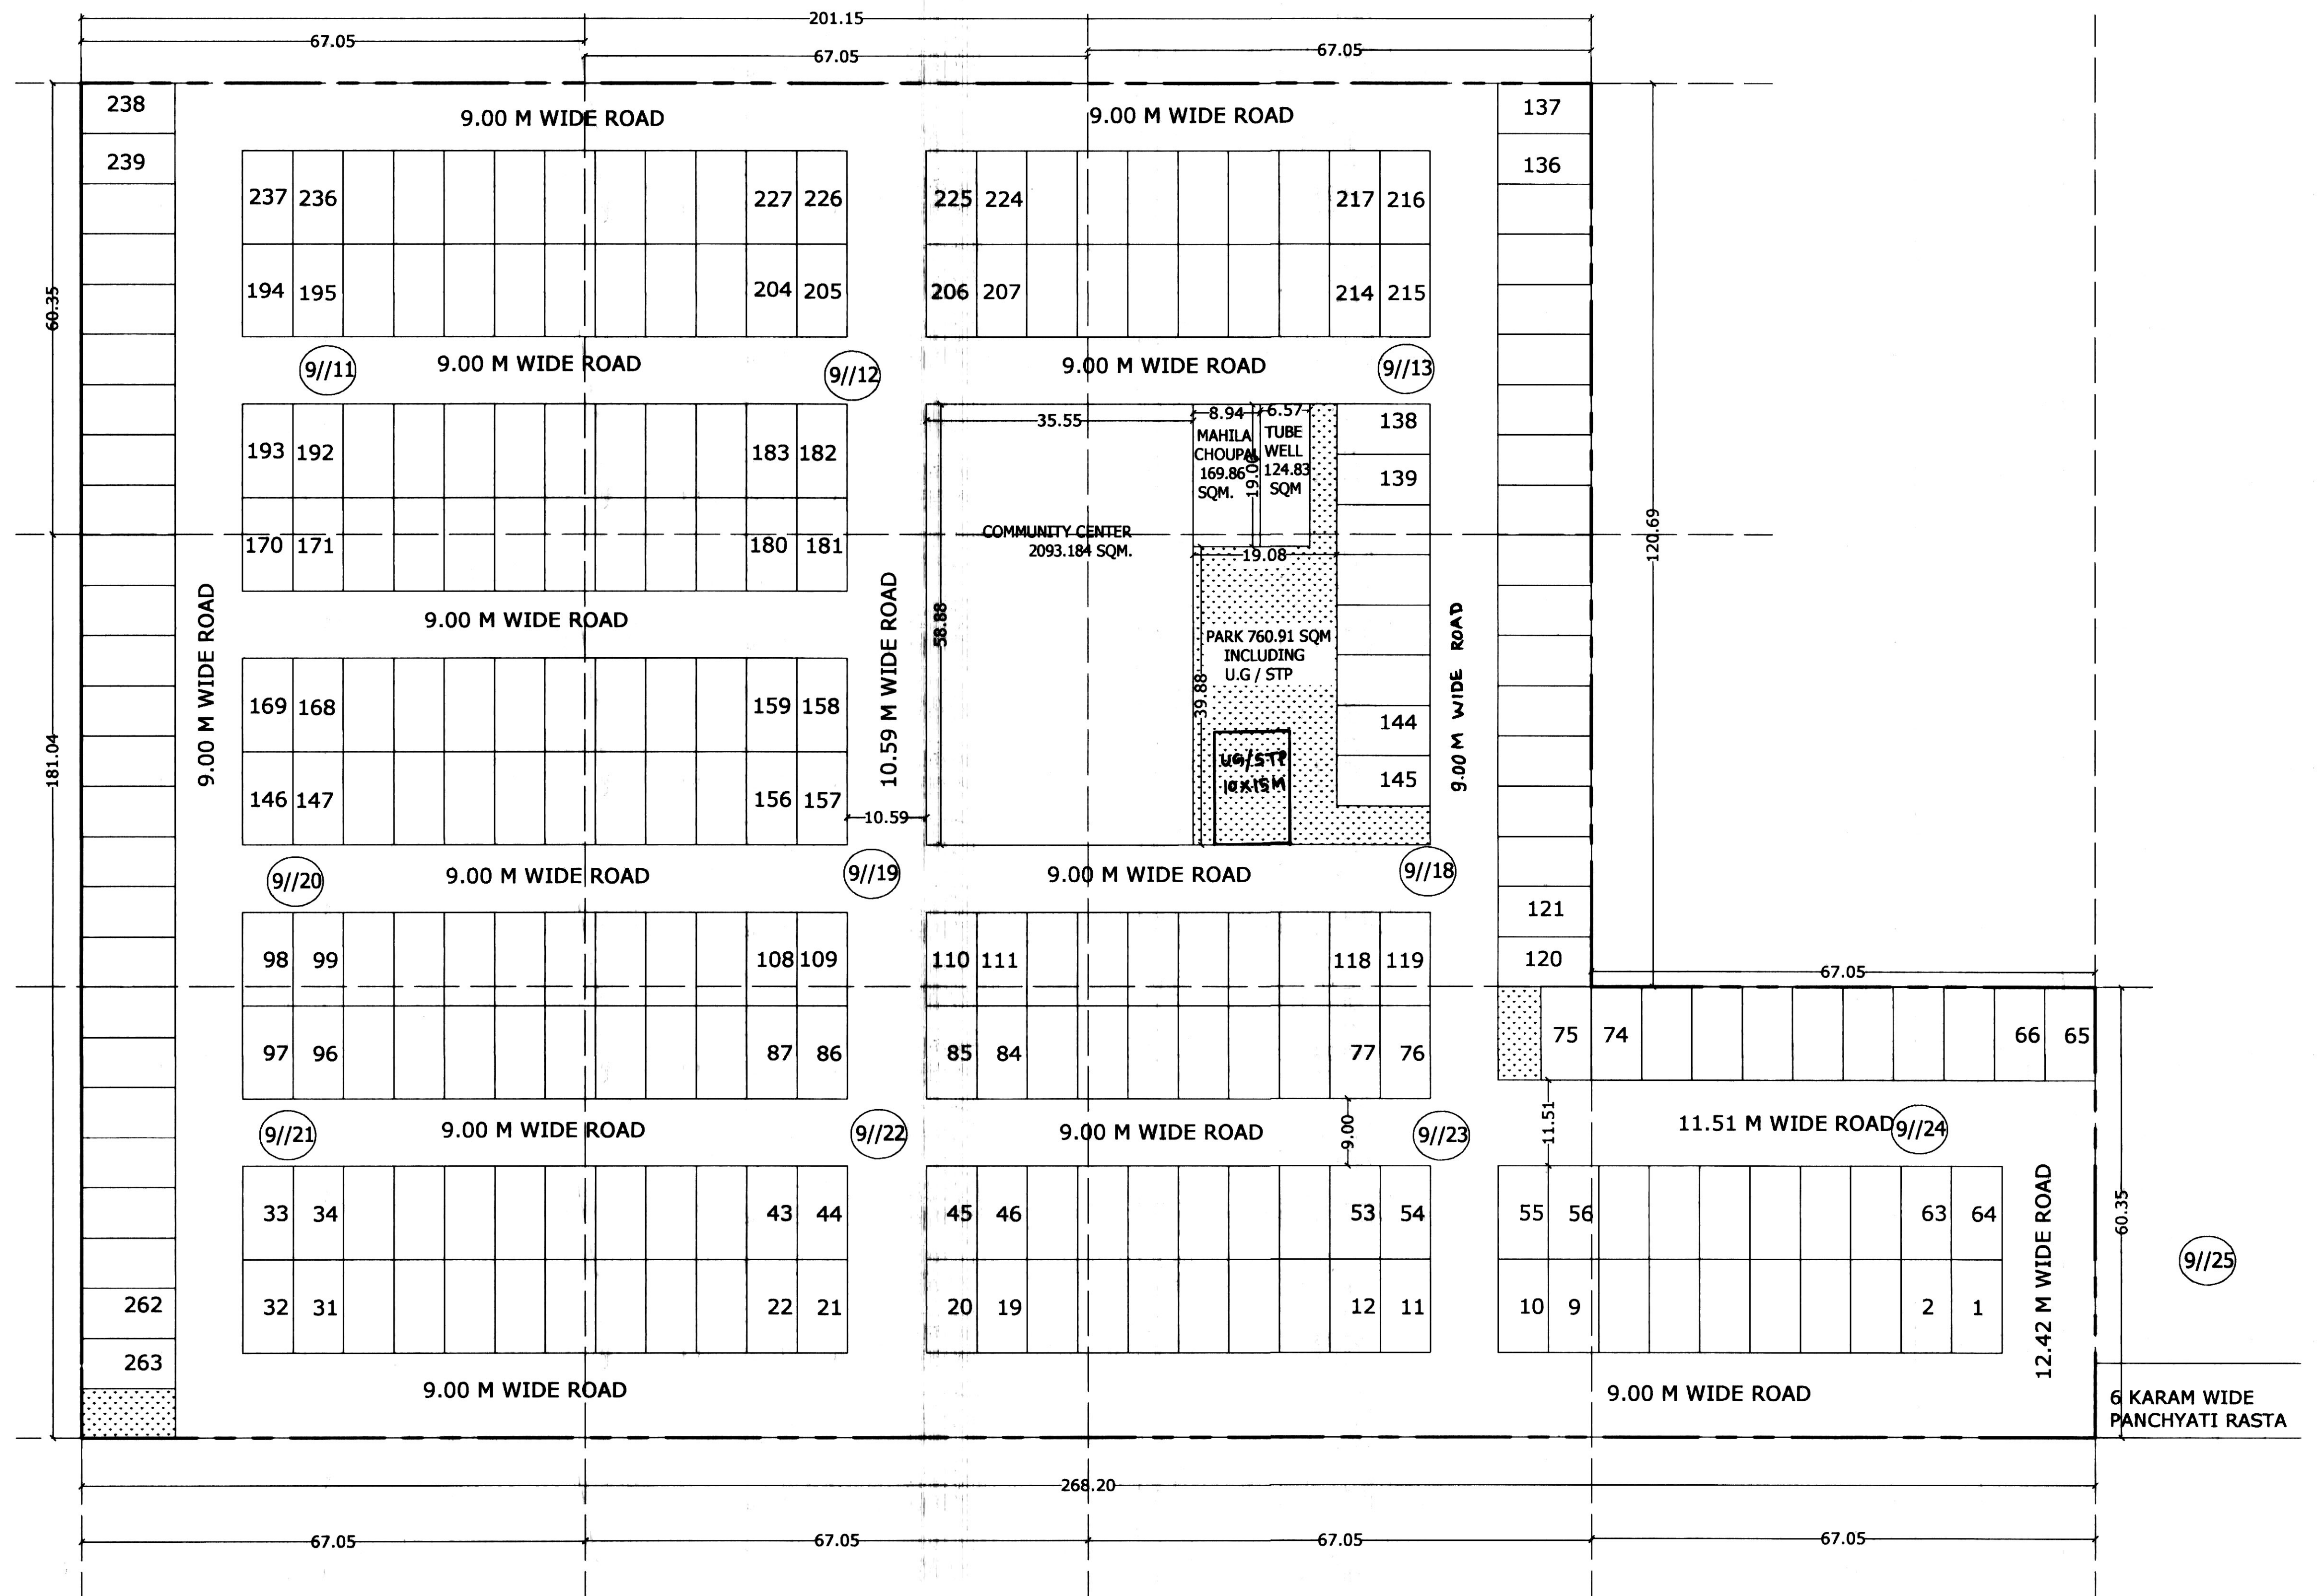

SUB-DIVISIONAL OFFICER,
MUNAK BLOCK, DISTRICT KARNAL
PANCHAYATI RAJ DEPARTMENT,
HARYANA, CHANDIGARH

B.D.P.O., MUNAK BLOCK,
DISTRICT KARNAL

CHAIRPERSON "MMGAY-2.0" - CUM -
SENIOR TOWN PLANNER, PANCHKULA
TOWN & COUNTRY PLANNING DEPARTMENT,
HARYANA, CHANDIGARH