

YAMUNA NAGAR-JAGADHRI

VILLAGE - RADAURI

LAYOUT-CUM-DEMARICATION PLAN OF THE RESIDENTIAL PLOTTED COLONY UNDER MUKHYA MANTRI GRAMIN AWAS YOJNA - 2.0 (MMGAY-2.0) IN KHASRA NO. 143, 144, 145 186 IN THE REVENUE ESTATE OF VILLAGE RADAURI, BLOCK - RADAUR, DISTRICT YAMUNA NAGAR, (HARYANA).

AREA DETAIL:-

TOTAL LAND AREA 13954.93 SQM AS PER SURVEY

DETAIL OF PLOTS	SIZE OF PLOTS	TOTAL NOS.	AREA (SQM)
1 TO 14, 16 TO 19, 22 TO 25, 28 TO 31 & 33 TO 32	6.71 X 12.47	86	7195.84
15, 20, 21, 26, 27, 32	7.87 X 12.47	6	584.83
TOTAL		92	7780.67

FACILITIES PROVIDED

1. STP 318.23 SQM.
2. MAHILA CHOPAL 141.66 SQM.
3. ELECTRIC TRANSFORMER 132.93 SQM.
4. MILK & VEGETABLE BOOTH 66.46 SQM.
5. TUBE-WELL 66.46 SQM.
6. I/G 2 NO. 152.75 SQM.
7. PARK 312.69 SQM.

AREA UNDER PLOTS = 7780.67 SQM (55.78)
AREA UNDER PUBLIC FACILITIES = 725.74 SQM
AREA UNDER PARK, I/G AND ROAD = 5444.42 SQM

LEGEND

SCHEME BOUNDARY

KILLA LINE

PARK/OPEN SPACE



NOTE:- THIS DRAWING HAS BEEN PREPARED ON THE BASIS OF SAJRA PLAN OF CONCERNED REVENUE ESTATE.

DRG. NO. DTP(Y) 160 / 2025 DATED 28.06.2025

SCALE:- 1CM = 06 MTR



DRAWN BY

RADHIKA TRACER

FIELD INVESTIGATOR


ANIL KUMAR

JUNIOR ENGINEER

CHECKED BY

MANINDER SINGH, P.A.

DEPTT. OF TOWN & COUNTRY PLANNING HARYANA

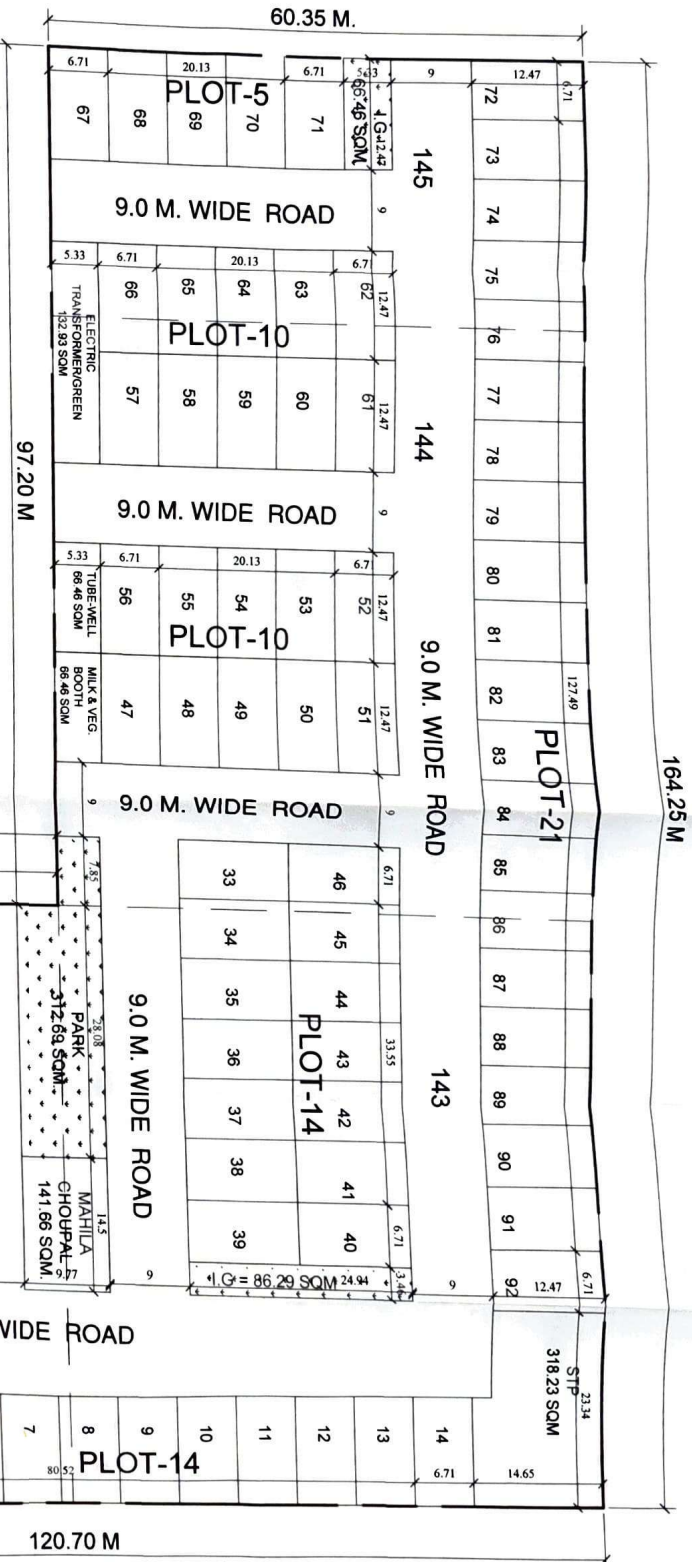

SCALE:- 1CM = 06 MTR

DRAWN BY RADHIKA TRACER

FIELD INVESTIGATOR ANIL KUMAR

JUNIOR ENGINEER

CHECKED BY MANINDER SINGH, P.A.

DEPTT. OF TOWN & COUNTRY PLANNING HARYANA

DISTRICT TOWN PLANNER (MEMBER), YAMUNA NAGAR

DISTRICT TOWN PLANNER (MEMBER), YAMUNA NAGAR

BLOCK DEVELOPMENT & PANCHAYAT OFFICER (MEMBER), YAMUNA NAGAR

SUB DIVISIONAL OFFICER PANCHAYAT (MEMBER), YAMUNA NAGAR

SENIOR TOWN PLANNER (MEMBER), PANCHKULA

EXISTING 7 KARAM WIDE RASTA