

LAYOUT CUM DEMARCATION PLAN OF
RESIDENTIAL PLOTS UNDER "MUKHYA MANTRI
GRAMIN AWAS YOJNA-3.0" (MMGAY-3.0)
GRAM PANCHAYAT
STRIC

VILLAGE DEMARCATION PLAN OF GRAMIN AWAS YOJNA-3.0" (MMGAY-3.0)	
GRAM PANCHAYAT	JOGNA KHERA
TEHSIL	KURUKSHETRA
AREA	THANESAR
REVENUE DETAIL/ KHASRA NO.	3.52 ACRES
CONTROLLED AREA	22/12, 19, 20, 21/1, 23/25/1
URBAN AREA	NA
DEVELOPMENT PLAN	YES
LEGEND:	

LEGEND

SCHEME BOUNDARY	
APPROACH ROAD	
ELECTRICITY LINE	
KHAL / NALLAH / DRAIN	
REVENUE RASTA	
PROPOSED RASTA	
PARKS / GREEN AREA	
DETAIL OF AREA	

DETAIL OF AREA CALCULATION

AREA UNDER SCHEME	3.52 ACRES (14281.33 SQM)
AREA UNDER PLOTS	1.964 ACRES (7948.65 SQM)
AREA UNDER MAHILA CHOUHAL	0.0425 ACRE (172.03 SQM)
AREA UNDER PARKS/ GREEN AREA	0.149 ACRE (605.185 SQM)
AREA UNDER ET (59.389 SQM), TW (82.364 SQM), = 141.753 SQM OR 0.035 ACR ES	

AREA UNDER ROADS	1.337 ACRES (5413.712 SQM)
------------------	----------------------------

UNDER ROADS		1.337 ACRES (5413.712 SQM)	
DETAILS OF PLOTS			
PLOT Nos.	PLOT SIZE	AREA	TOTAL AREA UNDER PLOTS
1-95	6.71x12.47 MT	83.67 SQM	7948.65 SQM

TOTAL PLOTTED AREA= 55.66%

SCALE 1:600

DRAWING NO - DTP(KK)/1240/26, DATED:- 12/02/2026

DRAWN BY: RAKESH NLAAR S.O.

PATVNAE SUSDB, KIRMAR

JUNIOR ENGINEER KRISHAN KUMAR

ASSISTANT TOWN (VACANT)
PLANNER


DATE: 10/10/1964 (10/10/1964)
BY: J. H. H. (J. H. H.)

INFO, PARAJAYATI, RA (MEMBER)

SIDE PLANT ~~PLANT~~ (MURDER)

DAVID KLEIN PLANN
SENIOR TOWN PLANNING ENGINEER

DEPARTMENT OF TCP. HARYANA

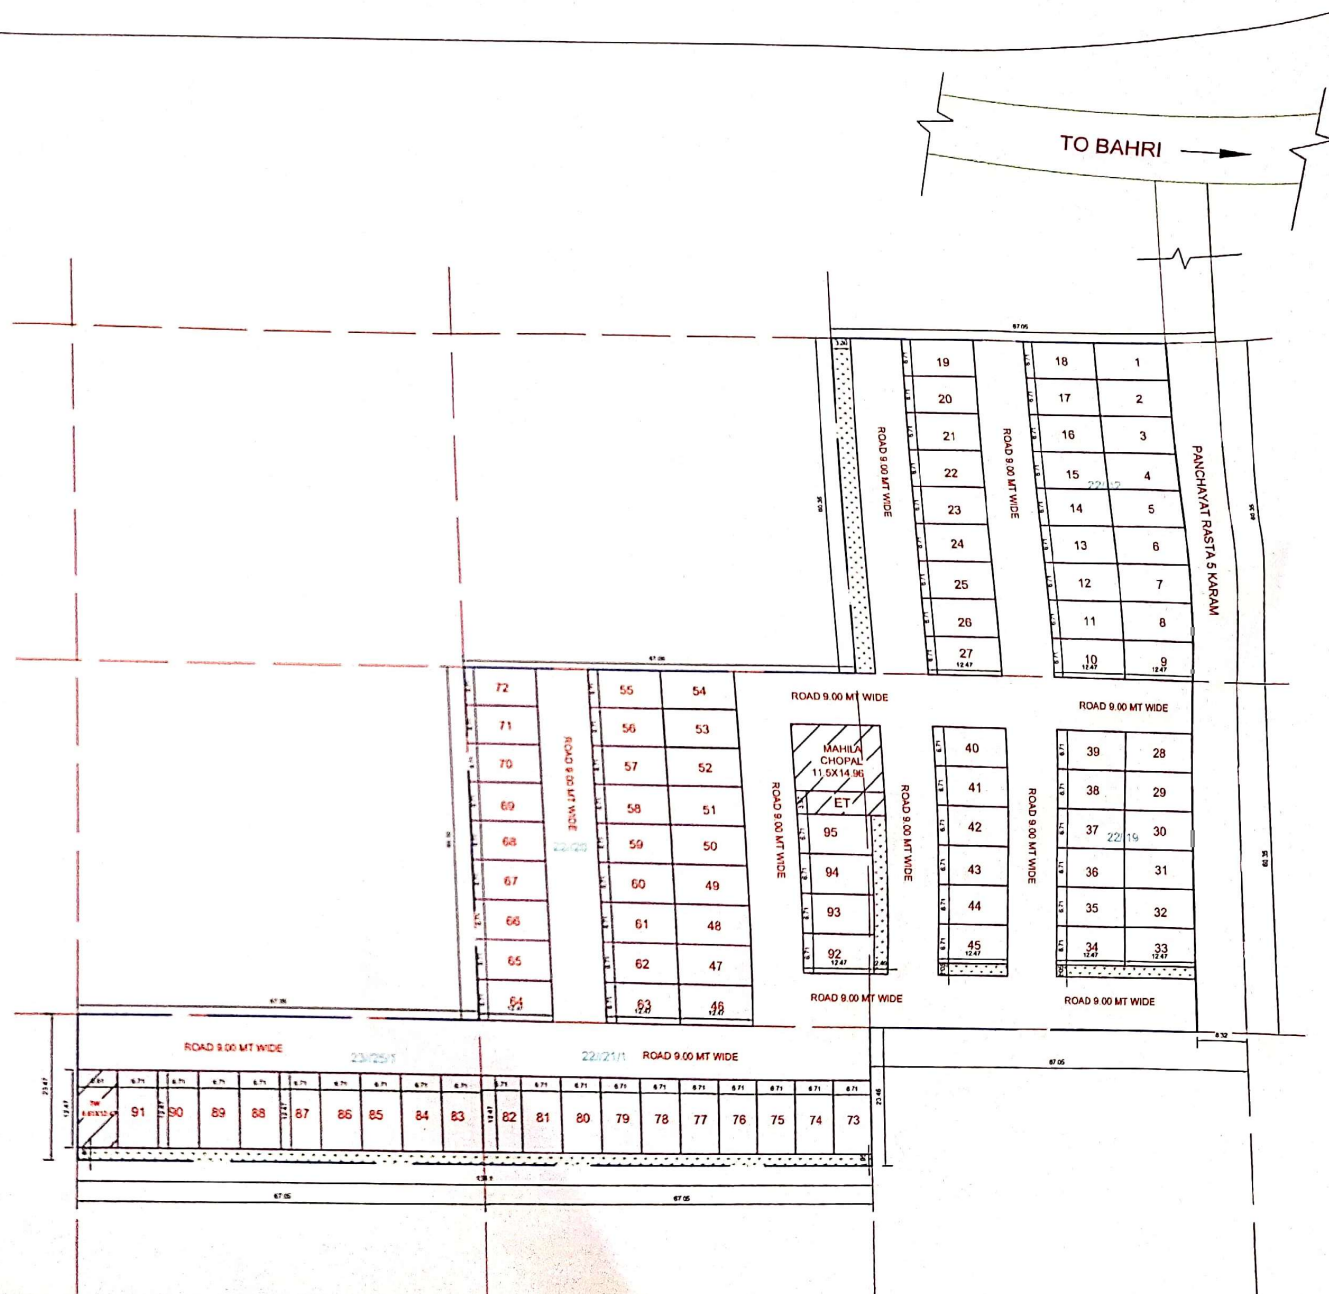

NOTE
KASTA APPROACH SHOWN AS PER
PANCHAYAT RESOLUTION.