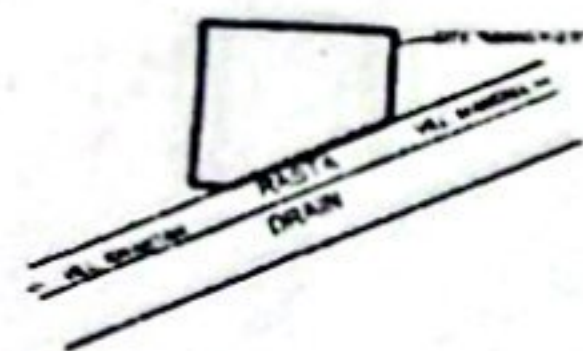


K A I T H A L

LAYOUT CUM DEMARCATION PLAN OF SITE APPROVED UNDER "MUKHYA MANTRI GRAMIN AWAS YOJNA - 2.0 (MMGAY-2.0), SITUATED AT KHASRA NO. 42/7,8,13/1,14/1, IN THE REVENUE ESTATE OF VILLAGE NOUCH, TEHSIL AND DISTRICT KAITHAL.

INSET PLAN
(NOT TO SCALE)



LEGEND :-

1. APPROVED "MMGAY" SCHEME BOUNDARY SHOWN THUS
2. OPEN SPACE / PARK SHOWN THUS
3. EXISTING ROAD SHOWN THUS
4. KACHHAREVENUE RASTA SHOWN THUS



DETAIL OF AREA

APPROVED "MMGAY-2.0" SCHEME AREA
NET PLANNED AREA
AREA UNDER PLOTS
AREA UNDER MAHILA CHOUPAL
AREA UNDER S.T.P.
AREA UNDER U.G.T.
AREA UNDER R.W.H.
AREA UNDER E.T.
AREA UNDER OPEN SPACE / PARK
AREA UNDER ROADS

AREA IN ACRES/SQ MTR.

= 3.24/13101.67
= 3.24/13101.67
= 1.78/195.94
= 0.04/167.35
= 0.03/138.78
= 0.05/234.58
= 0.02/82.18
= 0.01/79.97
= 0.308/1245.70
= 1.019/124.52

DETAIL OF NET PLANNED AREA - 3ACRE-1KANAL-18MARLA

SR. NO.	CATEGORY	SIZE	NO. OF PLOTS
1	4 MARLA	06.71 M X 12.47 M	84
2	MAHILA CHOUPAL	13.42 M X 12.47 M	01
3	S.T.P.	AS PER LAYOUT	01
4	U.G.T.	AS PER LAYOUT	01
5	R.W.H.	AS PER LAYOUT	01
6	E.T.	AS PER LAYOUT	01
	TOTAL		89

PLOTABLE AREA = 7898.80

= 60.29 % (APP.)

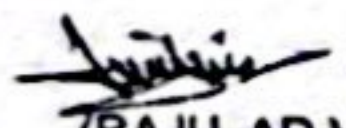
NOTES :-

1. ALL THE DIMENSIONS ARE IN METERS
2. THIS LAYOUT CUM DEMARCATION PLAN HAS BEEN PREPARED ON THE BASIS OF SURVEY PLAN RECEIVED FROM HOUSING FOR ALL DEPARTMENT, HARYANA AND LAND RESOLUTION AND SAURA RECEIVED FROM THE CONCERNED BDO OFFICE
3. THE EXACT LOCATION, SHAPE AND SIZE OF EACH PLOTS ARE SUBJECT TO ACTUAL DEMARCATION AT SITE

SCALE :- 1 CM. = 5 MTS.

DRAWING. NO. DTP (KTL) 304/2025

DATED:- 04.07.2025

DRAWN BY :- 
(RAJU, AD)

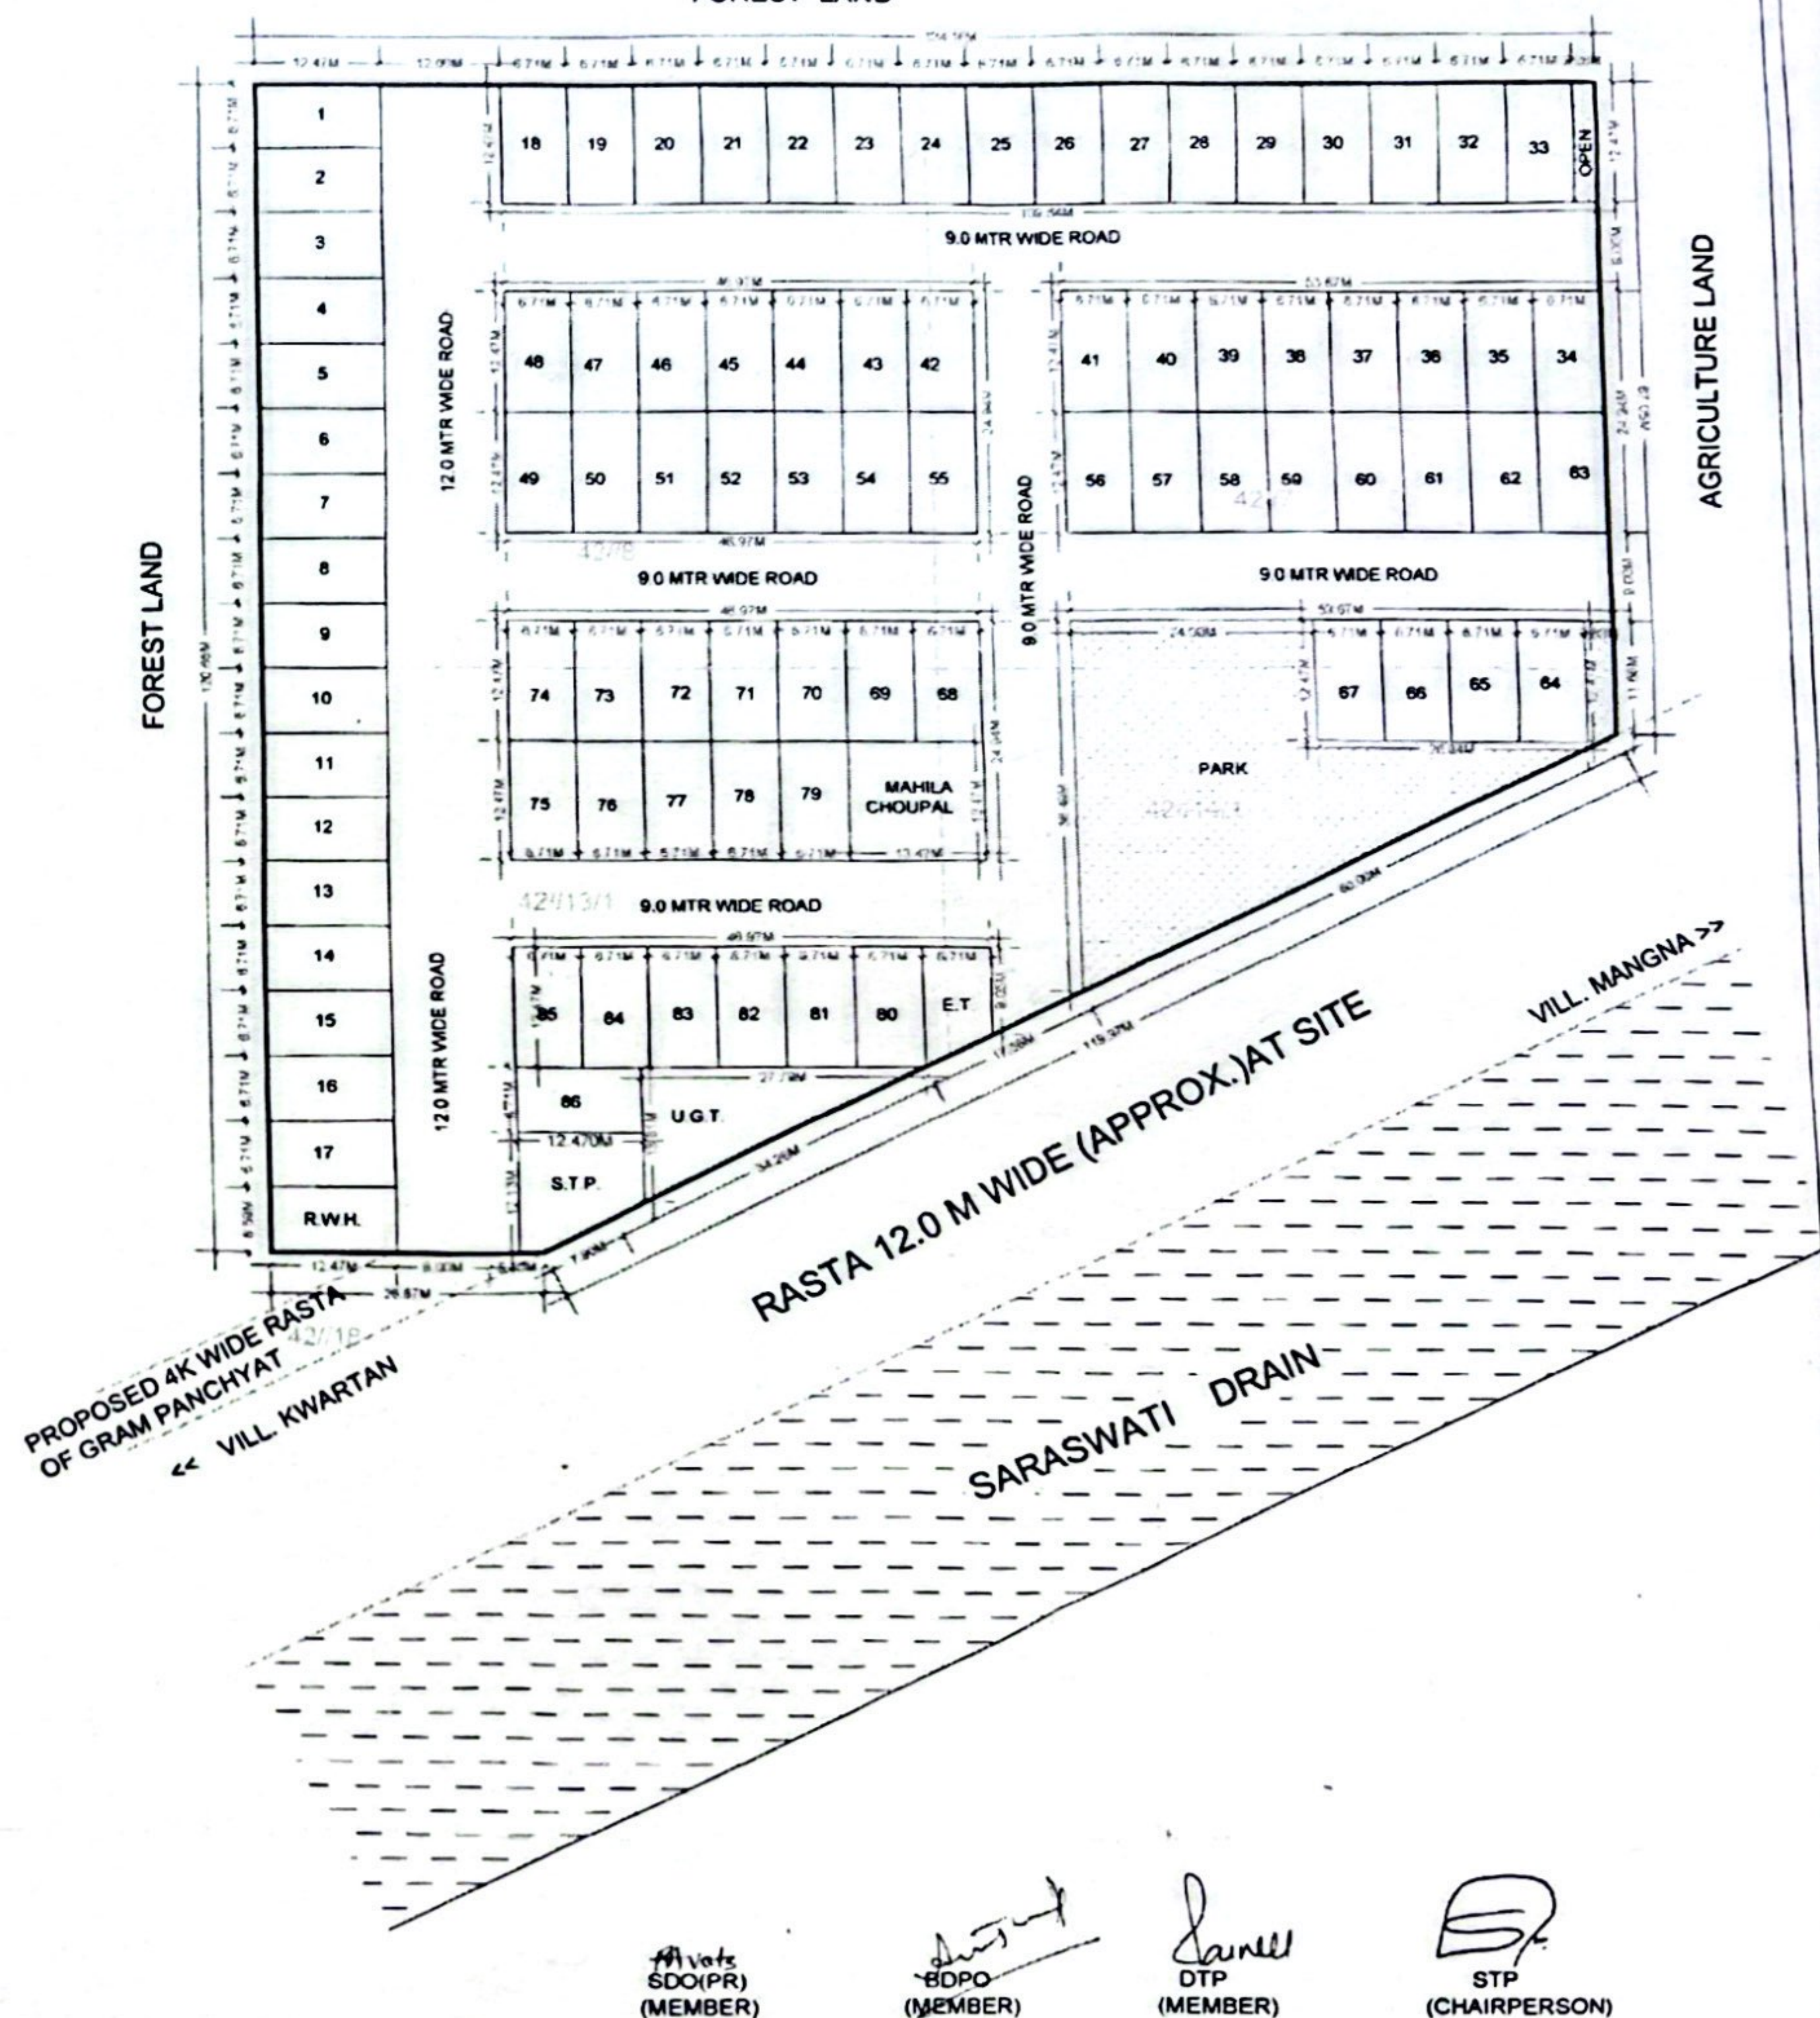
JUNIOR DRAFTSMAN :- (VACANT)

PLANNING ASSISTANT :- (VACANT)

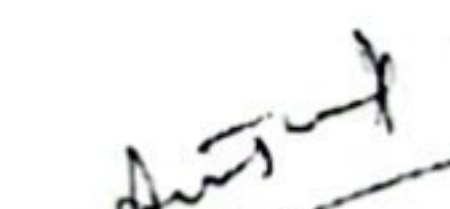
ASSTT. TOWN PLANNER :- (VACANT)

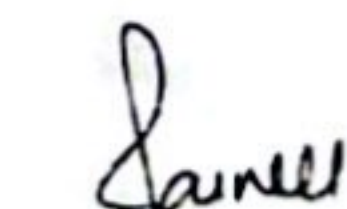
DEPARTMENT. OF T & C PLANNING, HARYANA, CHANDIGARH.

FOREST LAND



A. Vats
SDO (PR)
(MEMBER)


BDO
(MEMBER)


DTP
(MEMBER)


STP
(CHAIRPERSON)