

KARNAL

LAYOUT PLAN OF HOUSING SCHEME UNDER "MUKHYAMANTRI GRAMIN AWAS YOJANA - 2.0" (MMGAY-2.0) AREA MEASURING 6.71 ACRES, COMPRISING IN KHASRA NOS. 58//17, 18, 19, 20/2, 22, 23 & 24 IN THE REVENUE ESTATE OF VILLAGE BOHLA KHALSA, BLOCK-NILOKHERI, DISTRICT KARNAL.

DETAILS OF PLOTTED AREA :-

SR.NO.	PARTICULAR	SIZE	NOS.	AREA
1.	RESI. PLOT	6.71X12.47 M	176	14726.57 SQM.
2.	COMMUNITY CENTRE	AS PER SITE	1	2131.90 SQM.
3.	MAHILA CHOUPAL	13.42X12.47	1	167.34 SQM.
4.	EXIST. TUBE WELL	13.42X12.47	1	167.34 SQM.
TOTAL PLOTTED AREA				= 17193.15 SQM. OR 4.248 ACRES

DETAILS OF AREA :-

AREA OF SCHEME	= 6.71 ACRES
PLOTTED AREA	= 4.248 ACRES (63.31%)
AREA UNDER ROADS / PARKS / OPEN SPACES	= 2.462 ACRES

LEGEND :-

SCHEME BOUNDARY

HT. LINE

KILLA LINE

VILLAGE BOUNDARY

PARK / OPEN SPACES

NOTE:-

1. ALL DIMENSIONS ARE IN METERS.
2. THIS LAYOUT PLAN HAS BEEN PREPARED ON THE BASIS OF SHAJRA PLAN PROVIDED BY BDPO, NILOKHERI.
3. THE KHASRA NOS. OF MMGAY-2.0 SCHEME FALLS OUTSIDE CONTROLLED AREA AND URBAN AREA OF DISTRICT KARNAL.
4. THIS SITE DOES NOT FALL IN NCZ SURVEY REPORT APPROVED BY DLSC AND SENT TO SLC.

SCALE: 1 CM = 6 MTR.

NORTH



DRAWING NO. D.T.P. (K) 1782 / 2026 DATED:- 29.01.2026

DRAWN BY:- RAJNEESH KUMAR (TRACER)

CHECKED BY:- DHANI RAM RANGA (JD)

PARDEEP KUMAR (SD)


RAMESH KUMAR (SD)

PLANNING ASSISTANT (VACANT)

ASSTT. TOWN PLANNER MOHIT SINGH

DISTT. TOWN PLANNER GUNJAN VERMA

DEPTT.OF TOWN & COUNTRY PLANNING HARYANA

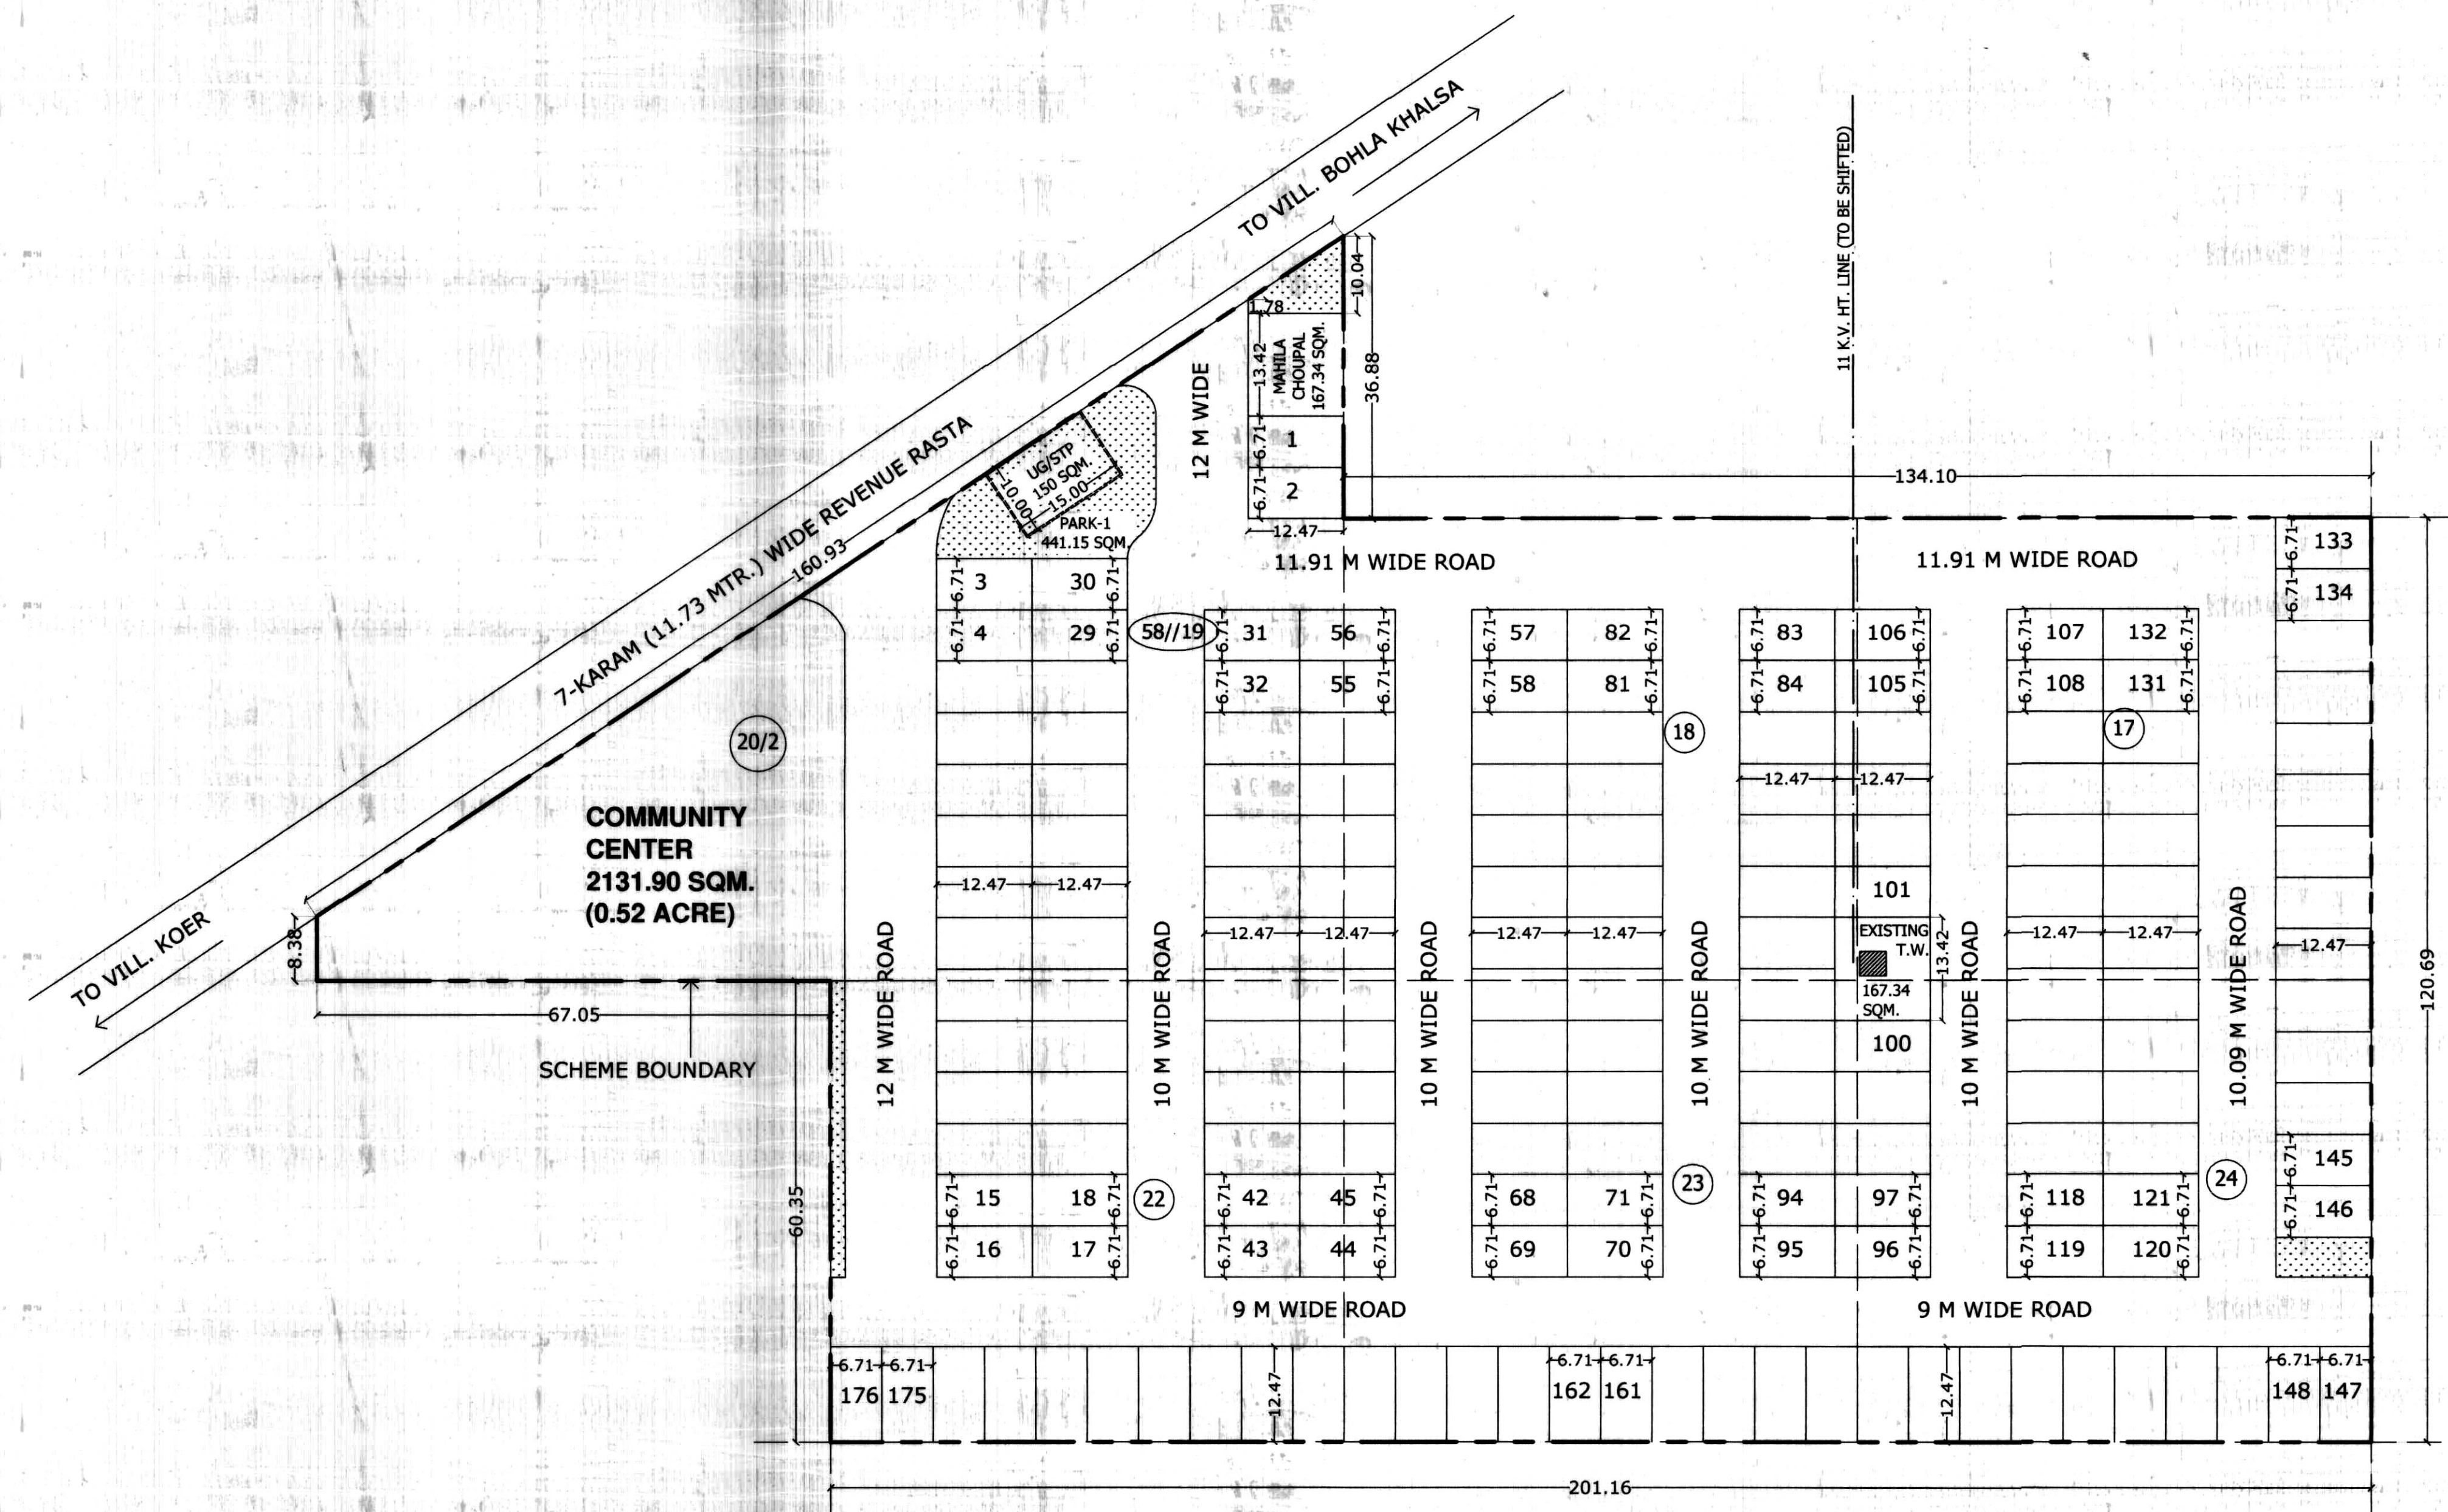

SUB DIVISIONAL OFFICER,
NILOKHERI BLOCK, DISTRICT KARNAL
PANCHAYATI RAJ DEPARTMENT,
HARYANA, CHANDIGARH

B.D.P.O., NILOKHERI BLOCK,
DISTRICT KARNAL

CHAIRPERSON "MMGAY-E" - CUM -
SENIOR TOWN PLANNER, PANCHKULA
TOWN & COUNTRY PLANNING DEPARTMENT,
HARYANA, CHANDIGARH