

KARNAL

LAYOUT PLAN OF HOUSING SCHEME UNDER "MUKHYAMANTRI GRAMIN AWAS YOJANA - 2.0" (MMGAY-2.0) AREA MEASURING 4.72 ACRES, COMPRISING IN KHASRA NOS. 21/18, 19/1, 23/1, 23/2, 23/3, 2 IN THE REVENUE ESTATE OF VILLAGE CHAKDA, BLOCK-NISSING, DISTRICT KARNAL.

AREA STATEMENT - CHAKDA VILLAGE (Distt. KARNAL)

Description	Acres	SQ.M.	%
SITE AREA	4.720	19,101.130	
PROPOSED AREA DETAILS			
RESIDENTIAL PLOTS	2.707	10,954.200	57.35%
MAHILA CHAUPAL	0.042	170.110	
GREEN AREA	0.320	1,296.010	
ROAD AREA	1.637	6,622.820	

LEGEND :-

SCHEME BOUNDARY

HT. LINE

KILLA LINE

VILLAGE BOUNDARY

PARK / OPEN SPACES

NOTE:-

- ALL DIMENSIONS ARE IN METERS.
- THIS LAYOUT PLAN HAS BEEN PREPARED ON THE BASIS OF SAJRA PLAN PROVIDED BY BDPO, NISSING.
- THE KHARSA NOS. OF MMGAY-2.0 SCHEME FALLS OUTSIDE CONTROLLED AREA AND URBAN AREA OF DISTRICT KARNAL.
- THIS SITE DOES NOT FALL IN NCZ SURVEY REPORT APPROVED BY DLSC AND SENT TO SLC.

SCALE: 1 CM = 5 MTR.

NORTH



DRAWING NO. D.T.P (K) 1748/2025 DATED:- 25.07.2025

DRAWN BY:- DHANI RAM RANGA (JD)

CHECKED BY:- PARDEEP KUMAR (SD), RAMESH KUMAR (SD)

PLANNING ASSISTANT (VACANT)

RAM NIWAS, J.E.

ASSTT. TOWN PLANNER MOHIT SINGH

JOGINDER SINGH, PATWARI


DISTT. TOWN PLANNER GUNJAN VERMA

DEPTT.OF TOWN & COUNTRY PLANNING HARYANA

AMUPUR

TO

MAJRA

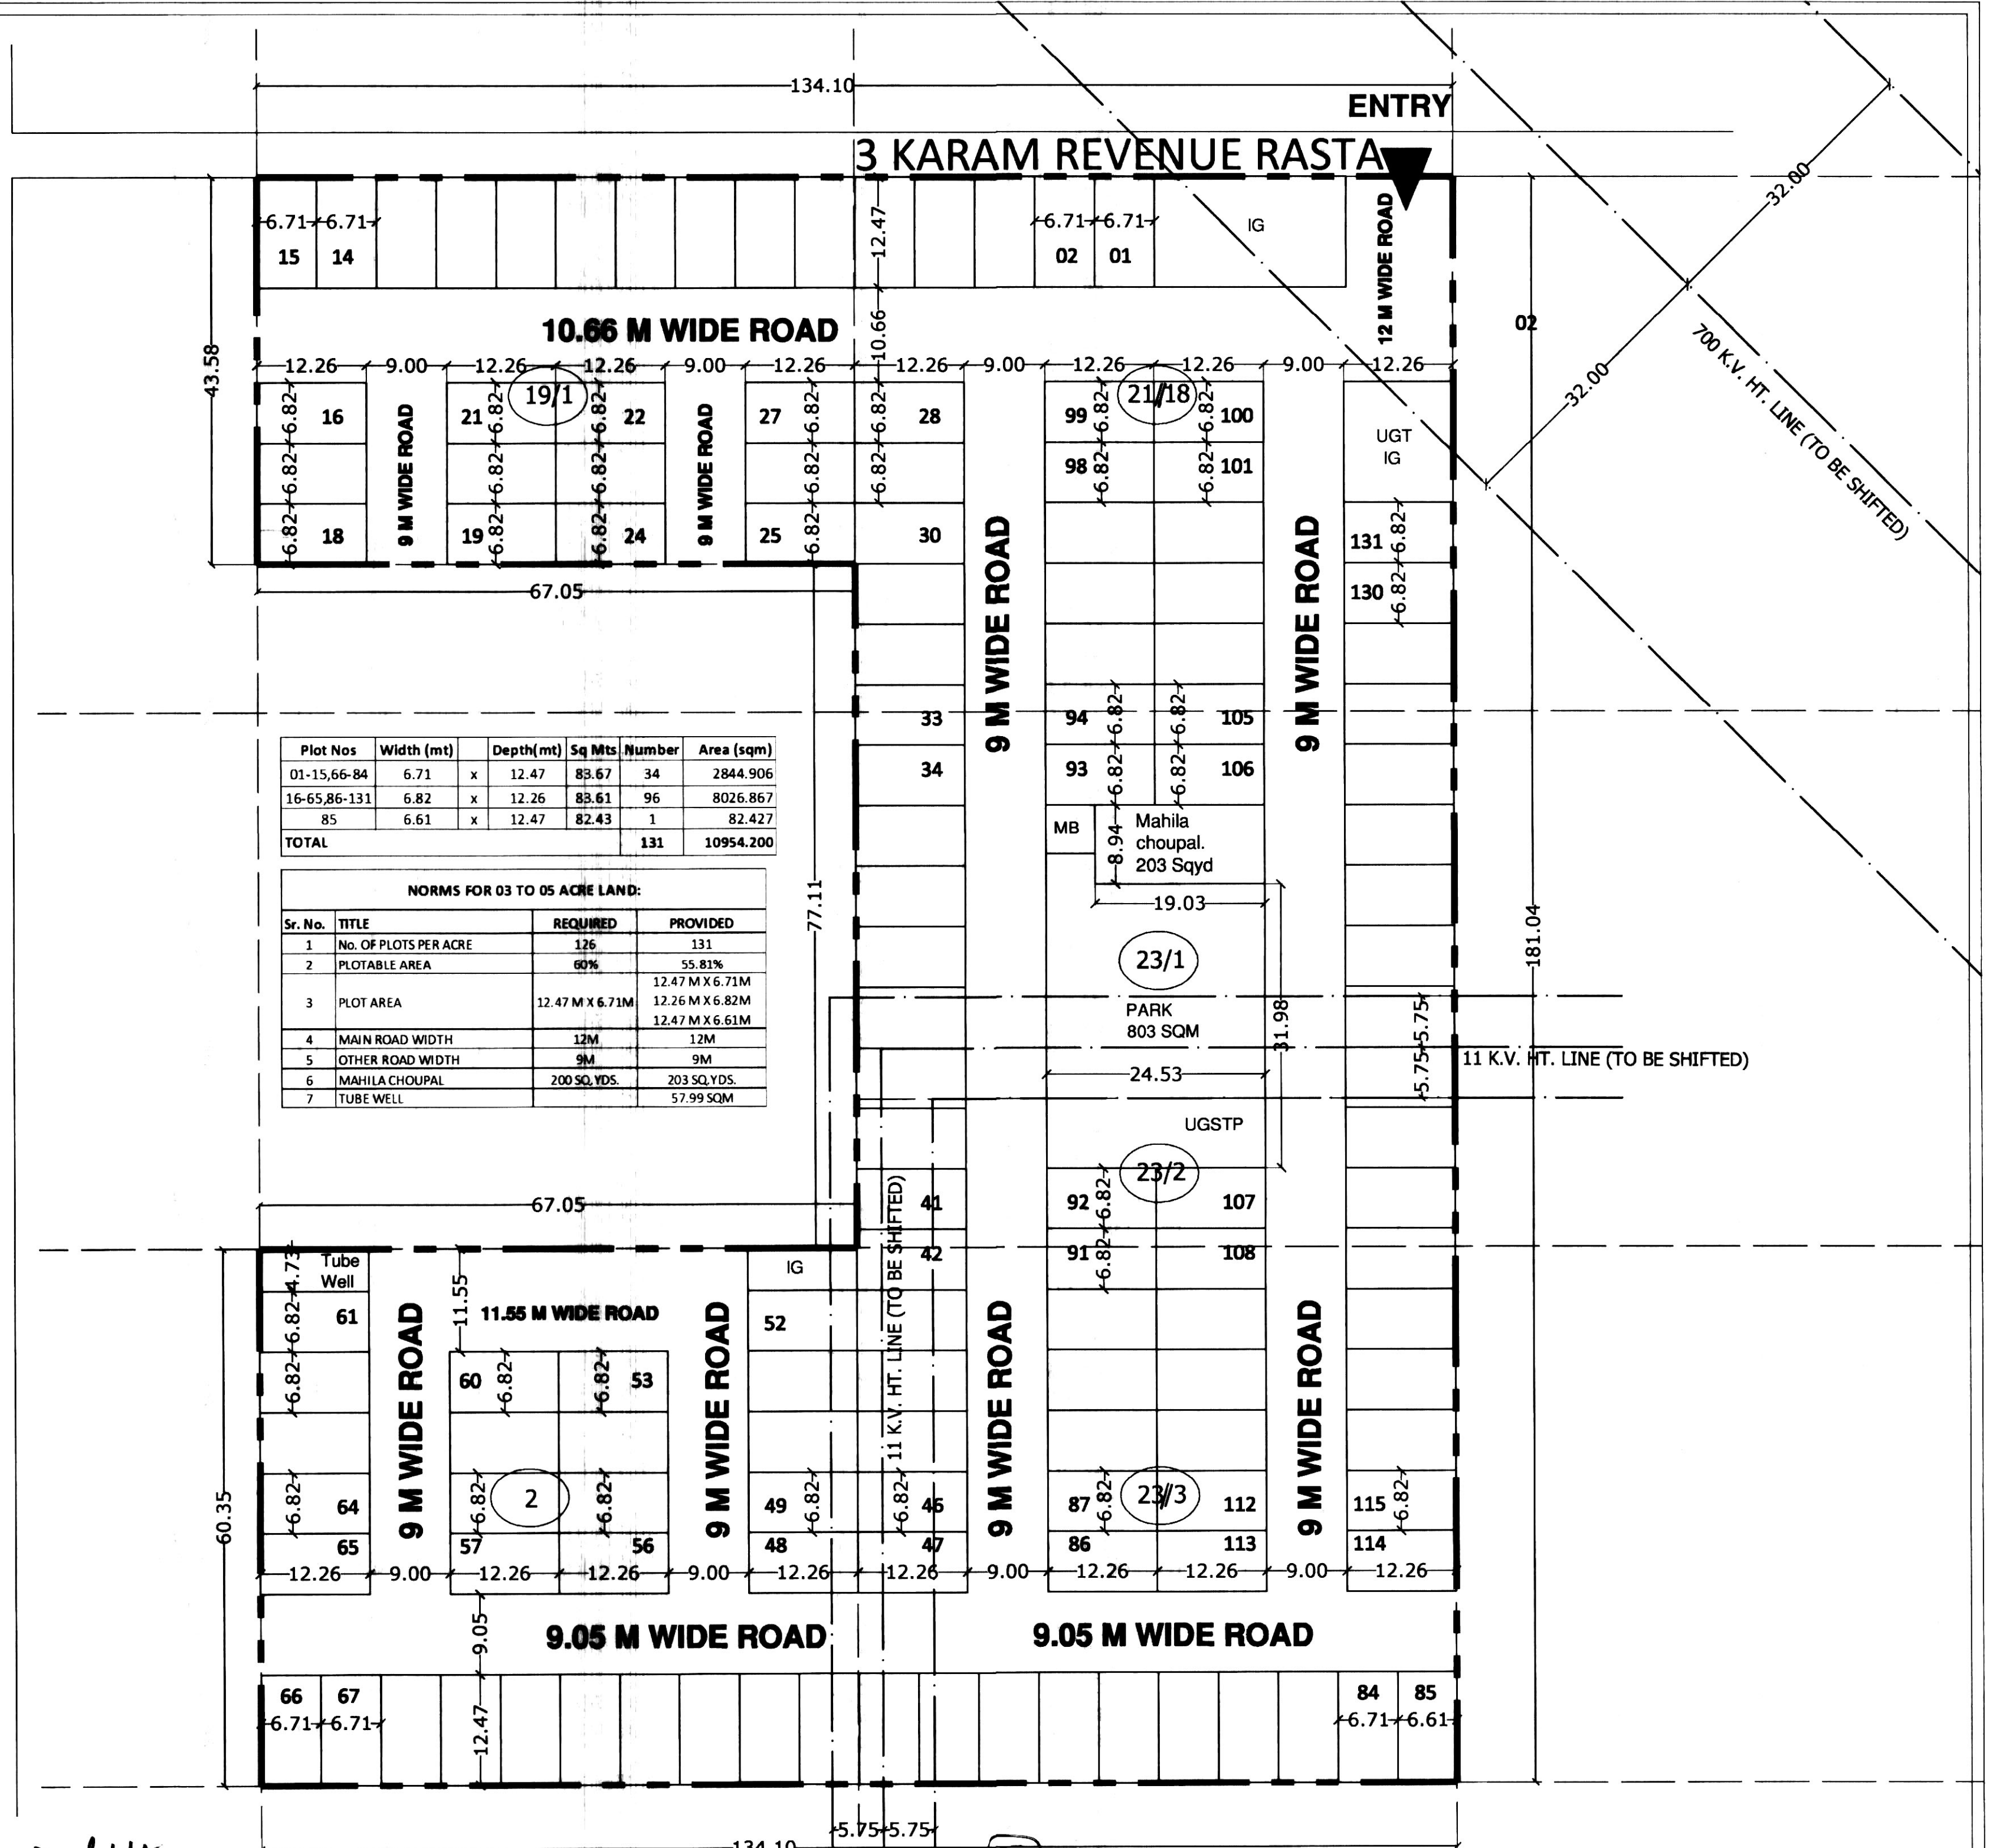

SUB DIVISION OFFICER,
NISSING BLOCK, DISTRICT KARNAL
PANCHAYATI RAJ DEPARTMENT,
HARYANA, CHANDIGARH

B.D.P.O., NISSING BLOCK,
DISTRICT KARNAL

CHAIRPERSON "MMGAY-2.0" - CUM -
SENIOR TOWN PLANNER, PANCHKULA
TOWN & COUNTRY PLANNING DEPARTMENT,
HARYANA, CHANDIGARH