

# KARNAL

LAYOUT PLAN OF HOUSING SCHEME UNDER "MUKHYAMANTRI GRAMIN AWAS YOJANA - 2.0" (MMGAY-2.0) AREA MEASURING 4.61 ACRES, COMPRISING IN KHASRA NOS. 88/2 MIN, 3 MIN, 8 MIN, 9, 12 & 13 IN THE REVENUE ESTATE OF VILLAGE GUNYANA, BLOCK-NISSING, DISTRICT KARNAL

| DETAILS OF PLOTTED AREA :- |                |                |                                |
|----------------------------|----------------|----------------|--------------------------------|
| SR.NO.                     | PARTICULAR     | SIZE           | NOS.                           |
| 1.                         | RESI. PLOT     | 6.71X12.47 M   | 121                            |
| 2.                         | MAHILA CHOUPAL | 15.94 X10.66 M | 1                              |
| 3.                         | TUBE WELL      | 15.94X 7.85 M  | 1                              |
| TOTAL PLOTTED AREA         |                |                | = 10419.568 SQM. OR 2.57 ACRES |

| DETAILS OF AREA :-                     |                       |
|----------------------------------------|-----------------------|
| AREA OF SCHEME                         | = 4.61 ACRES          |
| AREA UNDER ROADS / PARKS / OPEN SPACES | = 2.57 ACRES (55.74%) |
|                                        | = 2.04 ACRES          |

| LEGEND :-          |     |
|--------------------|-----|
| SCHEME BOUNDARY    | --- |
| HT. LINE           | --- |
| KILLA LINE         | --- |
| VILLAGE BOUNDARY   | --- |
| PARK / OPEN SPACES | --- |

NOTE:-  
1. ALL DIMENSIONS ARE IN METERS.  
2. THIS LAYOUT PLAN HAS BEEN PREPARED ON THE BASIS OF SAJIRA PLAN PROVIDED BY BDPO, NISSING.  
3. THE KHASRA NOS. OF MMGAY-2.0 SCHEME FALLS IN URBAN AREA NISSING.  
4. THE KHASRA NOS. OF MMGAY-2.0 SCHEME FALLS OUTSIDE CONTROLLED AREA OF DISTRICT KARNAL.  
5. THIS SITE DOES NOT FALL IN NCZ SURVEY REPORT APPROVED BY DLSC AND SENT TO SLC.


SCALE: 1 CM = 5 MTR. NORTH

DRAWING NO. D.T.P. (K) 1723 / 2025 DATED:- 10.07.2025

|                     |                                         |
|---------------------|-----------------------------------------|
| DRAWN BY:-          | RAJNEESH KUMAR (TRACER)                 |
| CHECKED BY:-        | DHANI RAM RANGA (JD) PARDEEP KUMAR (SD) |
| PLANNING ASSISTANT  | RAMESH KUMAR (SD) RAMNIVAS, J.E.        |
| ASSTT. TOWN PLANNER | MOHIT SINGH                             |
| DISTT. TOWN PLANNER | SATISH KUMAR                            |

DEPTT. OF TOWN & COUNTRY PLANNING HARYANA

AGRICULTURE/ PANCHAYAT LAND

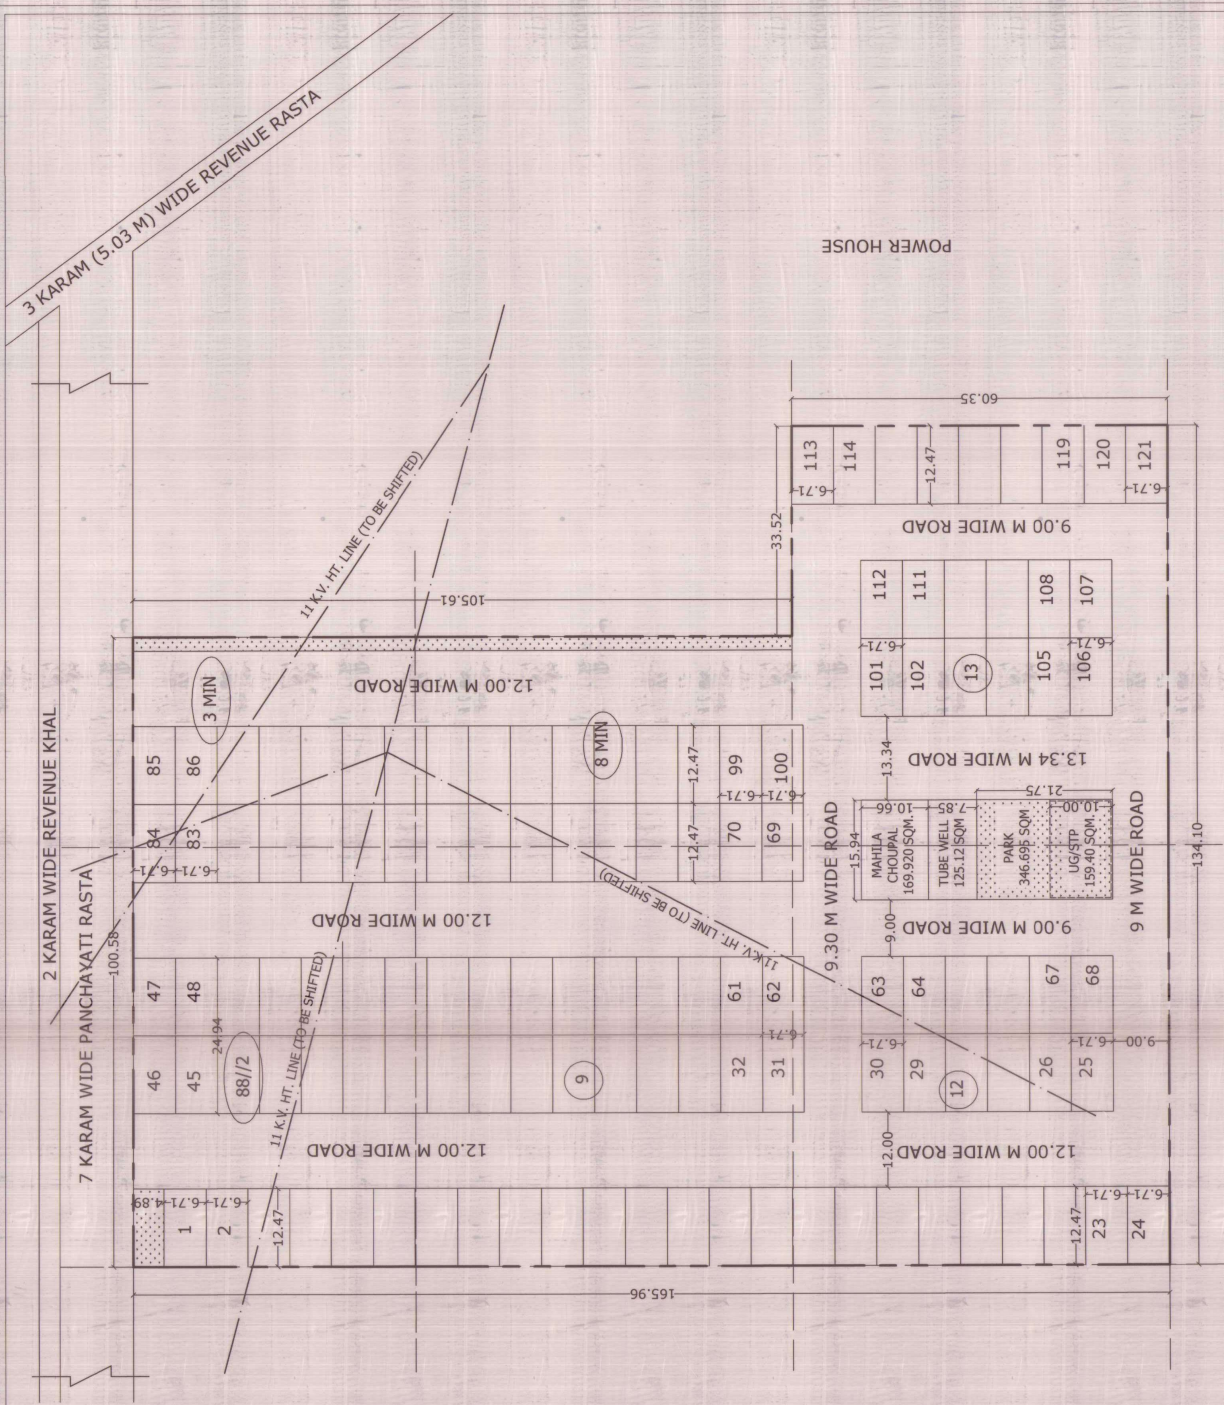

AGRICULTURE/ PANCHAYAT LAND

SUB DIVISIONAL OFFICER, DISTRICT KARNAL  
PANCHAYATI RAJ DEPARTMENT,  
HARYANA, CHANDIGARH

S.D.P.O. NISSING BLOCK,  
DISTRICT KARNAL

CHAIRPERSON "MMGAY-2.0" CUM,  
SENIOR TOWN PLANNER, PANCHKULA  
TOWN & COUNTRY PLANNING DEPARTMENT,  
HARYANA, CHANDIGARH