

KARNAL

LAYOUT PLAN OF HOUSING SCHEME UNDER "MUKHYAMANTRI GRAMIN AWAS YOJANA-EXTENSION" (MMGAY-E) AREA MEASURING 3.0 ACRES, COMPRISING IN KHASRA NOS. 46/17, 24 & 25 IN THE REVENUE ESTATE OF VILLAGE HINORI, BLOCK-INDRI, DISTRICT KARNAL.


DETAILS OF PLOTTED AREA :-			
Sr.NO.	PARTICULAR	SIZE	NOS.
1.	RES. PLOT	6.71X12.47 M	70
2.	MAHILA CHOUPAL	11.08X15.50 M	1
3.	TUBE WELL	11.08X9.44 M	1
TOTAL PLOTTED AREA		= 8886.55 SQM. OR 1.701 ACRES	

DETAILS OF AREA :-	
AREA OF SCHEME	= 3.00 ACRES
AREA UNDER ROADS / PARKS / OPEN SPACES	= 1.701 ACRES (56.70%)

LEGEND :-	
SCHEME BOUNDARY	---
HT. LINE	---
KULLA LINE	---
VILLAGE BOUNDARY	---
PARK / OPEN SPACES	---

NOTE:- DIMENSIONS ARE IN METERS.
2. THIS LAYOUT PLAN HAS BEEN PREPARED ON THE BASIS OF SAIPA PLAN PROVIDED BY BPO, INORI.
3. THE KHASRA NOS. OF MMGAY-2.0 SCHEME FALLS IN URBAN AREA LADWA (DISTRICT KURUKSHETRA).
4. CONTROLLED AREA OF DISTRICT KARNAL.
5. THIS SITE DOES NOT FALL IN NCZ SURVEY REPORT APPROVED BY DLSC AND SENT TO SLC.

SCALE: 1 CM = 5 MTR.	NORTH	DATED:- 10.07.2025
DRAWN BY:-	RAJESH KUMAR (TRACER)	
CHECKED BY:-	DHAN RAM RANGA (JD)	PARDIEP KUMAR (JD)
PLANNING ASSISTANT	RAJESH KUMAR (SD)	MOHIT, J.E.
ASSTT. TOWN PLANNER	MOHIT SINGH	JOGINDER SINGH, PATWARI
DISTT. TOWN PLANNER	SATISH KUMAR	
DEPTT. OF TOWN & COUNTRY PLANNING HARYANA		

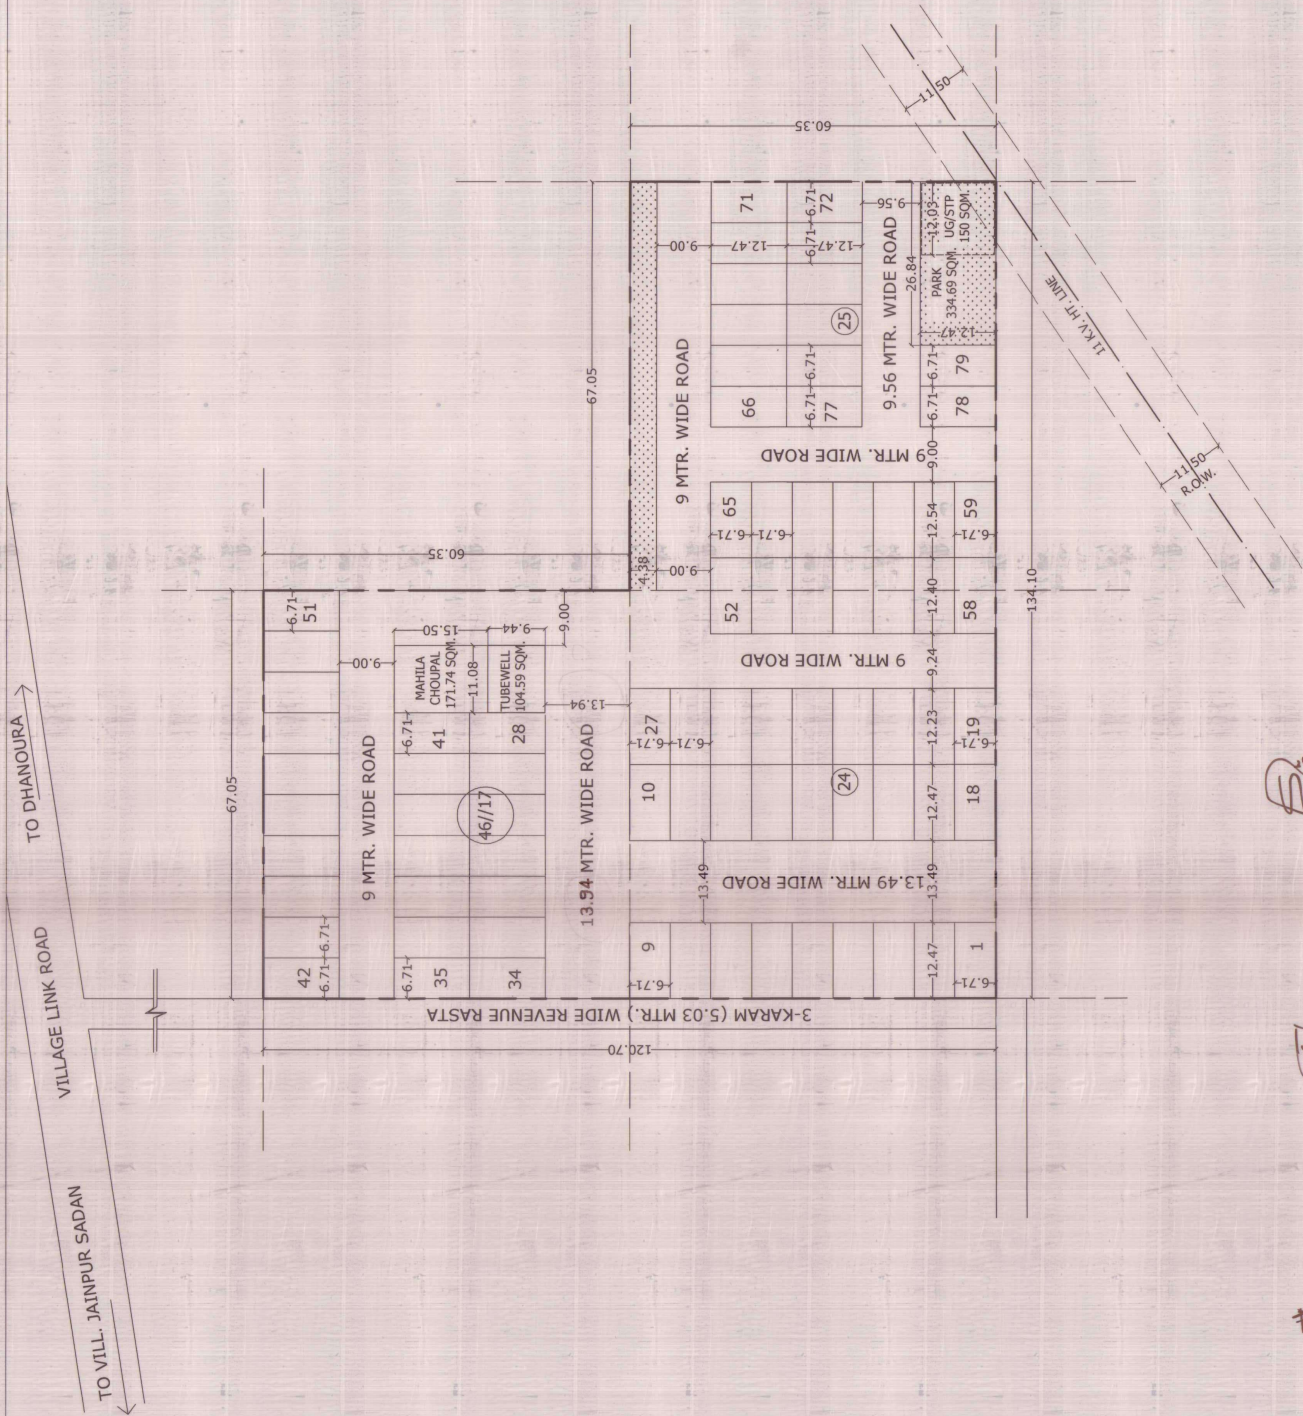

CHAIRPERSON "MMGAY-E", JUM-
SENIOR TOWN PLANNER, PANCHKULA
TOWN & COUNTRY PLANNING DEPARTMENT,
HARYANA, CHANDIGARH

S.D.O., INDI BLOCK,
DISTRICT KARNAL

SUB DIVISIONAL OFFICER,
INDRI BLOCK, DISTRICT KARNAL,
PANCHAYATI RAJ DEPARTMENT,
HARYANA, CHANDIGARH