

# KARNAL

LAYOUT PLAN OF HOUSING SCHEME UNDER "MUKHYAMANTRI GRAMIN AWAS YOJANA - 2.0" (MMGAY-2.0) AREA MEASURING 3.94 ACRES, COMPRISING IN KHASRA NOS. 65/7, 8, 9/1 MIN & 14 IN THE REVENUE ESTATE OF VILLAGE PATEHRA, BLOCK-INDRI, DISTRICT KARNAL.

## DETAILS OF PLOTTED AREA :-

| SR.NO.             | PARTICULAR     | SIZE           | NOS. | AREA                          |
|--------------------|----------------|----------------|------|-------------------------------|
| 1.                 | RESI PLOT      | 6.71X12.47 M   | 84   | 7028.59 SQM.                  |
| 2.                 | MAHILA CHOUPAL | 13.42 X12.47 M | 1    | 167.34 SQM.                   |
| 3.                 | TUBE WELL      | AS PER SITE    | 1    | 128.00 SQM.                   |
| TOTAL PLOTTED AREA |                |                |      | = 7323.93 SQM. OR 1.809 ACRES |

## DETAILS OF AREA :-

|                                        |                        |
|----------------------------------------|------------------------|
| AREA OF SCHEME                         | = 3.94 ACRES           |
| PLOTTED AREA                           | = 1.809 ACRES (45.91%) |
| AREA UNDER ROADS / PARKS / OPEN SPACES | = 2.131 ACRES          |

## LEGEND :-

|                    |     |
|--------------------|-----|
| SCHEME BOUNDARY    | --- |
| HT. LINE           | --- |
| KILLA LINE         | --- |
| VILLAGE BOUNDARY   | --- |
| PARK / OPEN SPACES | --- |

## NOTE:-

1. ALL DIMENSIONS ARE IN METERS.
2. THIS LAYOUT PLAN HAS BEEN PREPARED ON THE BASIS OF SAURA PLAN PROVIDED BY BDPO, INDRI.
3. THE KHASRA NOS. OF MMGAY-2.0 SCHEME FALLS OUTSIDE CONTROLLED AREA AND URBAN AREA OF DISTRICT KARNAL.
4. THIS SITE DOES NOT FALL IN NCZ SURVEY REPORT APPROVED BY DLSC AND SENT TO SLC.

SCALE: 1 CM = 5 MTR. NORTH

DRAWING NO. D.T.P. (K) 1735 / 2025 DATED- 22.07.2025

DRAWN BY: RAJNEESH KUMAR (TRACER)


CHECKED BY: DHAN RAM RANGA (JD) PARDEEP KUMAR (SD)

PLANNING ASSISTANT: RAMESH KUMAR (SD) MOHT, J.E.

ASSTT. TOWN PLANNER: MOHT SINGH, PATWARI

DISTT. TOWN PLANNER: SATISH KUMAR

DEPTT. OF TOWN & COUNTRY PLANNING HARYANA

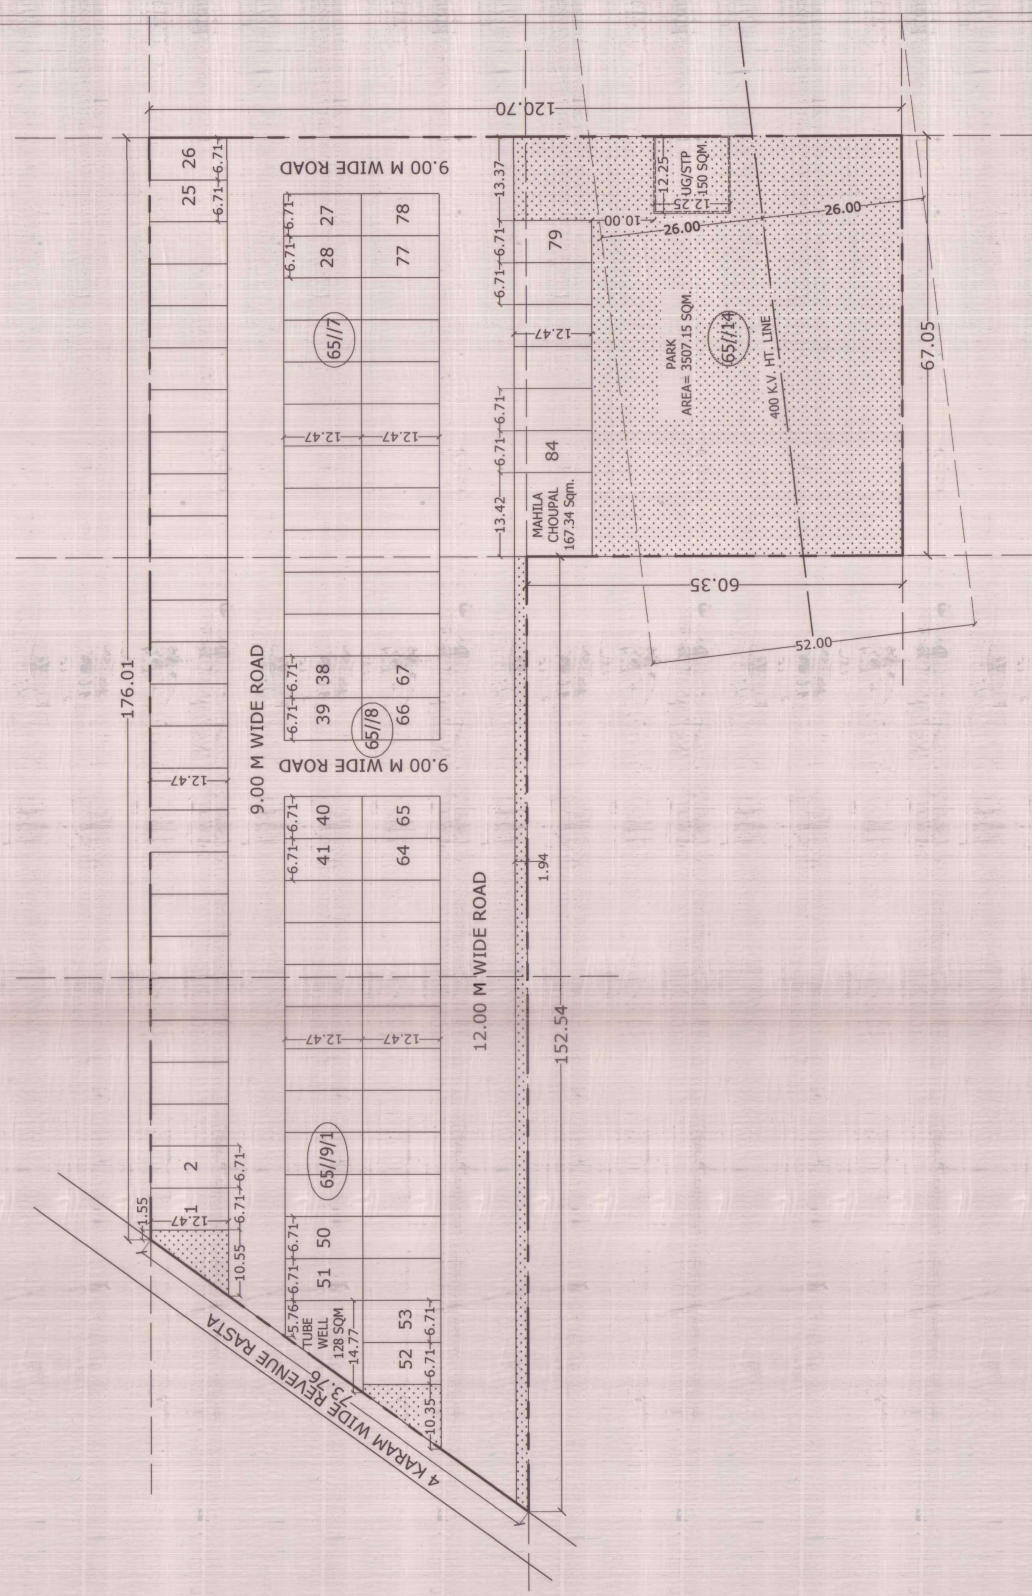

SUB DIVISIONAL OFFICER,  
PANCHAYATI RAJ DEPARTMENT,  
HARYANA, CHANDIGARH

B.D.P.O., INDRI BLOCK,  
DISTRICT KARNAL

CHAIRPERSON MMGAY-2.0, CUM,  
DISTRICT PANCHAYAT, HARYANA,  
TOWN & COUNTRY PLANNING DEPARTMENT,  
HARYANA, CHANDIGARH