

# KARNAL

LAYOUT PLAN OF HOUSING SCHEME UNDER "MUKHYAMANTRI GRAMIN AWAS YOJANA- EXTENSION" (MMGAY-E) AREA 3.00 ACRES COMPRISING IN KHASRA NOS. 30/7, 8 & 9 IN THE REVENUE ESTATE OF VILLAGE RAITH KHANA, BLOCK- INORI, DISTRICT KARNAL.

## DETAILS OF PLOTTED AREA:-

| SR. | PARTICULAR     | SIZE          | NOS. | AREA        |
|-----|----------------|---------------|------|-------------|
| 1.  | RES. PLOT      | 6.71X12.47 M  | 77   | 642.87 SQM. |
| 2.  | MAHILA CHOUHAL | 13.42X12.47 M | 1    | 167.34 SQM. |
| 3.  | TUBE WELL      | 6.57X12.47 M  | 1    | 81.92 SQM.  |

TOTAL PLOTTED AREA = 892.13 SQM. OR 1.86 ACRES

## DETAILS OF AREA:-

AREA OF SCHEME = 3 ACRES  
AREA UNDER ROADS / PARKS / OPEN SPACES = 1.55 ACRES (55%)  
= 1.35 ACRES

## LEGEND:-

SCHEME BOUNDARY

HT. LINE

KILA LINE

VILLAGE BOUNDARY

PARK / OPEN SPACES

## NOTES:-

- ALL DIMENSIONS ARE IN METERS.
- THIS LAYOUT PLAN HAS BEEN PREPARED ON THE BASIS OF THE KHASRA NOS. OF MMGAY-2.0 SCHEME FALLS OUTSIDE CONTROLLED AREA AND URBAN AREA OF DISTRICT KARNAL.
- THIS SITE DOES NOT FALL IN NCZ SURVEY REPORT APPROVED BY DLSC AND SENT TO SLIC.

SCALE: 1 CM = 5 MTR.

DRAWING NO. D.T.P. (K) 1754 / 2025 DATED- 22.07.2025

DRAWN BY:-

CHECKED BY:-

PLANNING ASSISTANT

ASST. TOWN PLANNER

DEPT. TOWN PLANNER

DEPT. OF TOWN & COUNTRY PLANNING HARYANA

APPROACH FROM 6 KARAM (10.06 MTR.) WIDE PANCHAYATI RASTA

11 K.V. HT. LINE (TO BE SHIFTED)

9 M WIDE ROAD

10.94 M WIDE ROAD

12 M WIDE ROAD

10.06

50.29

12.00

12.47

12.47

12.47

12.47


12.47

12.47

12.47

12.47

12.47

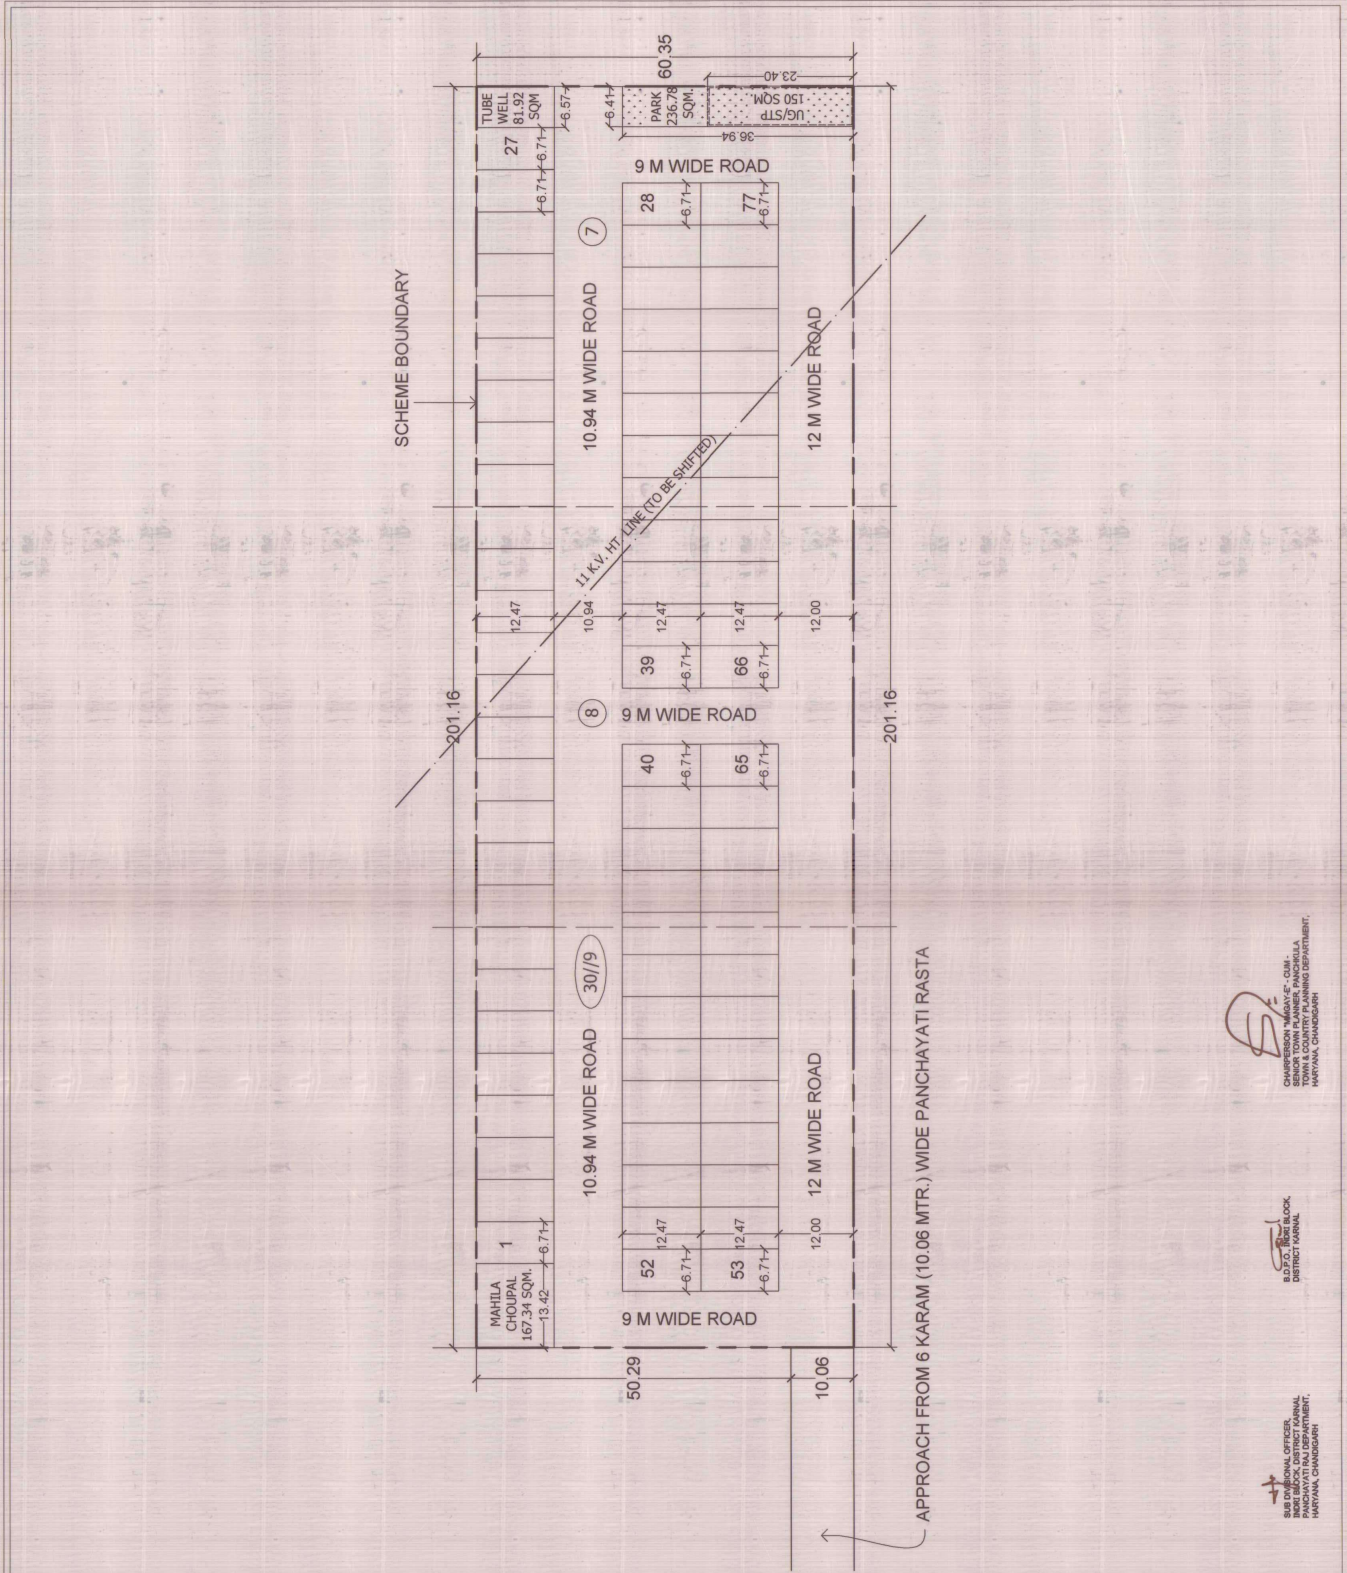

CHAIRPERSON "MMGAY-E" - CLM -  
DISTRICT OFFICE, KARNAL  
TOWN & COUNTRY PLANNING DEPARTMENT,  
HARYANA, CHANDIGARH

B.D.D. DIST. BLOCK,  
DISTRICT KARNAL

SUB DIVISIONAL OFFICER,  
DISTRICT KARNAL  
PANCHAYATI RAJ DEPARTMENT,  
HARYANA, CHANDIGARH